Eletrobras
APROVADO
Por: Cinthia Souza dos Santos Xavier em 30/10/2025

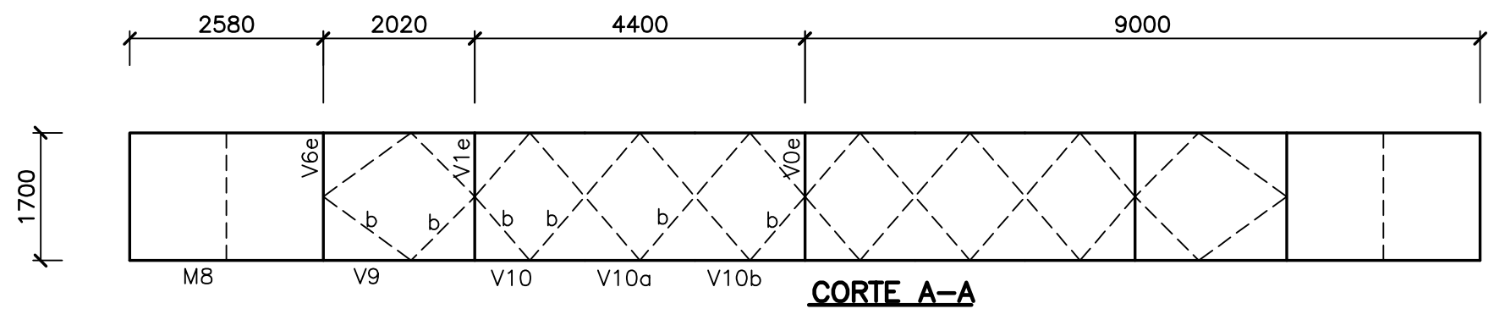

CORTE A-A

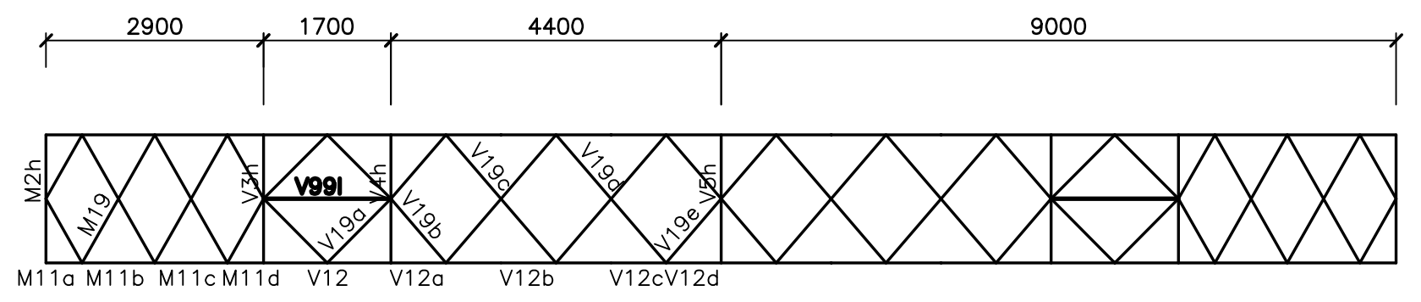

CORTE B-B

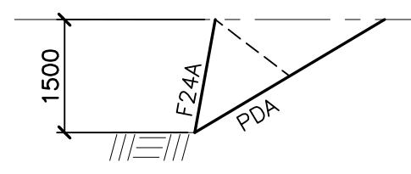

PÉ 1.5m

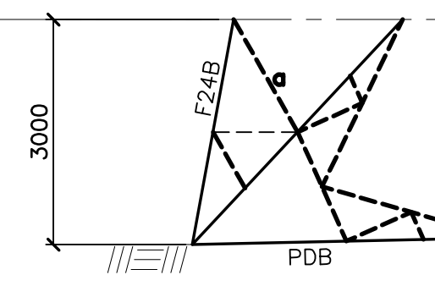

PÉ 3.0m

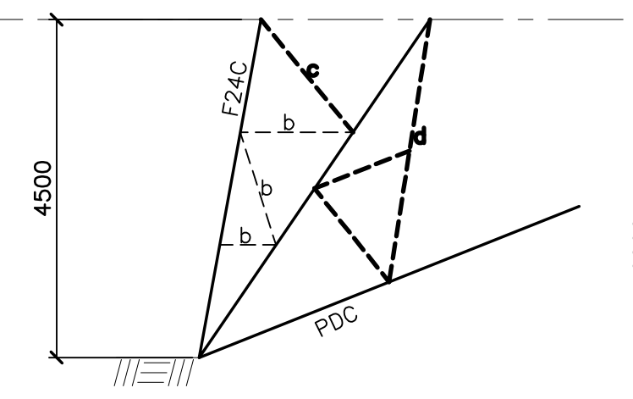

PÉ 4.5m

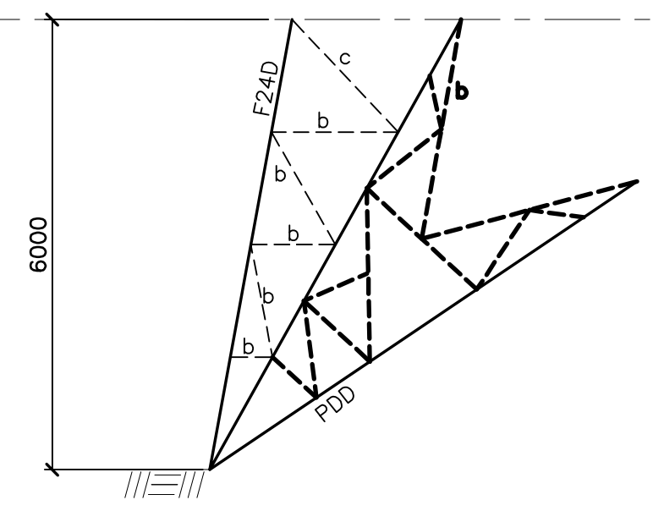

PÉ 6.0m

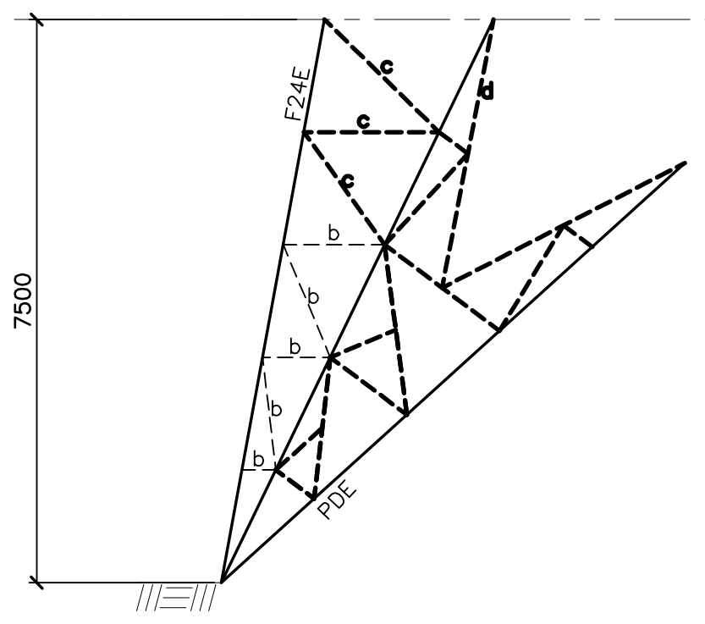

PÉ 7.5m

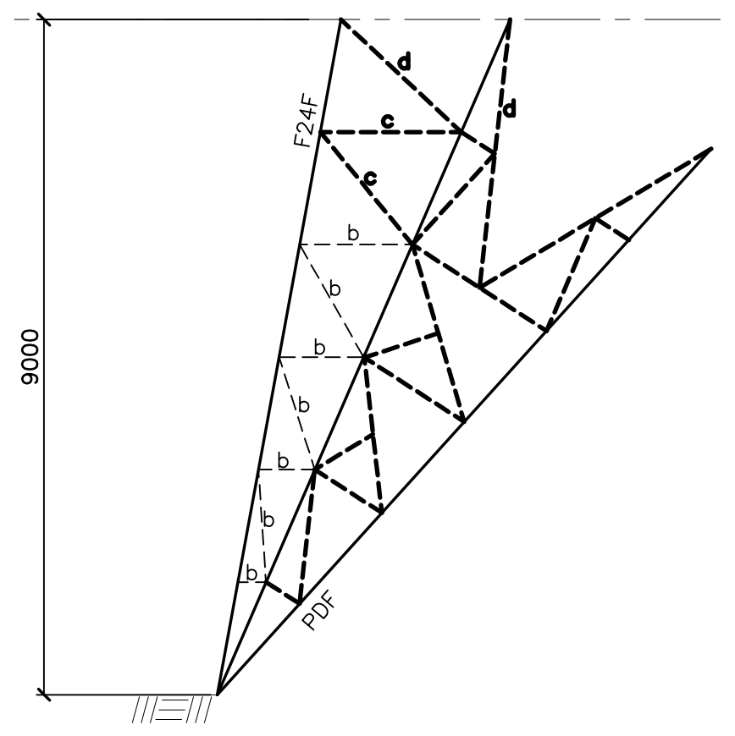

PÉ 9.0m

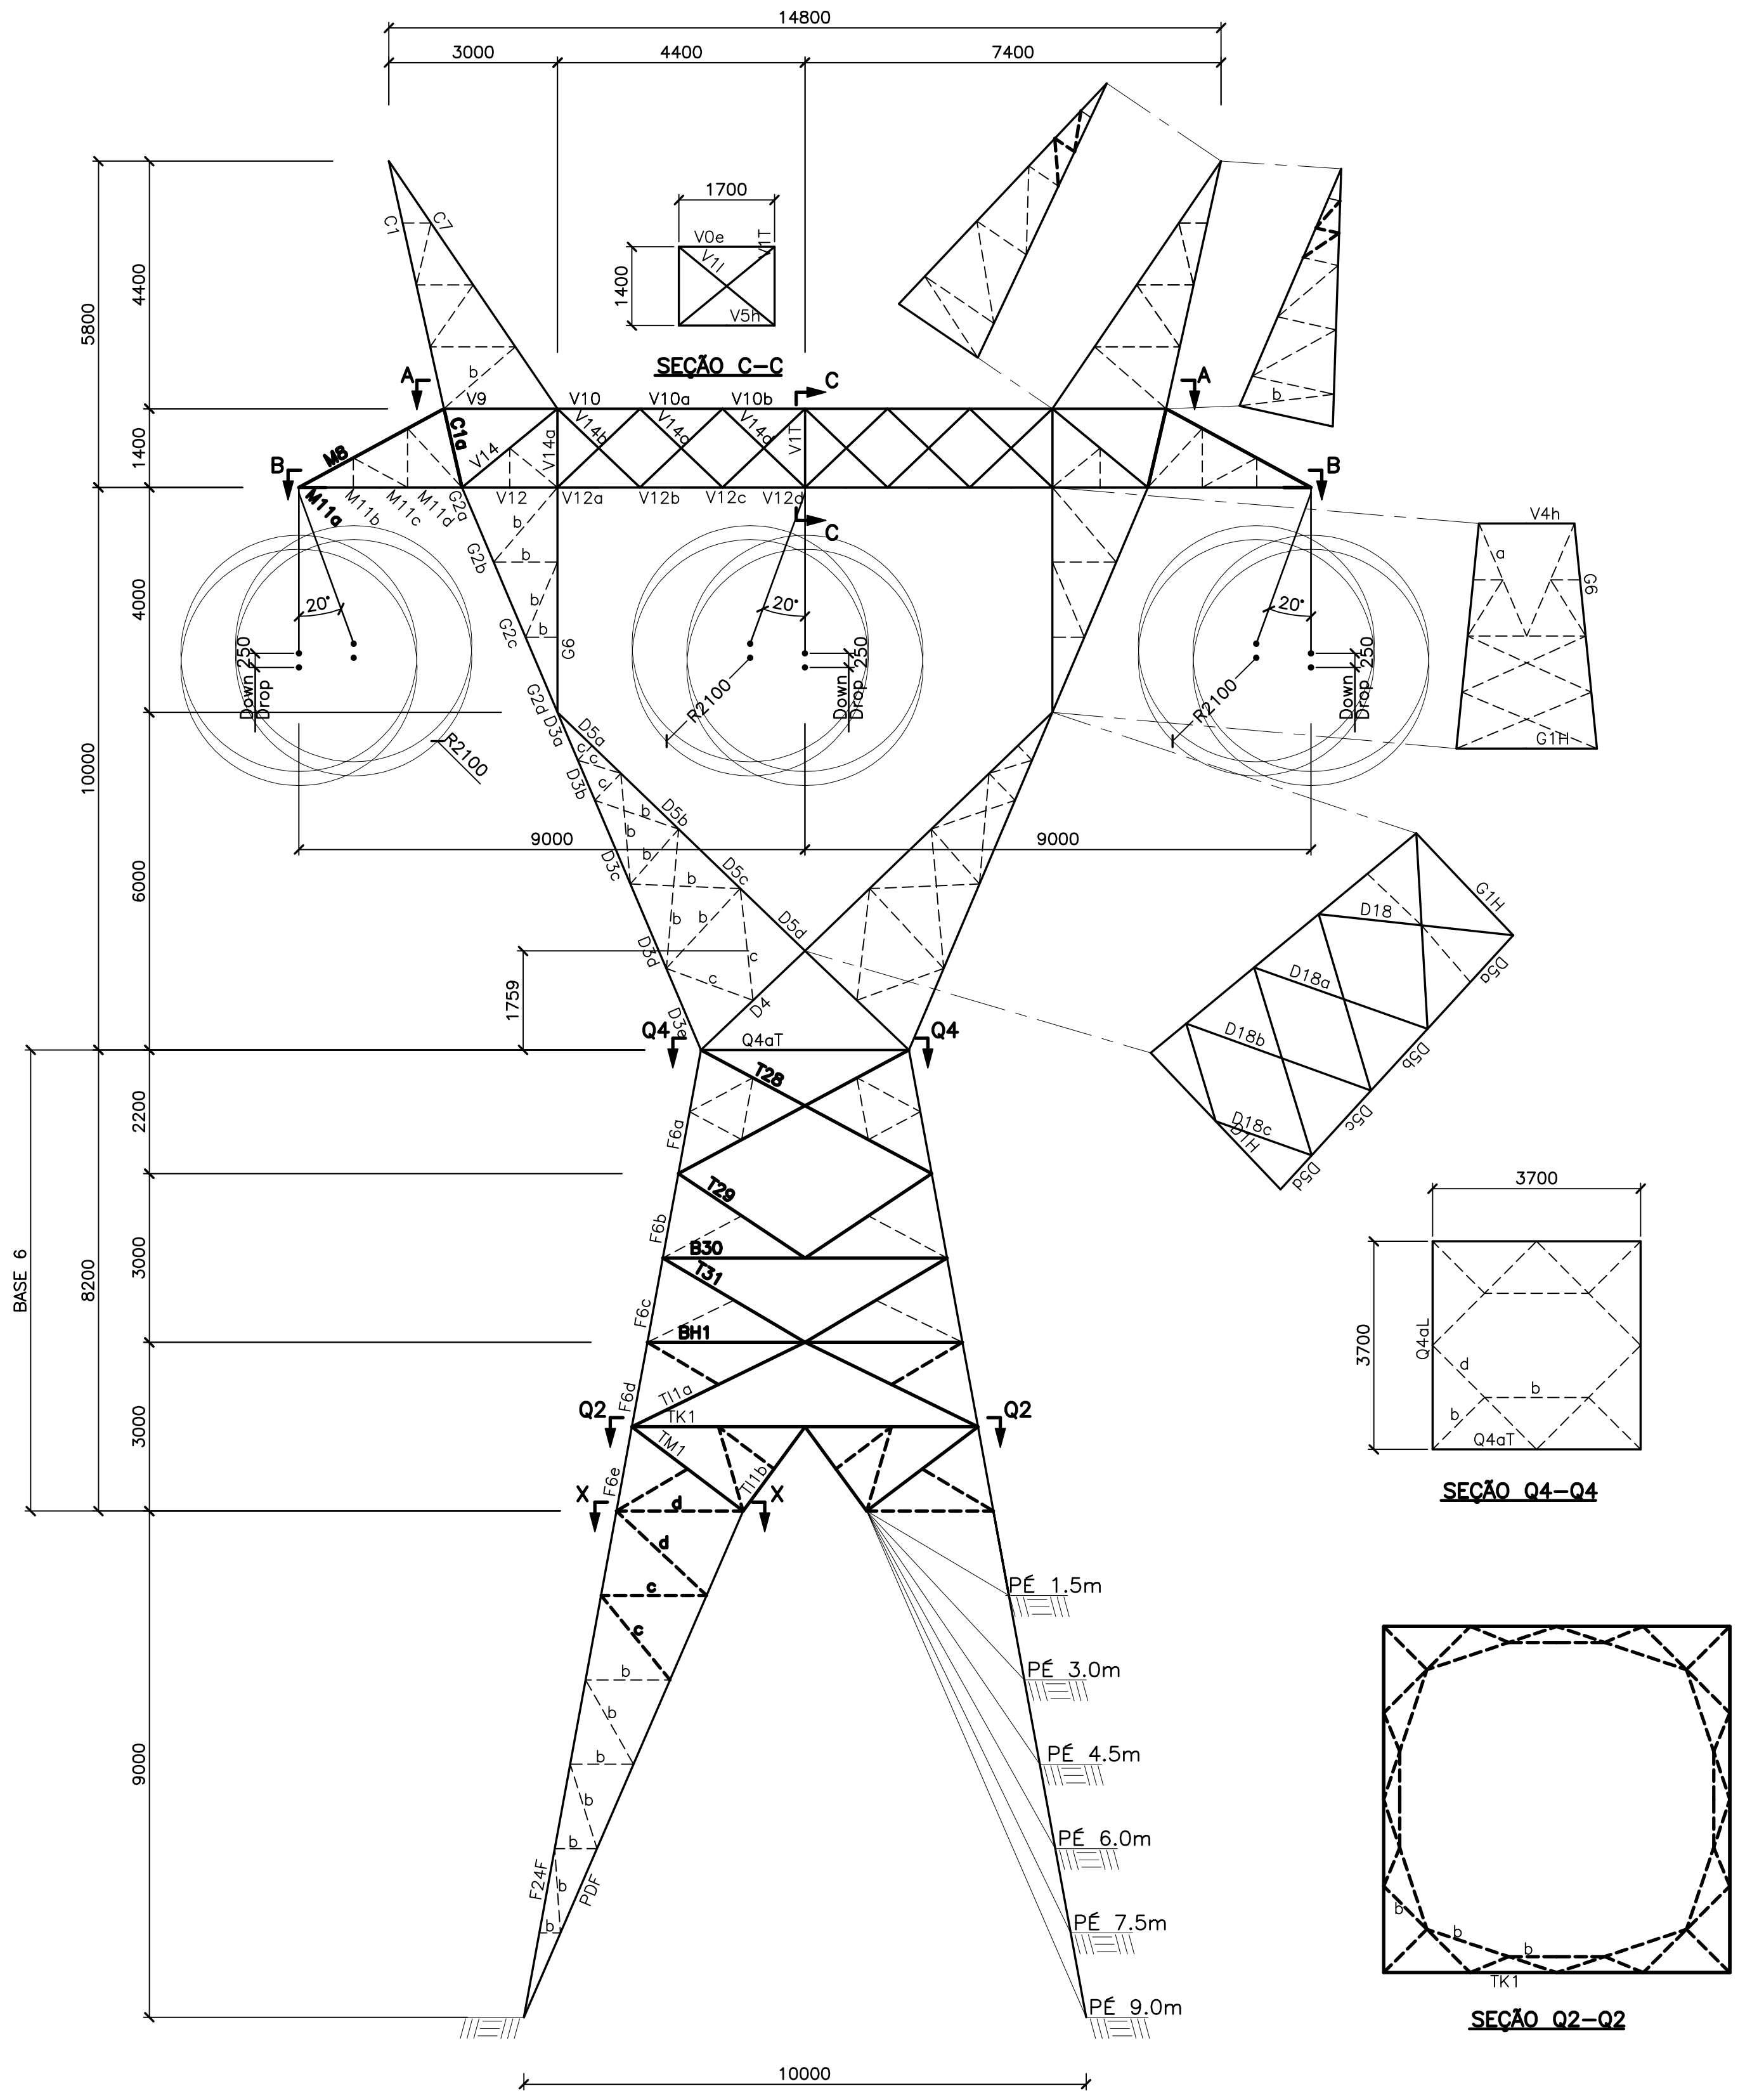

SEÇÃO C-C

SEÇÃO Q4-Q4

SEÇÃO Q2-Q2

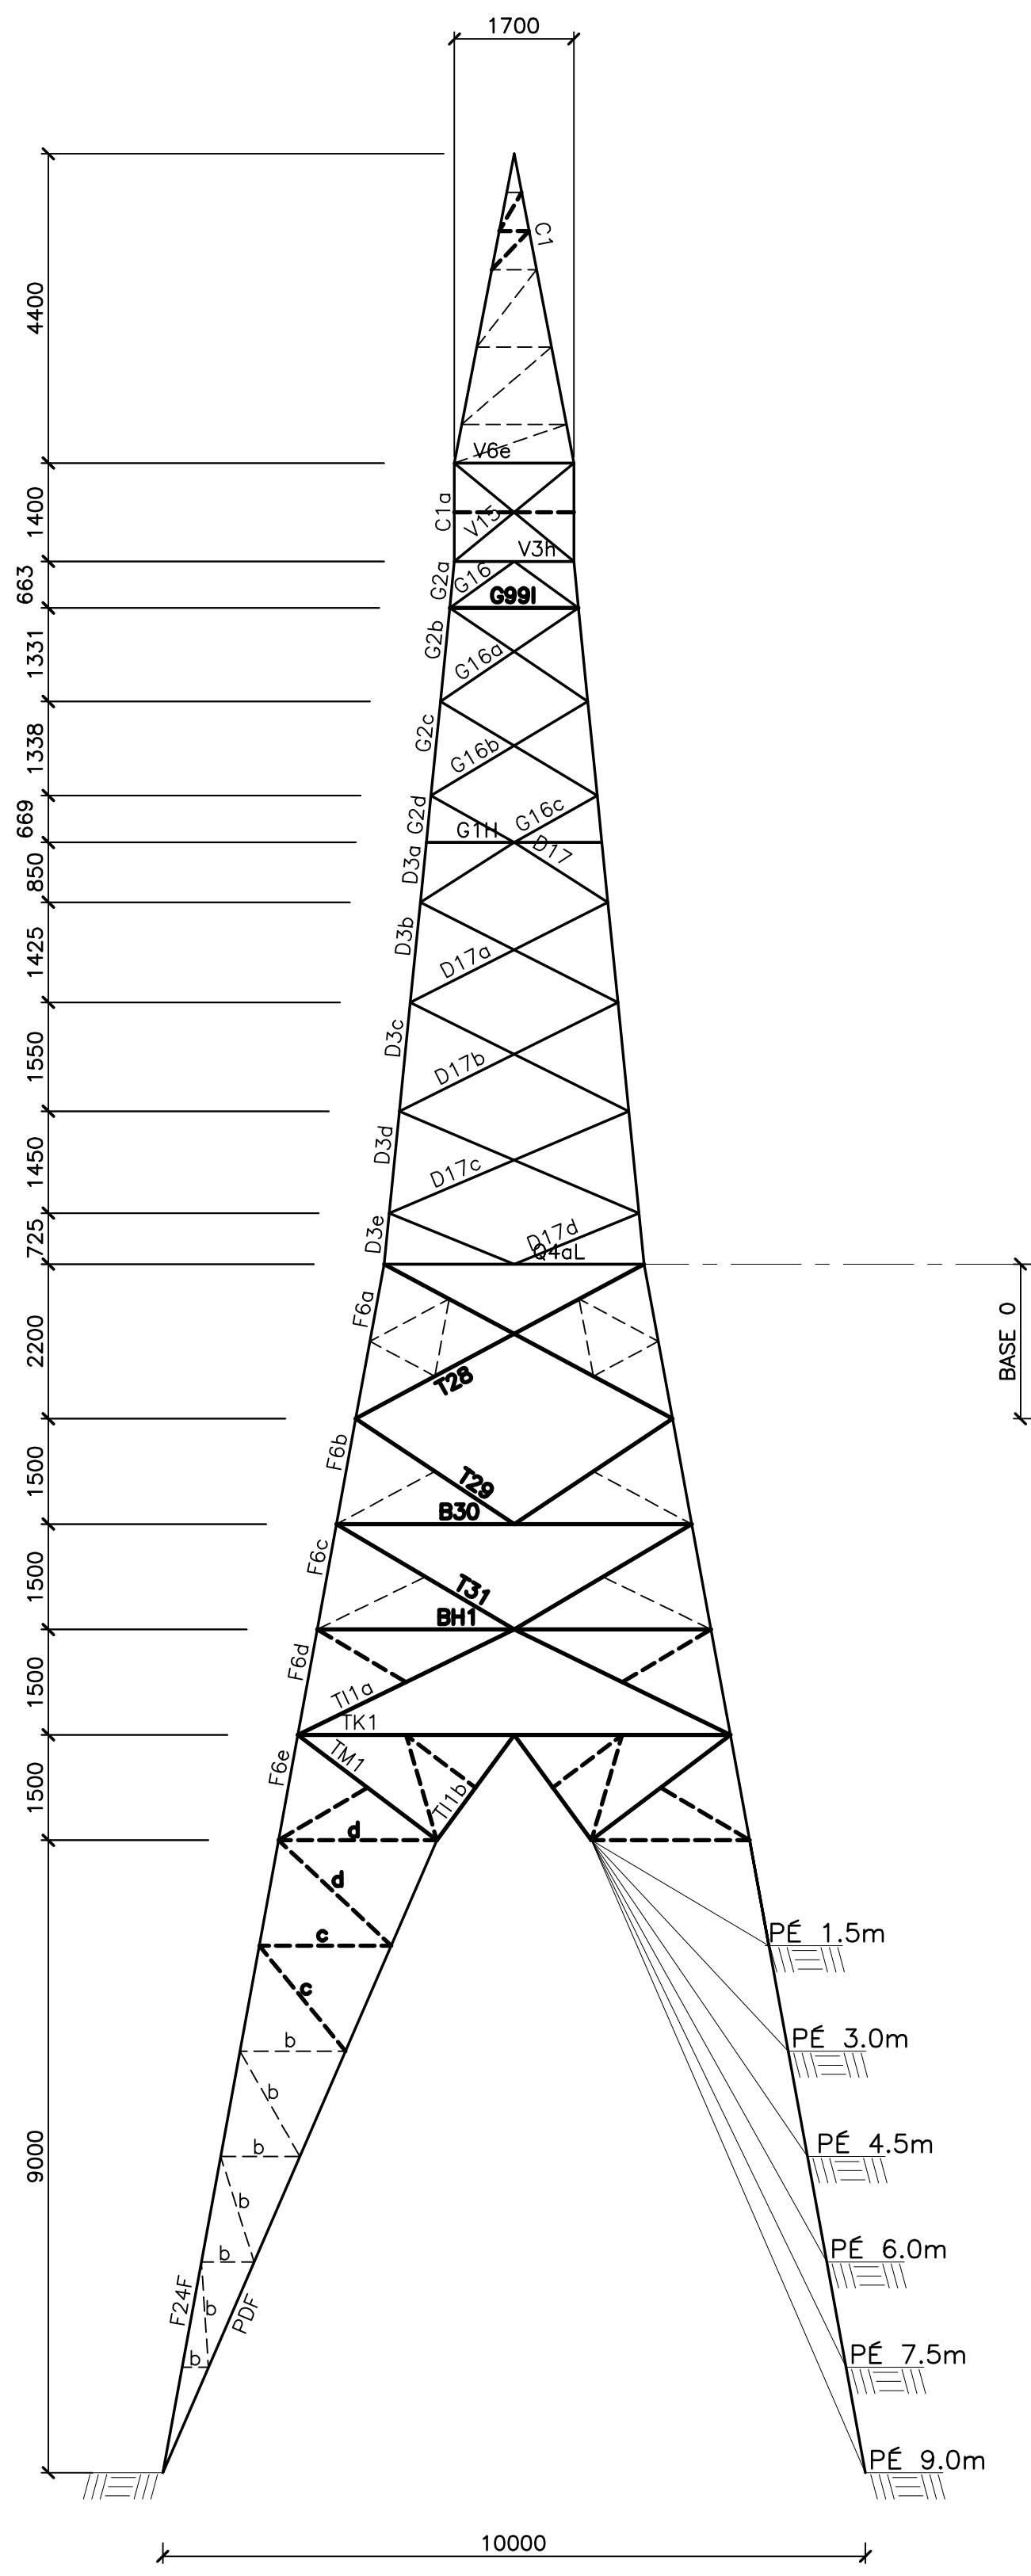

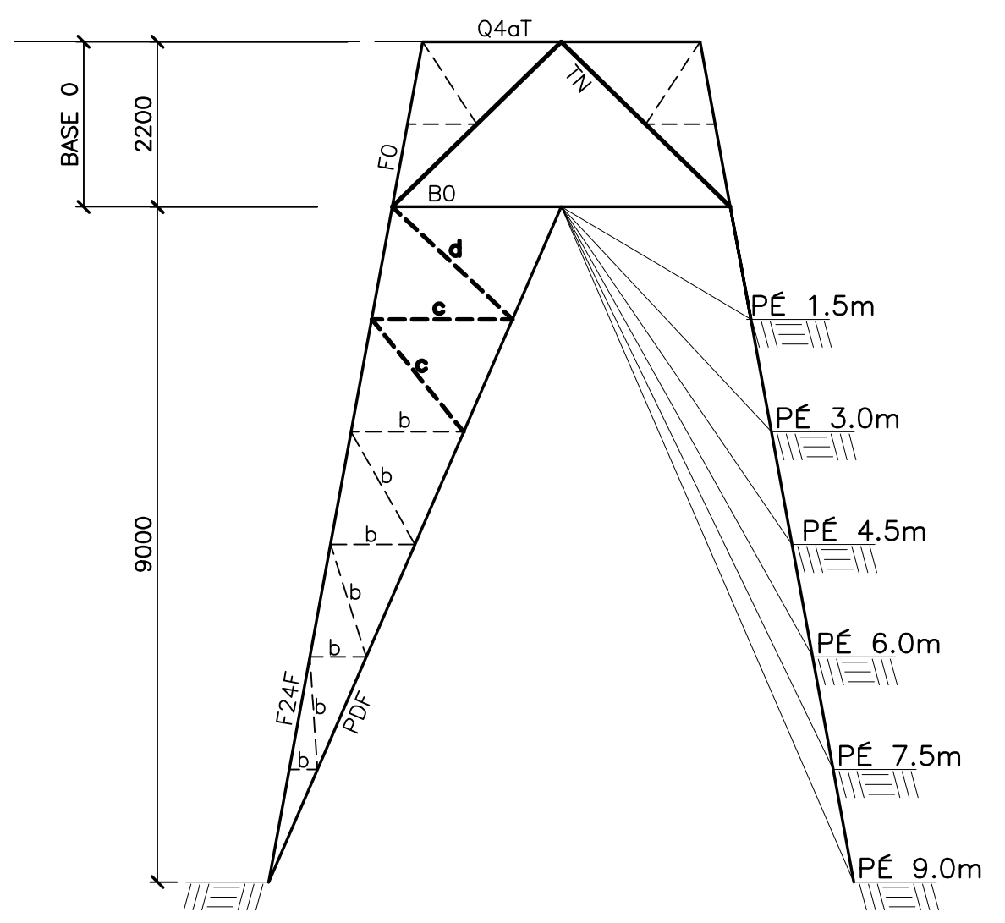

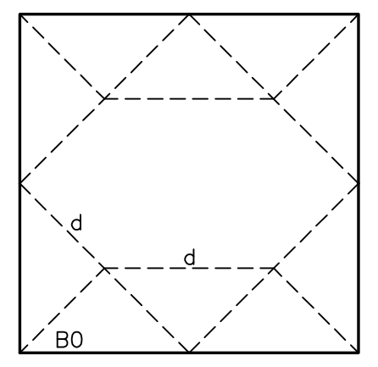

SEÇÃO Q0-Q0

TORRE AF2s - NOVA GEOMETRIA						
Barra	Posição	Dimensionamento		Dimensionamento Nova Geometria		
		Perfil	Ligação	Perfil	Ligação	Observação
M8	5,6	L 51 x 51 x 4.8	2 ϕ 12.7	L 51 x 51 x 4.8	3 ϕ 12.7	Acrés. Parafusos
M11a	7,8	L 64 x 64 x 4.8	3 ϕ 12.7	L 64 x 64 x 4.8	4 ϕ 12.7	Acrés. Parafusos
C1a	17,18	L 76 x 76 x 4.8	4 ϕ 15.9	L 76 x 76 x 4.8	4 ϕ 15.9	Contraventar Barra
G99l	Nova Posição			L 44 x 44 x 3.2	1 ϕ 12.7	Conforme Nova Geometria
V99l	Nova Posição			L 44 x 44 x 3.2	1 ϕ 12.7	Conforme Nova Geometria
TN	205	L 64 x 64 x 4.8	1 ϕ 12.7	L 76 x 76 x 4.8	3 ϕ 15.9	Substituir Perfil, Acrés. Parafusos
PDF	286, 287,312 : 315	L 76 x 76 x 6.4	3 ϕ 12.7	L 76 x 76 x 6.4	3 ϕ 15.9	Contraventar Vista, Substituir Parafuso
PDA	251	L 64 x 64 x 4.8	2 ϕ 12.7	L 76 x 76 x 4.8	3 ϕ 15.9	Substituir Perfil, Substituir Parafuso
T28	217	L 51 x 51 x 4.8	1 ϕ 12.7	L 64 x 64 x 4.8	2 ϕ 12.7	Substituir Perfi, Acrés. Parafusos
T29	218	L 51 x 51 x 4.8	1 ϕ 12.7	L 64 x 64 x 4.8	2 ϕ 12.7	Substituir Perfi, Acrés. Parafusos
B30	220	L 76 x 76 x 4.8	1 ϕ 12.7	L 76 x 76 x 4.8	2 ϕ 12.7	Acrés. Parafusos
T31	221	L 51 x 51 x 4.8	1 ϕ 12.7	L 64 x 64 x 4.8	2 ϕ 12.7	Substituir Perfil, Acrés. Parafusos
BH1	223	L 76 x 76 x 4.8	1 ϕ 12.7	L 76 x 76 x 4.8	2 ϕ 12.7	Acrés. Parafusos
TI1A	Nova Posição			L 76 x 76 x 4.8	2 ϕ 12.7	Conforme Nova Geometria
TK1	Nova Posição			L 64 x 64 x 4.8	2 ϕ 12.7	Conforme Nova Geometria
TI1b	Nova Posição			2L44x 44 x 4.8	2*2 ϕ 12.7	Conforme Nova Geometria
PDB	254	L 76 x 76 x 4.8	2 ϕ 12.7	L 76 x 76 x 4.8	3 ϕ 15.9	Contraventar Vista, Substituir Parafuso
PDC	258	L 76 x 76 x 4.8	2 ϕ 12.7	L 76 x 76 x 4.8	3 ϕ 15.9	Contraventar Vista, Substituir Parafuso
PDD	266 : 268	L 76 x 76 x 4.8	3 ϕ 12.7	L 76 x 76 x 4.8	3 ϕ 15.9	Contraventar Vista, Substituir Parafuso
PDE	282 : 287	L 76 x 76 x 6.4	3 ϕ 12.7	L 76 x 76 x 6.4	3 ϕ 15.9	Contraventar Vista, Substituir Parafuso
Aletas	359	L 127 x 127 x 9.5	4 ϕ 15.9	L 127 x 127 x 9.5	4 ϕ 15.9	Comprimento e Quantidade

OS MATERIAIS UTILIZADOS NOS AÇOS A SEREM UTILIZADOS NAS CHAPAS, TRELIÇAS E PARAFUSOS DEVERÃO SER DESIGNADOS CONFORME ITENS 8.1 e 8.3 DO MEMORIAL DE CÁLCULO PARA TODA A TORRE, INCLUSIVE NAS PARTES QUE NÃO FORAM OBJETO DE REFORÇO ESTRUTURAL ESPECÍFICO.

1 – Todas as cotas estão em milímetros.
2 – Para memória de cálculo ver doc. AF2s_ADR2451–M2001
3. Barras descarregadas:
Não indicadas: L38x38x3,2H – 1ø12.7
a) L38x38x4,8H – 1ø12.7
b) L44x44x3,2H – 1ø12.7
c) L44x44x4,8H – 1ø12.7
d) L51x51x4,8H – 1ø12.7
e) L64x64x4,8H – 1ø12.7

NOTAS

N°_DO_DOCUMENTO	TÍTULO DO DOCUMENTO DE REFERÊNCIA
NÚMERO	TÍTULO

DOCUMENTOS DE REFERÊNCIA

REV.	DESCRIÇÃO	DATA	ELABORAÇÃO	VERIFICAÇÃO
00	APROVADO	16/10/2025	ARTHUR SANTOS	MICHAEL RODRIGUES
00D	CONFORME COMENTÁRIOS	01/10/2025	MICHAEL RODRIGUES	MICHAEL RODRIGUES
00C	CONFORME COMENTÁRIOS	09/09/2025	ARTHUR SANTOS	MICHAEL RODRIGUES
00B	CONFORME NOVA GEOMETRIA	21/07/2025	ARTHUR SANTOS	CRISTINA CASSIMIRO
00A	EMISSÃO INICIAL	15/07/2025	ARTHUR SANTOS	CRISTINA CASSIMIRO

N° CR GONTIJO
AF2s_ADR2451–D4001

PROPRIEDADE
Eletrobras
SPE Nova Era Integração Transmissora S.A.

AUTORIA
AG CONSAG ENGENHARIA
CONSÓRCIO CONSTRUTOR SÃO FRANCISCO
CR GONTIJO
ENGENHARIA DE PROJETOS

APROVAÇÃO
HENRIQUE GONTIJO
RESPONSÁVEL
TÉCNICO
CREA 108382/MG

RESPONSÁVEL TÉCNICO

LOTE 05 – ANEEL 01/2024

DESCRIÇÃO DESENHO

TORRE DE ANCORAGEM/TERMINAL TIPO AF2s

SILHUETA

DESCRIÇÃO PROJETO

NOVA ERA INTEGRAÇÃO

LOTE 5 – LT 230 kV
SECCIONAMENTO DA LT 230 kV MILAGRES – CRATO II NA SE ABAIARA

CÓDIGO PROJETO	FORMATO	N° DESENHO	
LTNEI	A0	**LTRD1.01–230–PE–EM.DDM–0004**	
CLASSIFICAÇÃO	ESCALA	FOLHA	REVISÃO
EXECUTIVO.BÁSICO.PADRÃO	1/100	1	00