
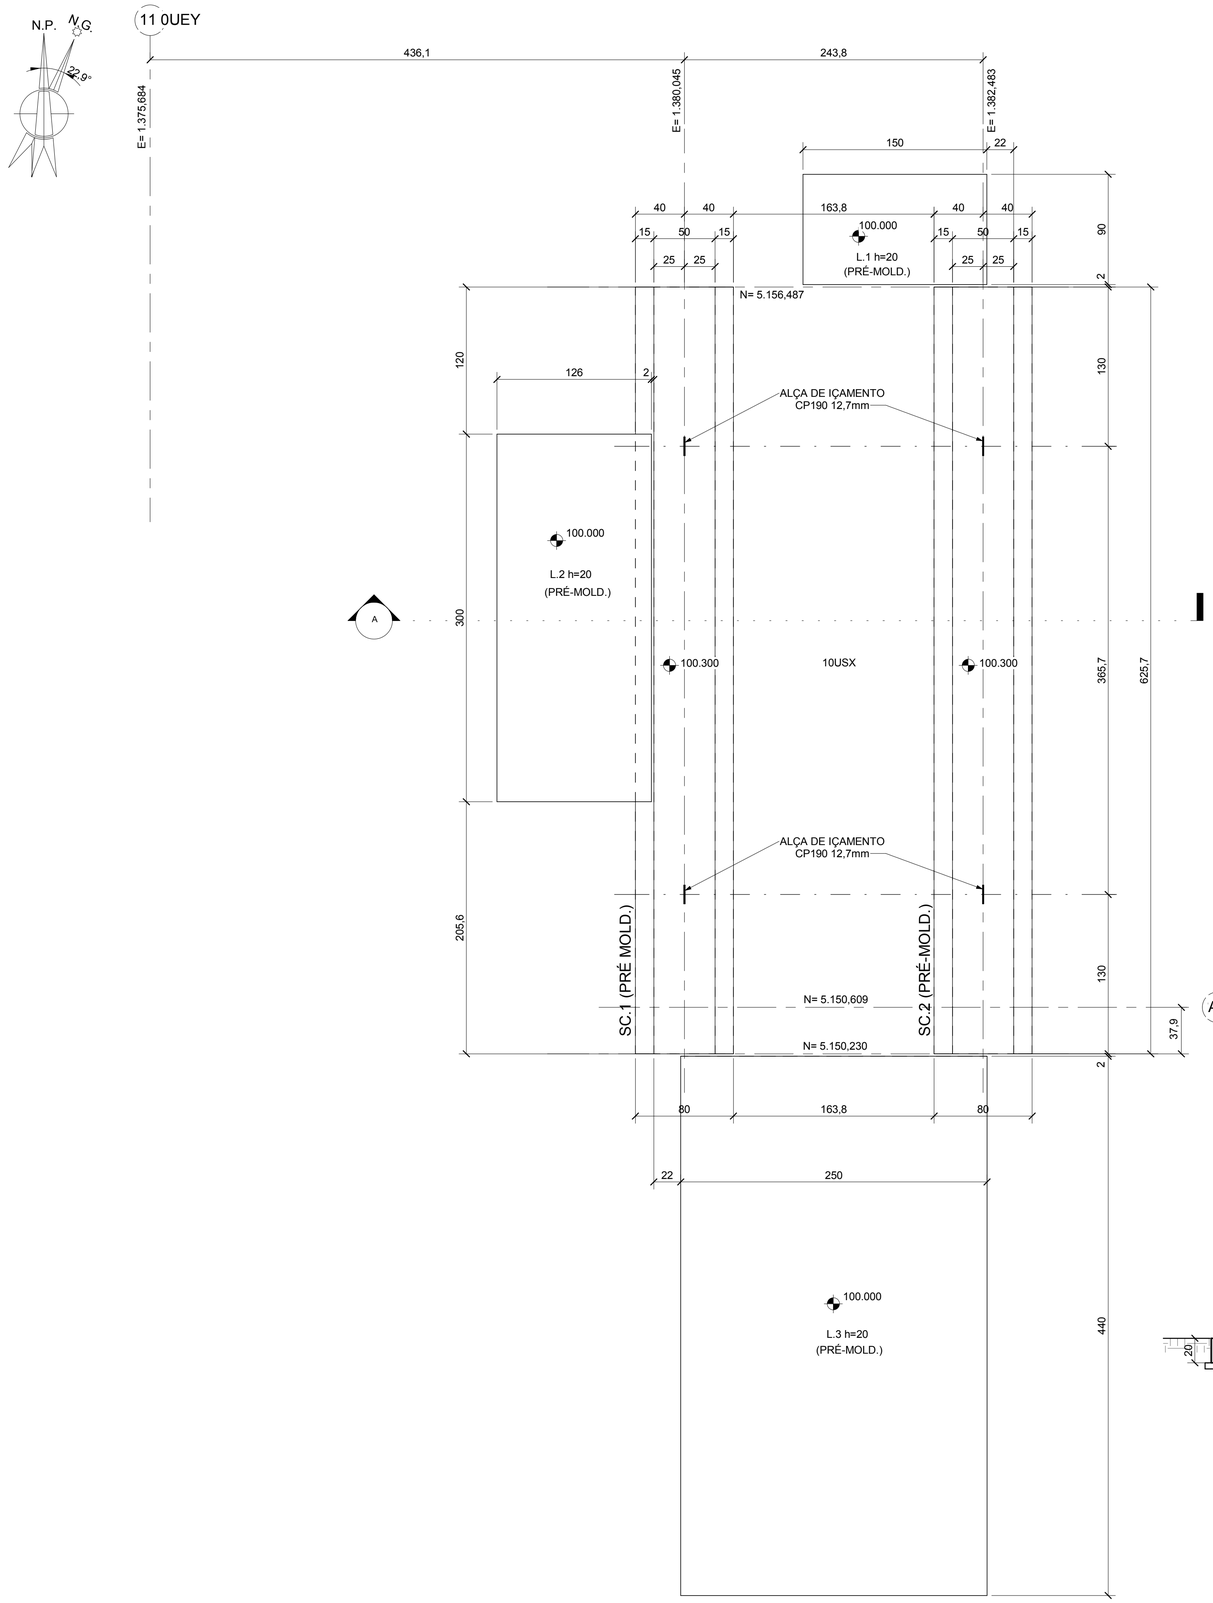



## PLANTA DA BASE - LOCAÇÃO


ESCALA: 1 : 25

| TRANSFORMAÇÃO DE COORDENADAS | |
|---|---|
| COORDENADAS DE PROJETO | COORD. UTM SIRGAS 2000 |
| E: 1.000,000 | X = 291.392,622 |
| N: 5.000,000 | Y = 7.582.694,937 |
| **TRANSFORMAÇÃO DE ELEVAÇÃO** | |
| ELEVAÇÃO | ELEVAÇÃO EM RELAÇÃO AO NÍVEL MÉDIO DO MAR |
| +100,000 (m) | +5,200 (m) |

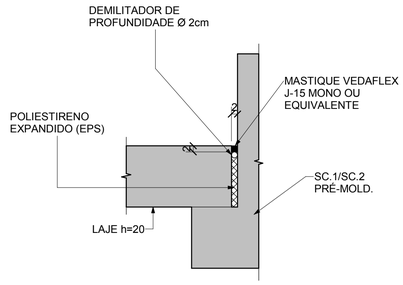



## DET. 1 - JE (TÍP.)

| JUNTA DE ENCONTRO (JE) | |
|---|---|
| MASTIQUE VEDAFLEX J-15 MONO OU EQUIV. | 4,0 m. |
| DEMILITADOR DE PROFUNDIDADE Ø 2cm | |
| POLIESTIRENO EXPANDIDO (EPS) | |

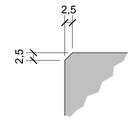


## CHANFRO EM ARESTAS-DET.TIP

ESCALA: 1 : 10

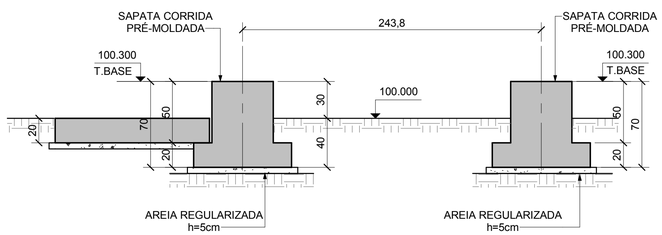


## CORTE A

ESCALA: 1 : 25

## DOCUMENTOS DE REFERÊNCIA:

BR1045-10QCD10-&MLH020-445128 - MS2 INPUT FOR AMMONIA DOSING SYSTEM
NOVO-SRCA-SP-0004-CIVIL - ESPECIFICAÇÃO TÉCNICA PARA CIVIL E ARQUITETURA
NOVO-SRCA-SP-0003 - ESPECIFICAÇÃO TÉCNICA DE TERRAPLENAGEM
NOVO-SRCA-CD-0001 - CRITÉRIOS DE PROJETO CIVIL
BR1045-11UEN-&CLH011-633014-STRUCTURE FOR FUEL GAS REDUCING

## NOTAS

1 - MEDIDAS EM CENTÍMETRO, BITOLAS EM MILÍMETRO, NÍVEIS E COORDENADAS EM METRO, EXCETO ONDE INDICADO.

2 - MATERIAIS :

- CONCRETO ESTRUTURAL C30 fck ≥ 30MPa
- CONCRETO MAGRO C10 fck ≥ 10MPa.
- RELAÇÃO a/c (ÁGUA/CIMENTO) ≤ 0,50 CLASSE DE AGRESSIVIDADE III
- CONSUMO DE CIMENTO ≥ 320 kg/m³
- MÓDULO DE ELASTICIDADE Ecs ≥ 26,8 GPa (AGREGADO GRAÚDO-GNAISSE)

- AÇO CA-50 fyk≥500 MPa.

- PARA TRANSPORTE, MANUSEIO E DESFORMA:
  fcj >= 20 MPa
  Ecs >= 21 GPa

- PARA A ALÇA: CORDOALHA CP 190 RB 12,7mm

3 - PARA CONTROLE TECNOLÓGICO DO CONCRETO SEGUIR RIGOROSAMENTE AS ESPECIFICAÇÕES DA NBR 12655 "CONCRETO-PREPARO, CONTROLE E RECEBIMENTO".

4 - A TENSÃO APLICADA NA COTA DE APOIO NA FUNDAÇÃO DIRETA É DE 0,45kgf/cm².

| REV. | DESCRIÇÃO | DATA | DES. | VERIF. | APROV. |
|---|---|---|---|---|---|
| | | | | | |
| | | | | | |
| 2 | REVISÃO ONDE INDICADO/EMITIDO PARA CONSTRUÇÃO | 30-07-18 | J.K.Y. | M.P.R. | E.R.P. |
| 1 | REVISÃO ONDE INDICADO/EMITIDO PARA CONSTRUÇÃO | 17-07-18 | J.K.Y. | M.P.R. | E.R.P. |
| 0 | EMISSÃO INICIAL / EMITIDO PARA CONSTRUÇÃO | 22-06-18 | G.P.V. | M.P.R. | E.R.P. |

**REVISÕES**

CONTRATANTE: SIEMENS / ANDRADE GUTIERREZ CONSÓRCIO ADJ

ENGENHARIA SUBCONTRATADA: SENER

CLIENTE: **UTE GNA I** Gás Natural Açu S.A.

© SENER, SETE PLA TECNOMETAL ENGENHARIA E SISTEMAS S.A.
AS INFORMAÇÕES CONTIDAS NESTE DOCUMENTO SÃO CONFIDENCIAIS E RESTRITAS, E DEVEM SER UTILIZADAS SOMENTE PARA FINS ESTABELECIDOS NO DOCUMENTO. MODIFICAÇÃO, EXPLORAÇÃO, REPRODUÇÃO, COMUNICAÇÃO A QUALQUER TERCEIRO, EXPLORAÇÃO OU DISTRIBUIÇÃO DE TODO OU QUALQUER PARTE DO DOCUMENTO NÃO É PERMITIDO SEM O CONSENTIMENTO PRÉVIO POR ESCRITO DA SENER SETE PLA TECNOMETAL ENGENHARIA E SISTEMAS S.A. A FALTA DE RETORNO SOBRE TAL CONSENTIMENTO NÃO DEVE, EM HIPÓTESE ALGUMA, SER INTERPRETADA COMO AUTORIZAÇÃO PARA USO DA INFORMAÇÃO.

| | |
|---|---|
| No ARQUIVO CAD : | NOVO-SRCA-PC-0509-01 Rev 2 |
| ESCALA : | |
| REFERÊNCIA : | P0Q27003 |
| TAMANHO ORIGINAL | A1 |
| PROJETO: | UTE GNA I<br>PLANTA DE CICLO COMBINADO<br>PORTO DO AÇU - RIO DE JANEIRO |
| No DESENHO SUBCONTRATADA: | NOVO-SRCA-PC-0509 |
| No DESENHO CLIENTE: | |
| No DESENHO SAG: | BR1045-30710-&CLB020-102139 |
| TÍTULO DO DESENHO: | FUNDAÇÃO DO SISTEMA DE DOSAGEM<br>*DOSING SYSTEM FOUNDATION - FORMS/STEEL REINFORCEMENT*<br>LOCAÇÃO DA FUNDAÇÃO |
| FL. | 01 |
| PRÓX. | 02 |

DIN A1 ( 841 x 594 )