Eletrobras
APROVADO
Por: Diogo Ferreira em 04/08/2026

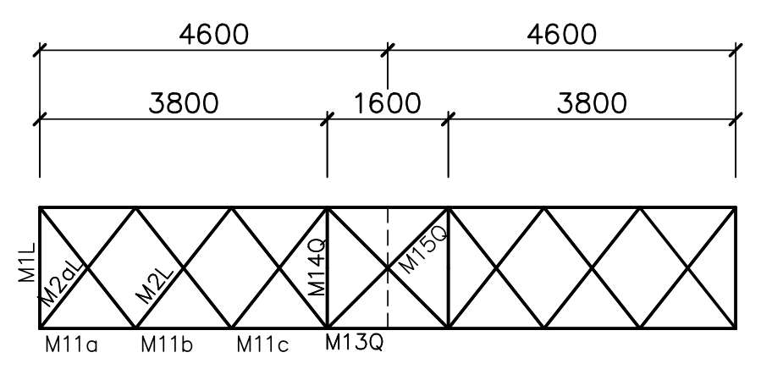

CORTE B-B

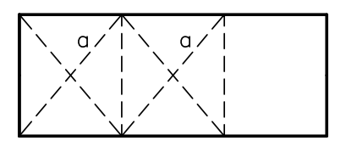

VISTA F

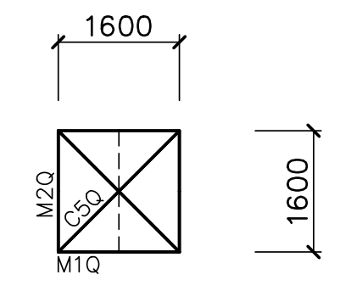

CORTE C-C

DEFLEXÃO 30°

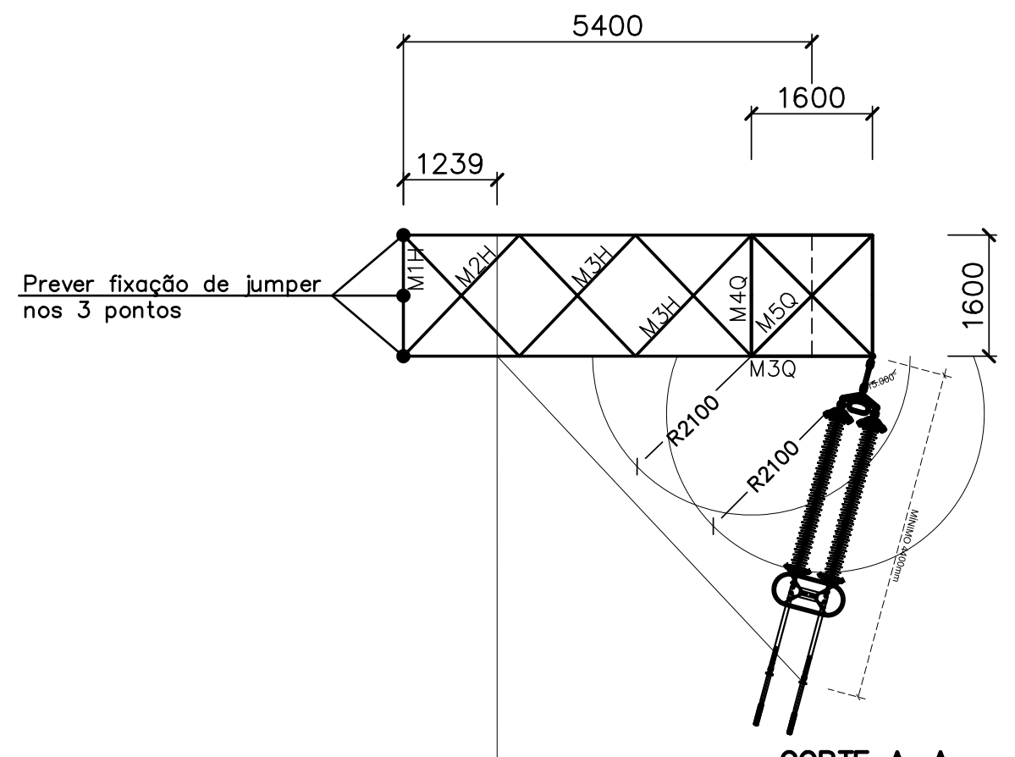

CORTE A-A

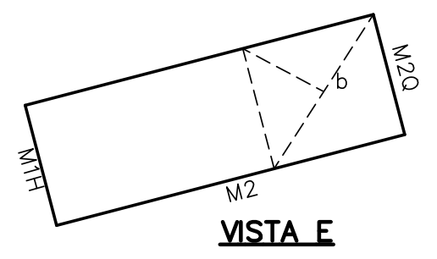

VISTA E

Pontos de fixação da cadeia de ancoragem da fase superior. Montagem sempre do lado oposto à mísula de jumper.

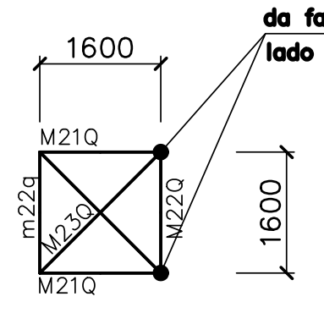

CORTE D-D

PARA TORRE EM ALINHAMENTO e ATÉ 30°: devem ser usadas duas cadeias de suspensão do jumper

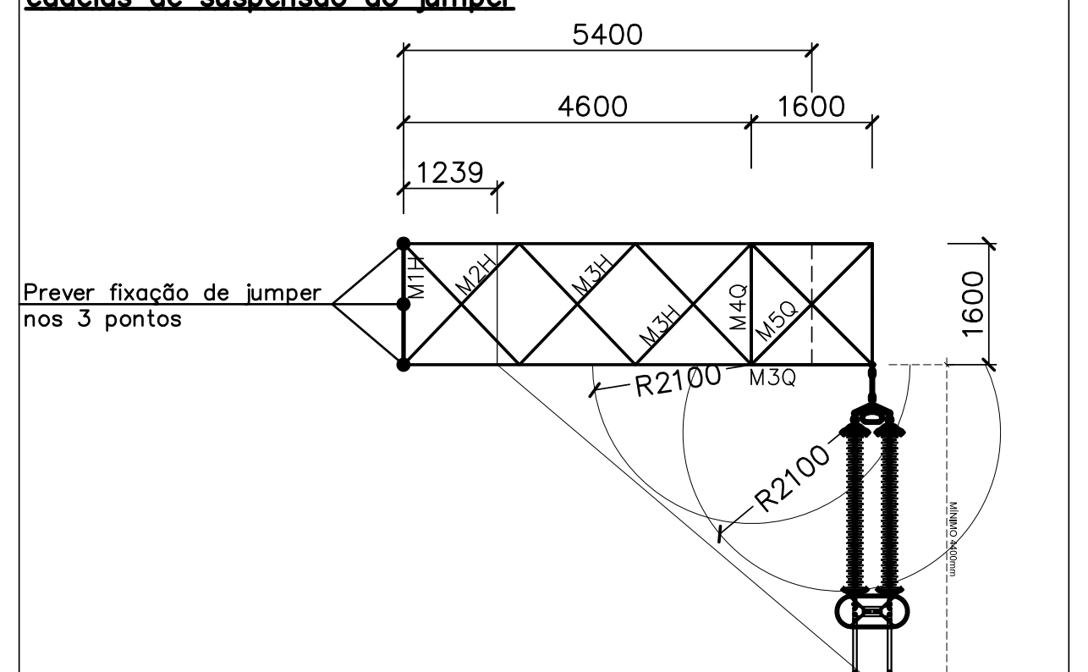

CORTE A-A

Mísula para fixação da cadeia de jumper da fase superior. Montada sempre internamente ao ângulo de deflexão da LT.

Ponto de fixação da cadeia de ancoragem da fase superior. Montagem sempre do lado oposto à mísula de jumper.

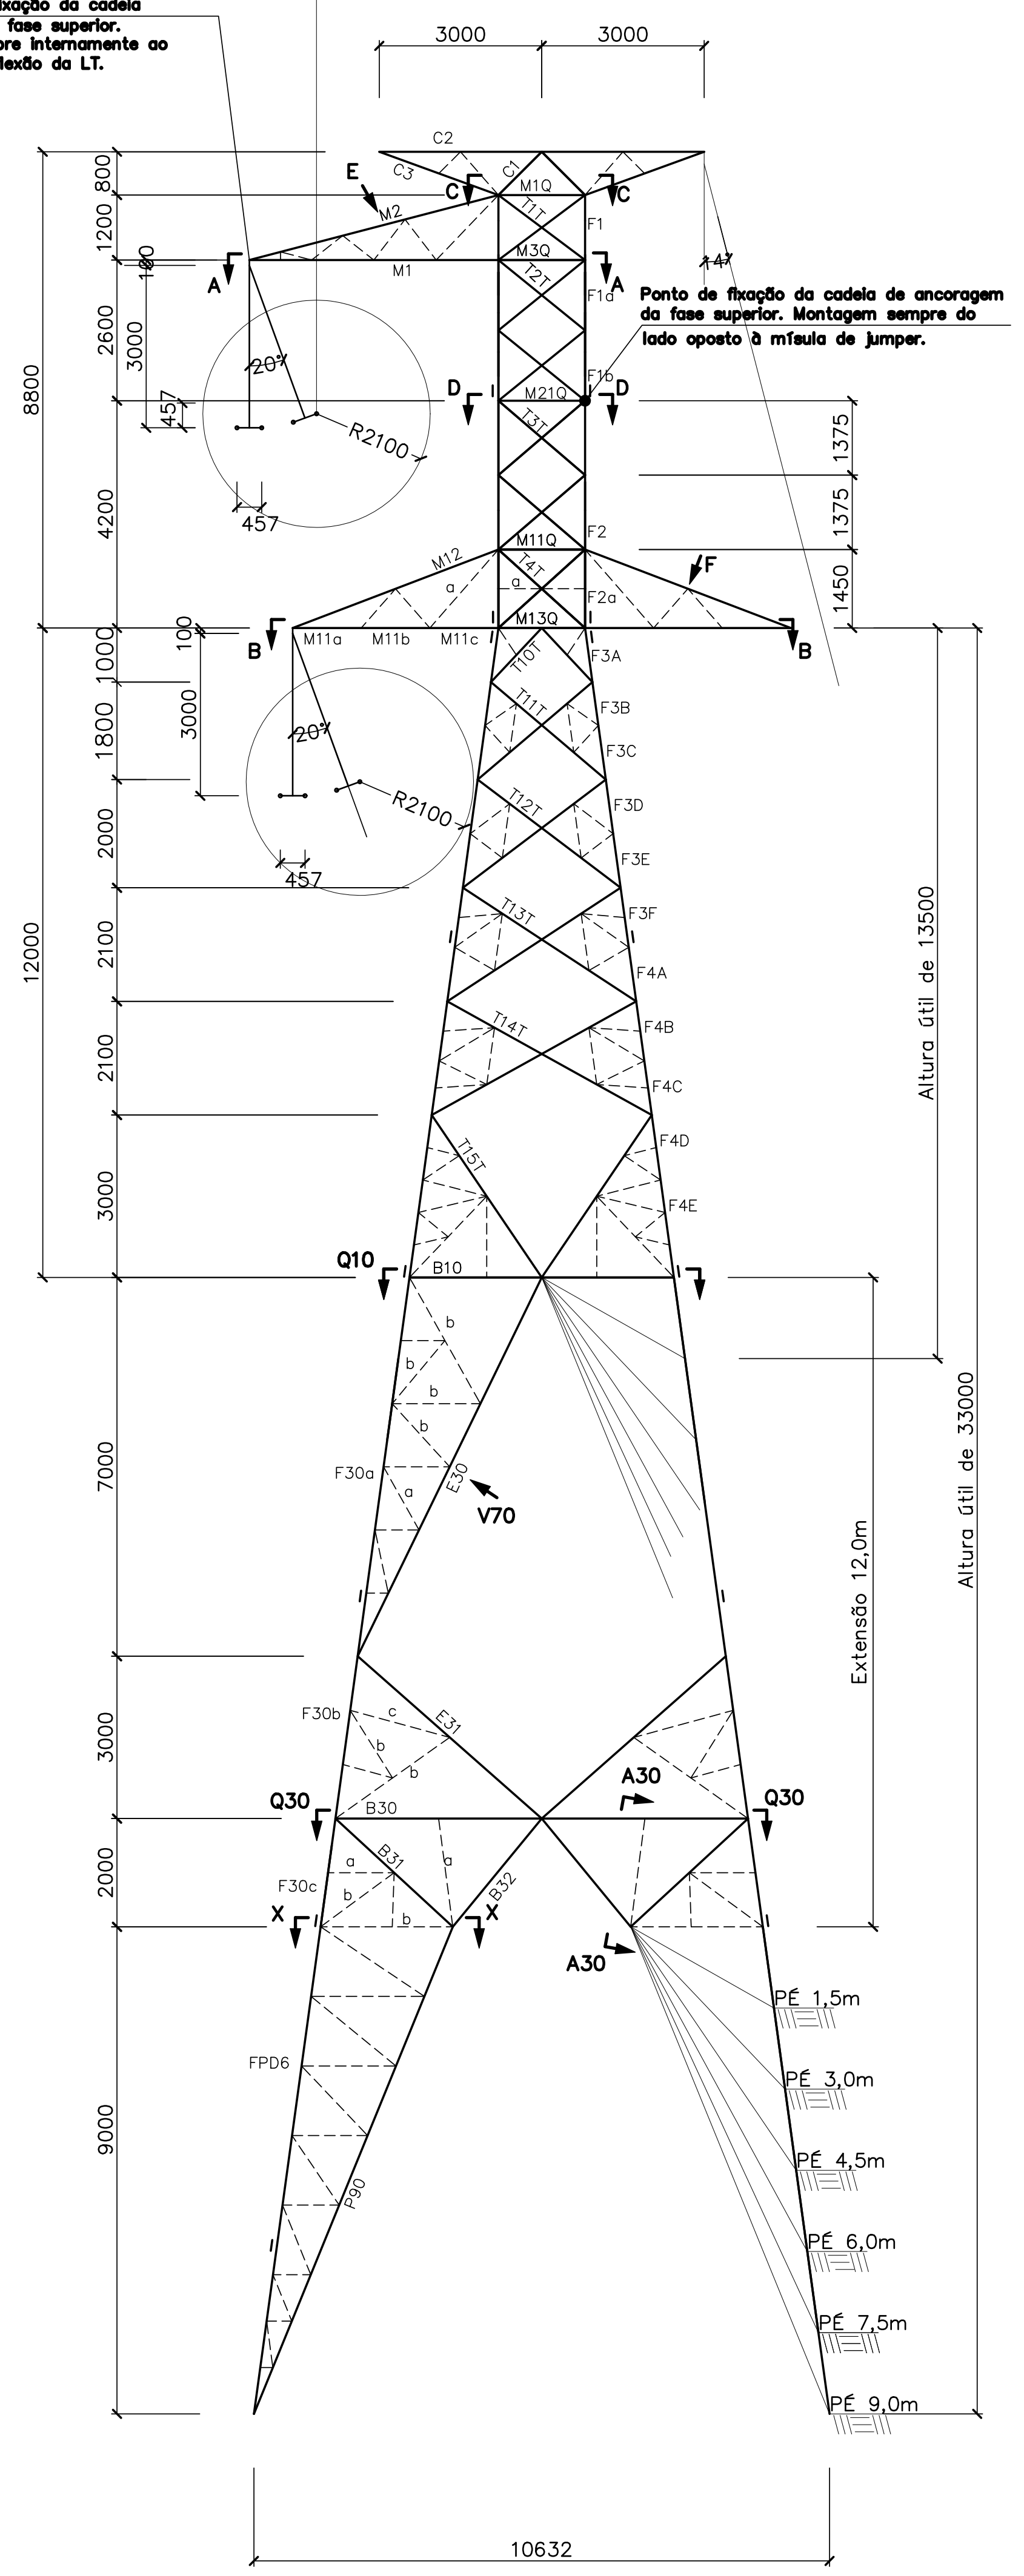

FACE TRANSVERSAL

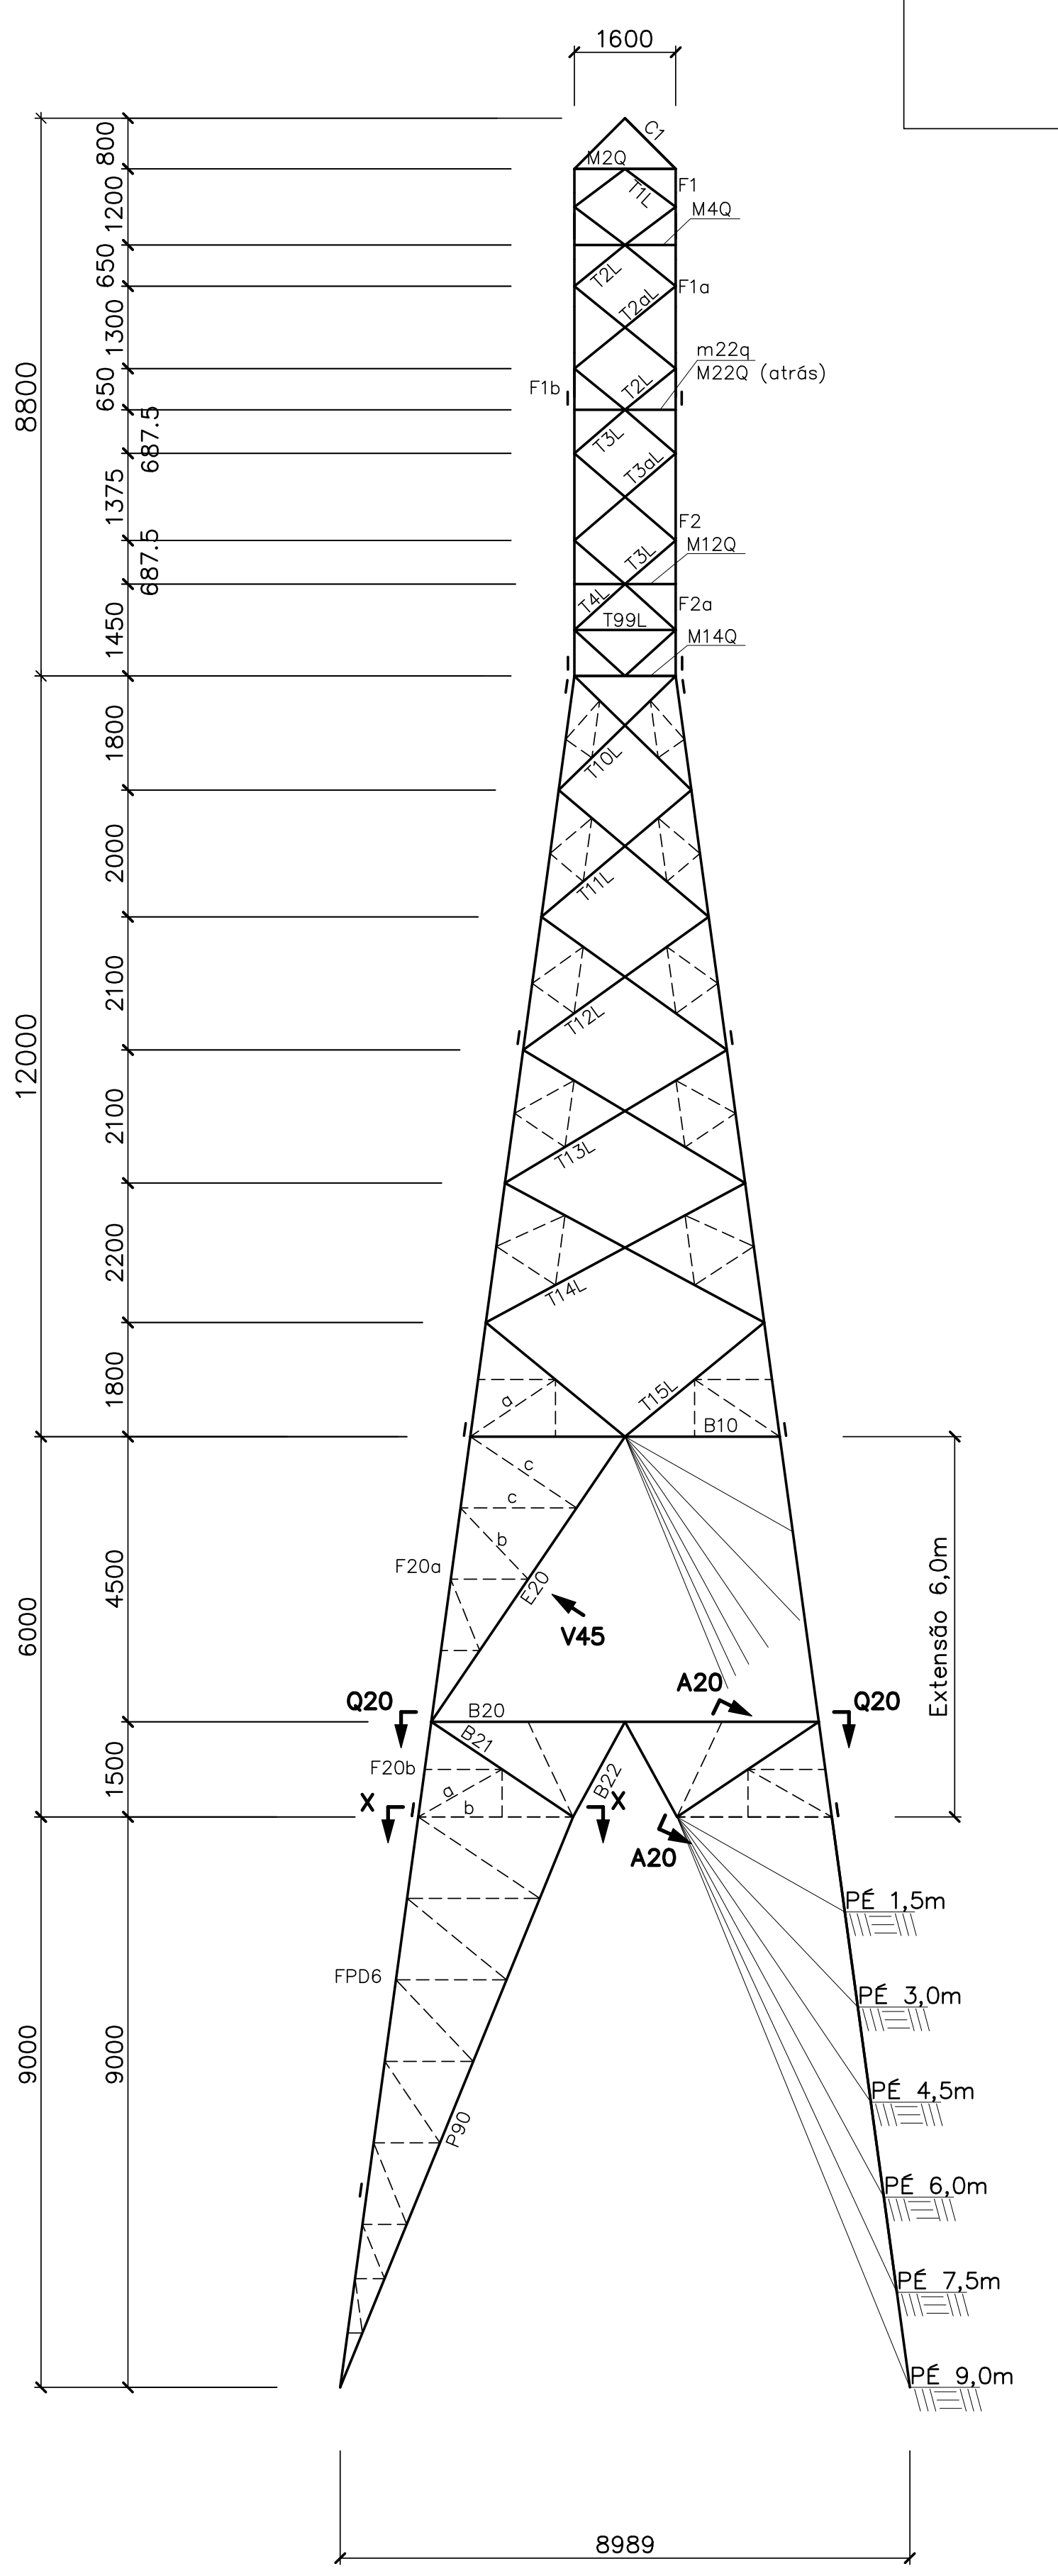

FACE LONGITUDINAL

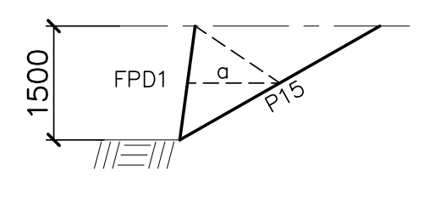

PÉ 1,5m

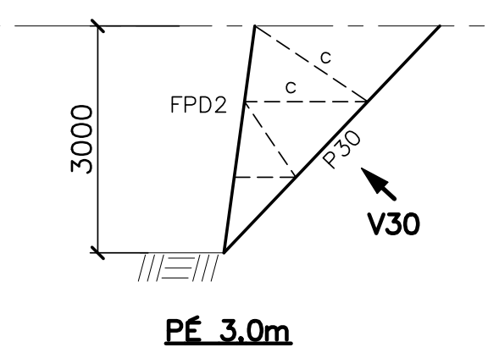

PÉ 3,0m

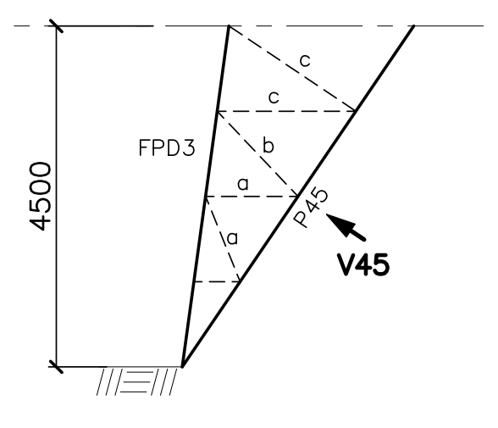

PÉ 4,5m

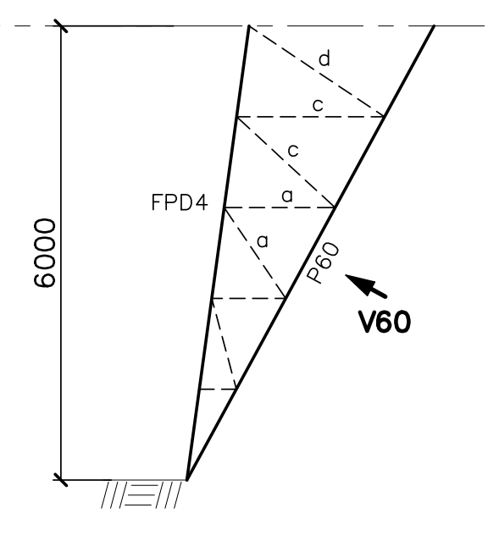

PÉ 6,0m

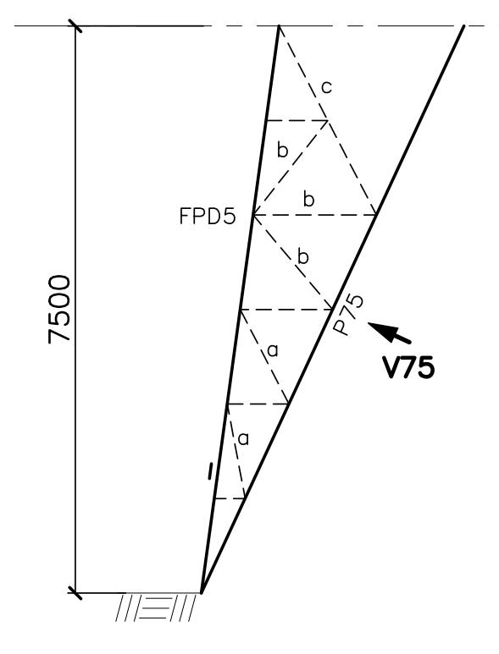

PÉ 7,5m

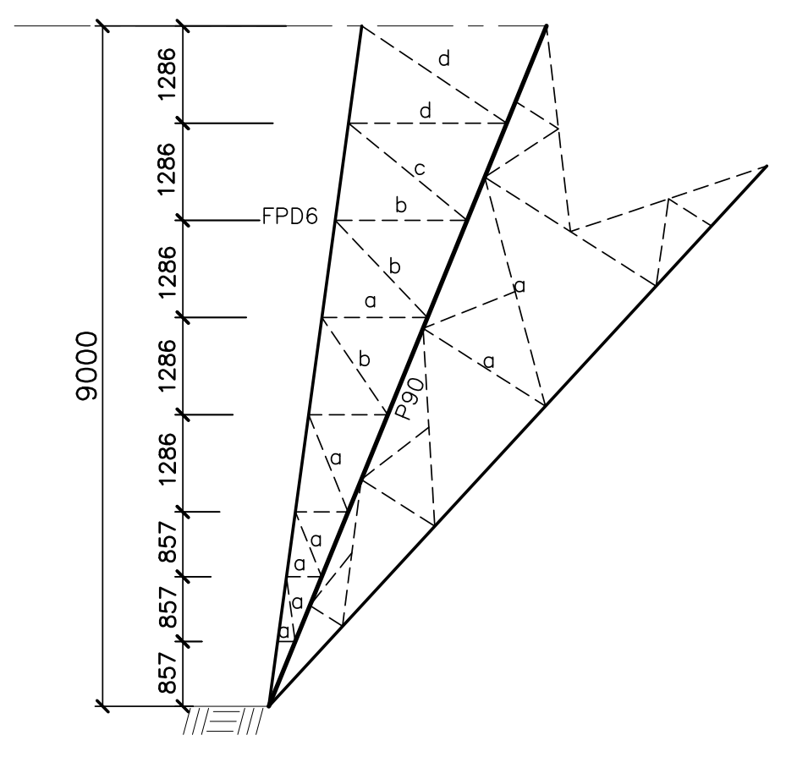

PÉ 9,0m

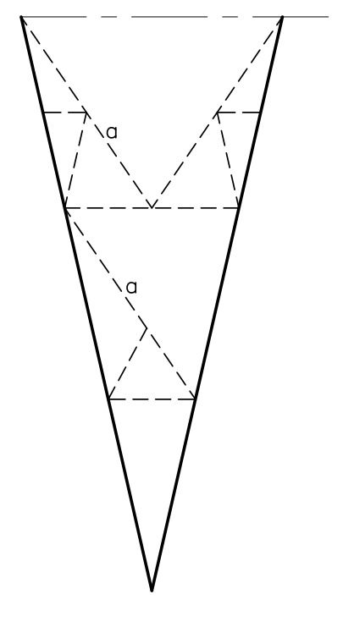

VISTA V70

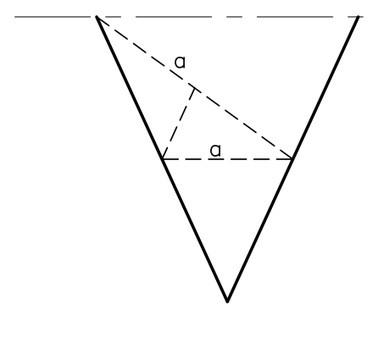

VISTA V30

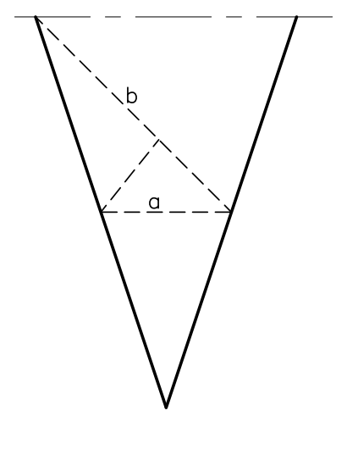

VISTA V45

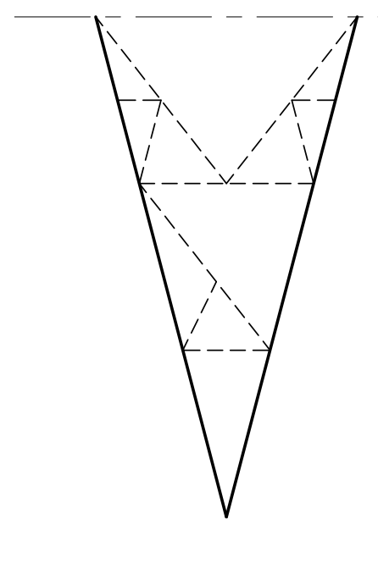

VISTA V60

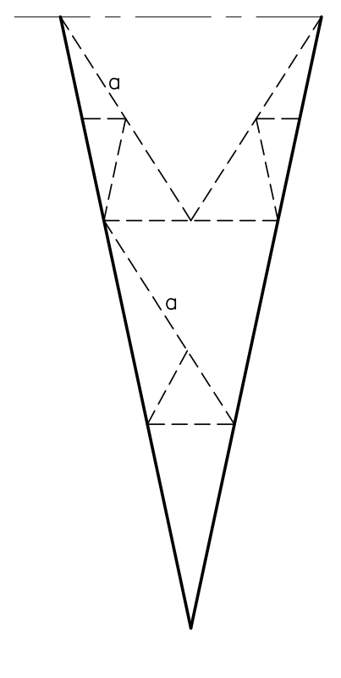

VISTA V75

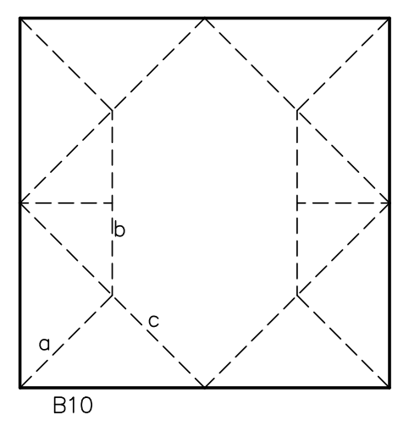

CORTE Q10-Q10

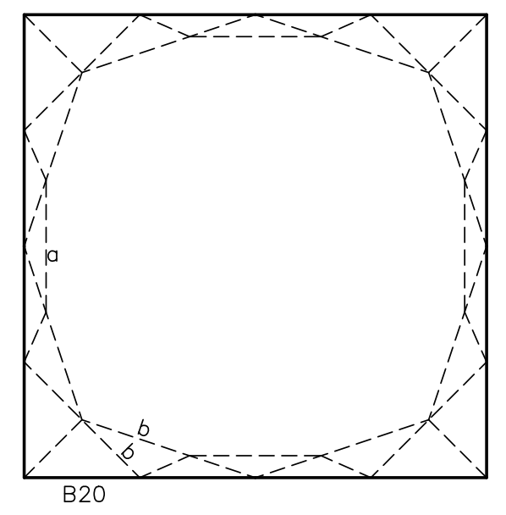

CORTE Q20-Q20

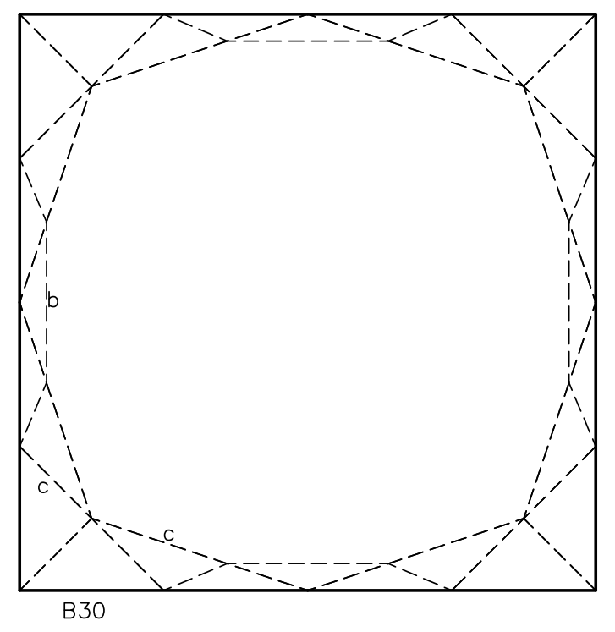

CORTE Q30-Q30

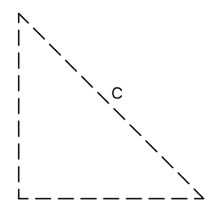

CORTE X-X

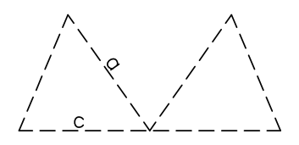

CORTE A20-A20

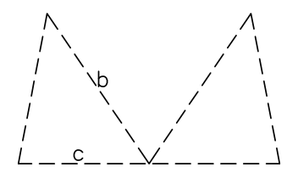

CORTE A30-A30

PADRÃO DE IMPRESSÃO		
DETC.ctb		
COR CAD	ESPESSURA (mm)	COR IMPRESSÃO
1	0,1	7
2	0,2	7
3	0,3	7
4	0,4	7
5	0,5	7
6	0,6	7
7	0,15	7
8	0,1	7
9	0,05	7
11	0,05	7
41	0,05	7

AS DEMAIS CORES DEVEM SER IMPRESSAS EM SUAS RESPECTIVAS CORES COM ESPESSURA DE 0.20 mm.

1. Todas as cotas estão em milímetro.
2. Barras descarregadas:
   Não indicadas: L40x40x3,0H – 1ø12.0
   a) L45x45x3,0H – 1ø12.0
   b) L50x50x3,0H – 1ø12.0
   c) L50x50x4,0H – 1ø12.0
   d) L60x60x4,0H – 1ø12.0
3. Para memória de cálculo ver doc. BNAA_ADR2451-M3001.

NOTAS

N°_DO_DOCUMENTO	TÍTULO DO DOCUMENTO DE REFERÊNCIA
NÚMERO	TÍTULO

DOCUMENTOS DE REFERÊNCIA

REV.	DESCRIÇÃO	DATA	ELABORAÇÃO	VERIFICAÇÃO
00	APROVADO	24/07/2026	LETÍCIA PENIDO	RANIA PEIXOTO
00A	EMISSÃO INICIAL	19/03/2026	CRISTINA CASSIMIRO	RANIA PEIXOTO

N° CR GONTIJO
BNAA_ADR2451-D3001

PROPRIEDADE
Eletrobras
SPE Nova Era Integração Transmissora S.A.

AUTORIA
CONSAG CONSÓRCIO CONSTRUTOR SÃO FRANCISCO
CR GONTIJO ENGENHARIA DE PROJETOS

APROVAÇÃO
HENRIQUE GONTIJO
RESPONSÁVEL TÉCNICO
CREA 108382/MG

RESPONSÁVEL TÉCNICO

LOTE 05 – ANEEL 01/2024

DESCRIÇÃO DESENHO
TORRE DE ANCORAGEM MEIO DE LINHA LEVE TIPO BNAA
SILHUETA

DESCRIÇÃO PROJETO
NOVA ERA INTEGRAÇÃO
LOTE 5 – LT 230 kV
BOM NOME – BOM NOME II C1 E C2

CÓDIGO PROJETO	FORMATO	N° DESENHO	
LTNEI	A0	LTRH1.06-230-PE-EM.DDM-0003	
CLASSIFICAÇÃO	ESCALA	FOLHA	REVISÃO
EXECUTIVO.BÁSICO.PADRÃO	1/100	1	00