
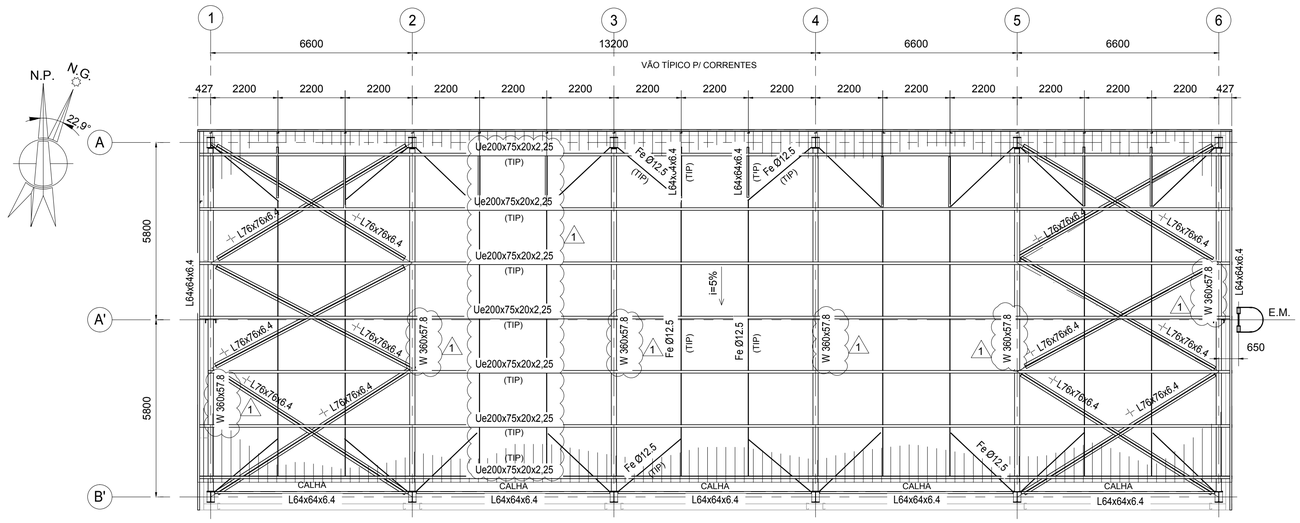



PLANTA DA COBERTURA - EIXOS 1 a 6 / A a B'

ESCALA: 1 : 100

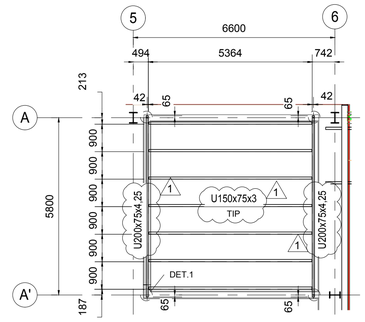


PLANTA NA EL. 104252 - SUPORTE PARA FORRO

ESCALA: 1 : 100

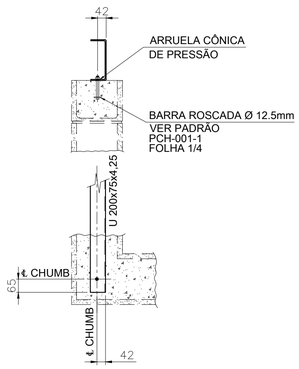


DETALHE 1

ESCALA: 1 : 15

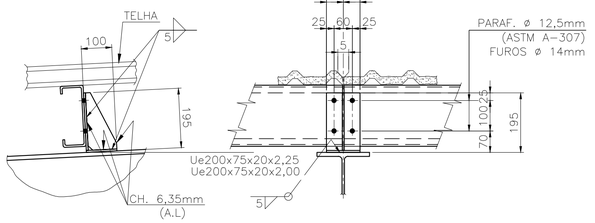


DETALHE TÍPICO DE FIXAÇÃO DAS TERÇAS

ESCALA: 1 : 10

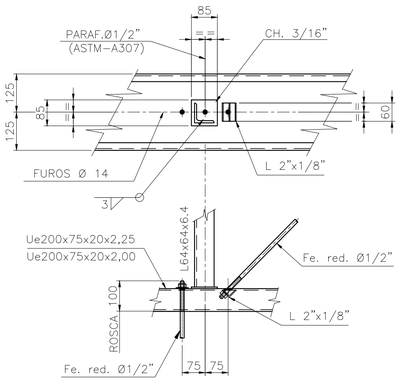


DET. TÍP. DE FIXAÇÃO DAS CORR. RÍGIDA DA COBERTURA

ESCALA: 1 : 10

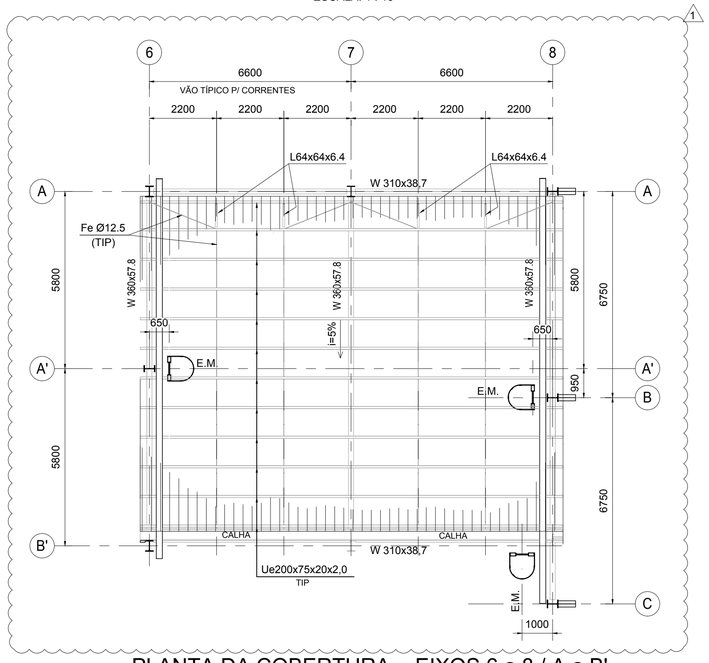

PLANTA DA COBERTURA - EIXOS 6 a 8 / A a B'

ESCALA: 1 : 100

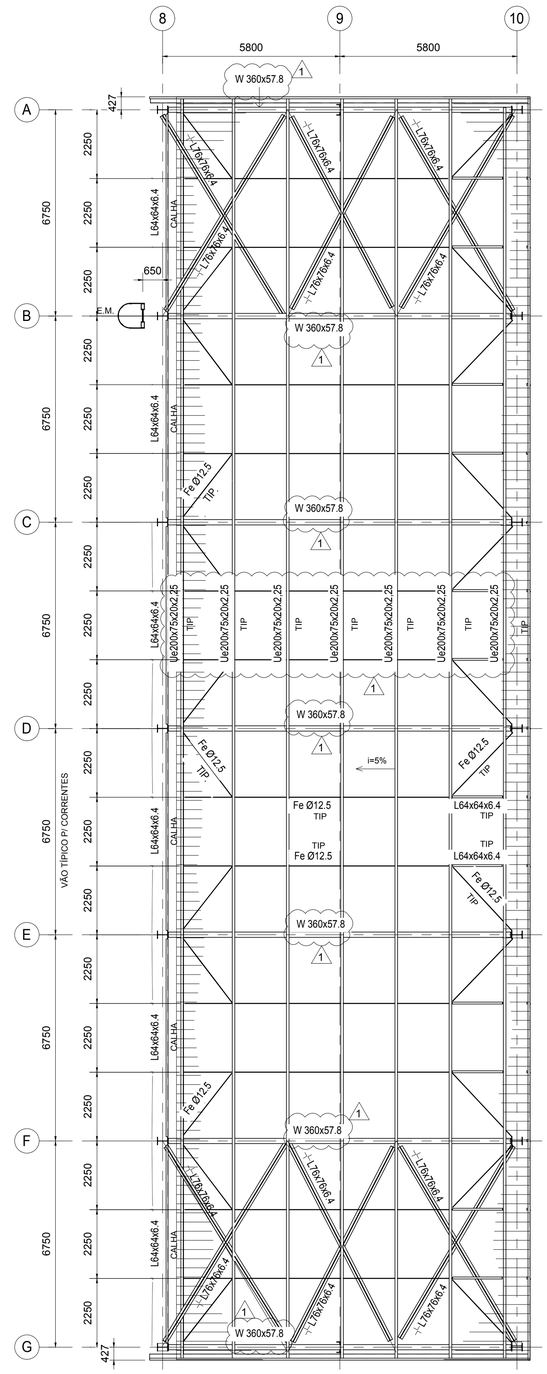

PLANTA DA COBERTURA - EIXOS 8 a 10 / A a G

ESCALA: 1 : 100

NOTAS

1- TODAS AS DIMENSÕES ESTÃO EM MILÍMETRO E ELEVAÇÕES EM METRO, SALVO INDICAÇÃO CONTRÁRIA.

2- PARA NOTAS GERAIS VER DESENHO: NOVO-SRCA-PC-0805-01.

REV.	DESCRIÇÃO	DATA	DES.	VERIF.	APROV.
1	REV. ONDE INDICADO/APROVADO P/ CONSTRUÇÃO	10/08/18	O.J.S.	M.P.R.	E.R.P.
0	EMISSÃO INICIAL/APROV. PARA CONSTRUÇÃO - AFC	28/04/18	G.F.A.	M.P.R.	E.R.P.

REVISÕES

CONTRATANTE:

ENGENHARIA SUBCONTRATADA:

CLIENTE:
UTE GNA I
Gás Natural Açu S.A.

© SENER SETEPLA TECNOMETAL ENGENHARIA E SISTEMAS S.A.
AS INFORMAÇÕES CONTIDAS NESTE DOCUMENTO SÃO CONFIDENCIAIS E RESTRITAS, E DEVEM SER UTILIZADAS SOMENTE PARA FINS ESTABELECIDOS NO DOCUMENTO. NÃO É PERMITIDO QUE TAIS INFORMAÇÕES SEJAM REPRODUZIDAS, TRANSMITIDAS OU DE QUALQUER FORMA COMUNICADAS A QUALQUER PARTE DO DOCUMENTO NÃO É PERMITIDO SEM O CONSENTIMENTO PRÉVIO POR ESCRITO DA SENER SETEPLA TECNOMETAL ENGENHARIA E SISTEMAS S.A.
A FALTA DE RETORNO SOBRE TAL CONSENTIMENTO NÃO DEVE, EM HIPÓTESE ALGUMA, SER INTERPRETADA COMO AUTORIZAÇÃO PARA USO DA INFORMAÇÃO.

No ARQUIVO CAD :	NOVO-SRCA-PC-0805 -02 Rev 1
ESCALA :	INDICADA
REFERÊNCIA :	P0Q27003
PROJETO:	UTE GNA I PLANTA DE CICLO COMBINADO PORTO DO AÇU - RIO DE JANEIRO
No DESENHO SUBCONTRATADA	NOVO-SRCA-PC-0805
No DESENHO CLIENTE:	
No DESENHO SIEMENS:	BR1045-31910-&CLC030-102195
TAMANHO ORIGINAL	A1
TÍTULO DO DESENHO:	OFICINA / ALMOXARIFADO - ESTR. METÁLICA *WORKSHOP WAREHOUSE BUILDING STRUCTURE* PLANTAS DAS COBERTURAS e SUPORTES PARA FORRO
FL.	02
PRÓX.	03

DIN A1 (841 x 594)