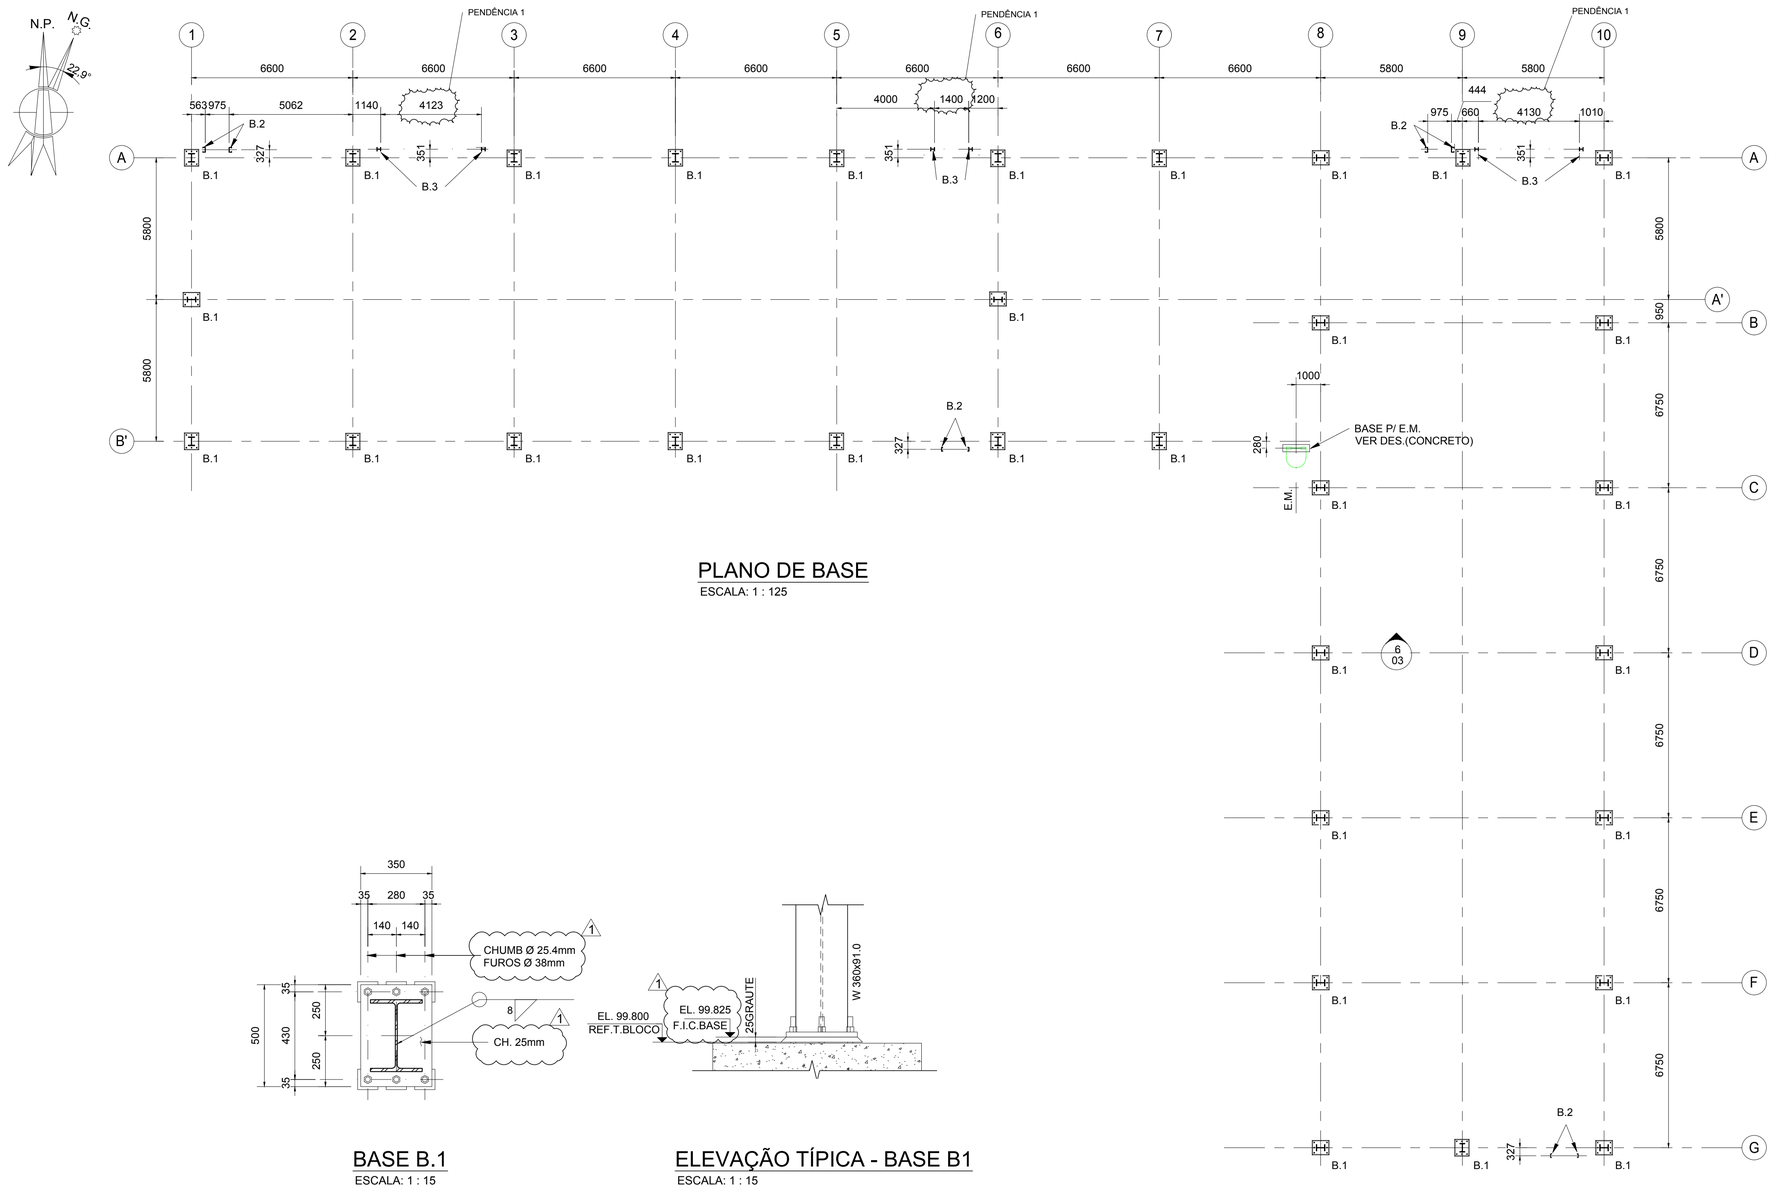


PLANO DE BASE

ESCALA: 1 : 125

BASE B.1

ESCALA: 1 : 15

ELEVAÇÃO TÍPICA - BASE B1

ESCALA: 1 : 15

LISTA DE MATERIAIS (COLUNAS)			
PERFIL	PESO UNIT (kg).	COMPRIM. TOTAL.(m)	PESO TOTAL (kg)
W 360x79.0	79	35,0	2765
W 360x91.0	91	250,7	22814
TOTAL		285,7	25579

LISTA DE MATERIAIS (VIGAS)			
PERFIL	PESO UNIT. kg/m	COMPRIM.TOTAL . (m - m²)	PESO TOTAL (kg)
VS 500x61	61,1	53,0	3239
W 360x79.0	79,0	6,0	474
W 360x57.8	57,8	180,0	10404
W 310x38.7	38,7	173,4	6711
W 200x35.9	35,9	125,0	4488
W 200x26,6	26,6	53,0	1410
W 150x22.5	22,5	41,0	923
Ue200x100x25x2,65	9,0	1151	10359
Ue200x75x20x2,25	6,63	527	3494
Ue200x75x20x2,00	5,92	166	983
U200x75x4,25	11,3	12,00	136
U150x75x3,00	6,83	38	260
L76x76x9,5	10,7	93,2	997
L76x76x6,4	7,29	370,0	2697
L76x76x4,8	5,5	73,0	403
L64x64x6.4	6,1	330,0	2013
L51x51x6.35	4,7	128,0	602
L51x51x9,5	6,99	26,0	182
Fe Ø12.5	1,0	805,3	806
CHAPA 25,4mm	199,2	5,0	996
CHAPA 19mm	149,4	10,2	1524
CHAPA 16mm	124,2	1,6	201
TOTAL			53302

1 OBS. ESTES PESOS NÃO INCLUEM ELEMENTOS DE LIGAÇÕES

PENDÊNCIA

1 - AGUARDANDO MEDIDAS DO FORNECEDOR

2 - MEDIDAS A SER DEFINIDAS PELO FORNECEDOR DA PONTE ROLANTE.

1

NOTAS:

1- TODAS AS DIMENSÕES ESTÃO EM MILÍMETRO E COORDENADAS EM METRO, SALVO INDICAÇÃO CONTRÁRIA.

2- MATERIAIS

-AÇOS LAMINADOS PLANOS ASTM A572 GR 50

-AÇOS LAMINADOS NÃO PLANOS TIPO "W" ASTM A-572 GRAU 50

-AÇOS PARA PERFIS SOLDADOS ASTM-A572 GR 50

1 -AÇOS PARA PERFIS DE CHAPA DOBRADA ASTM A36


-BARRA CIRCULAR AÇO F1554

-PARAFUSOS DE ALTA RESISTÊNCIA ASTM-F3125 GR A-325

-PARAFUSOS COMUNS ASTM-A307


-ELETRODOS E70XX

3- AS CARGAS MÍNIMAS PARA OS DETALHAMENTOS DAS CONEXÕES QUE NÃO FORAM APRESENTADAS NOS DESENHOS SÃO:
NORMAL= 4 kN E CISALHAMENTO= 12.4 kN.

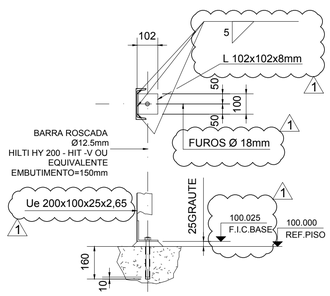


BASE B.2

ESCALA: 1 : 15

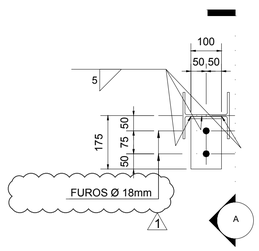

BASE B.3

ESCALA: 1 : 10

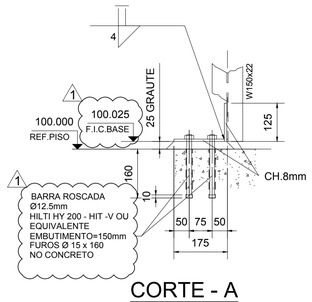

CORTE - A

ESCALA: 1 : 10

REV.	DESCRIÇÃO	DATA	DES.	VERIF.	APROV.
1	REV. ONDE INDICADO/APROVADO P/ CONSTRUÇÃO	10/08/18	O.J.S.	M.P.R.	E.R.P.
0	EMISSÃO INICIAL/APROV. PARA CONSTRUÇÃO - AFC	28/04/18	G.F.A.	M.P.R.	E.R.P.

REVISÕES

CONTRATANTE: SIEMENS / AG ANDRADE GUTIERREZ CONSÓRCIO ACU

ENGENHARIA SUBCONTRATADA: SENER

CLIENTE: **UTE GNA I** Gás Natural Açu S.A.

© SENER SETEPLA TECNOMETAL ENGENHARIA E SISTEMAS S.A.
AS INFORMAÇÕES CONTIDAS NESTE DOCUMENTO SÃO CONFIDENCIAIS E RESTRITAS, E DEVEM SER UTILIZADAS SOMENTE PARA FINS ESTABELECIDOS NO DOCUMENTO. MODIFICAÇÃO, EXPLORAÇÃO, REPRODUÇÃO, COMUNICAÇÃO A QUALQUER TERCEIRO, DIFUSÃO OU DISTRIBUIÇÃO DE TODO OU QUALQUER PARTE DO DOCUMENTO SEM O PRÉVIO BOM CONSENTIMENTO PRÉVIO POR ESCRITO DA SENER SETEPLA TECNOMETAL ENGENHARIA E SISTEMAS S.A. A FALTA DE RETORNO SOBRE TAL CONSENTIMENTO NÃO DEVE, EM HIPÓTESE ALGUMA, SER INTERPRETADA COMO AUTORIZAÇÃO PARA USO DA INFORMAÇÃO.

Nº ARQUIVO CAD:	NOVO-SRCA-PC-0805 -01 Rev 1
ESCALA:	INDICADA
REFERÊNCIA:	P0Q27003
TAMANHO ORIGINAL	A1
PROJETO:	UTE GNA I PLANTA DE CICLO COMBINADO PORTO DO AÇU - RIO DE JANEIRO
Nº DESENHO SUBCONTRATADA	NOVO-SRCA-PC-0805
Nº DESENHO CLIENTE:	
Nº DESENHO SIEMENS:	BR1045-31910-&CLC030-102195
TÍTULO DO DESENHO:	OFICINA / ALMOXARIFADO - ESTR. METÁLICA *WORKSHOP WAREHOUSE BUILDING STRUCTURE* PLANO DE BASES e DETALHE
FL.	01
PRÓX.	02

DIN A1 (841 x 594)