Eletrobras
APROVADO
Por: Wallace Castro em 01/09/2026

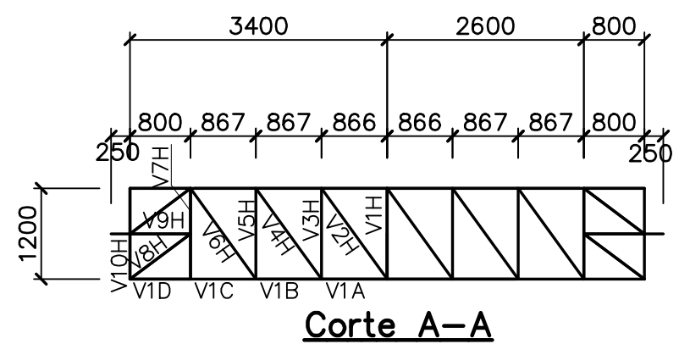

Corte A–A

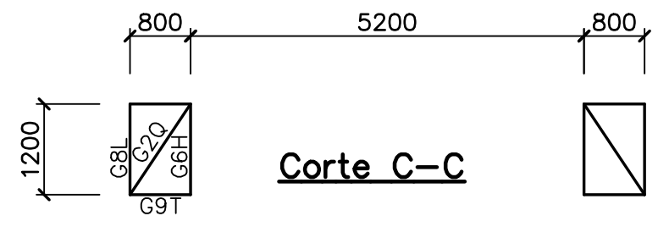

Corte C–C

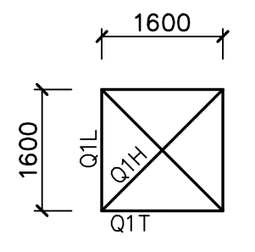

Seção E–E

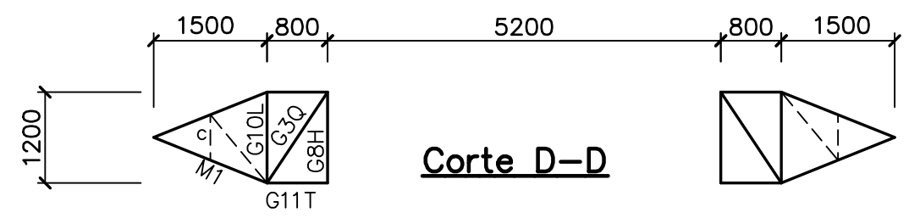

Corte D–D

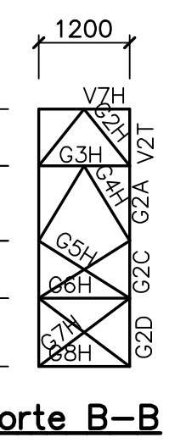

Corte B–B

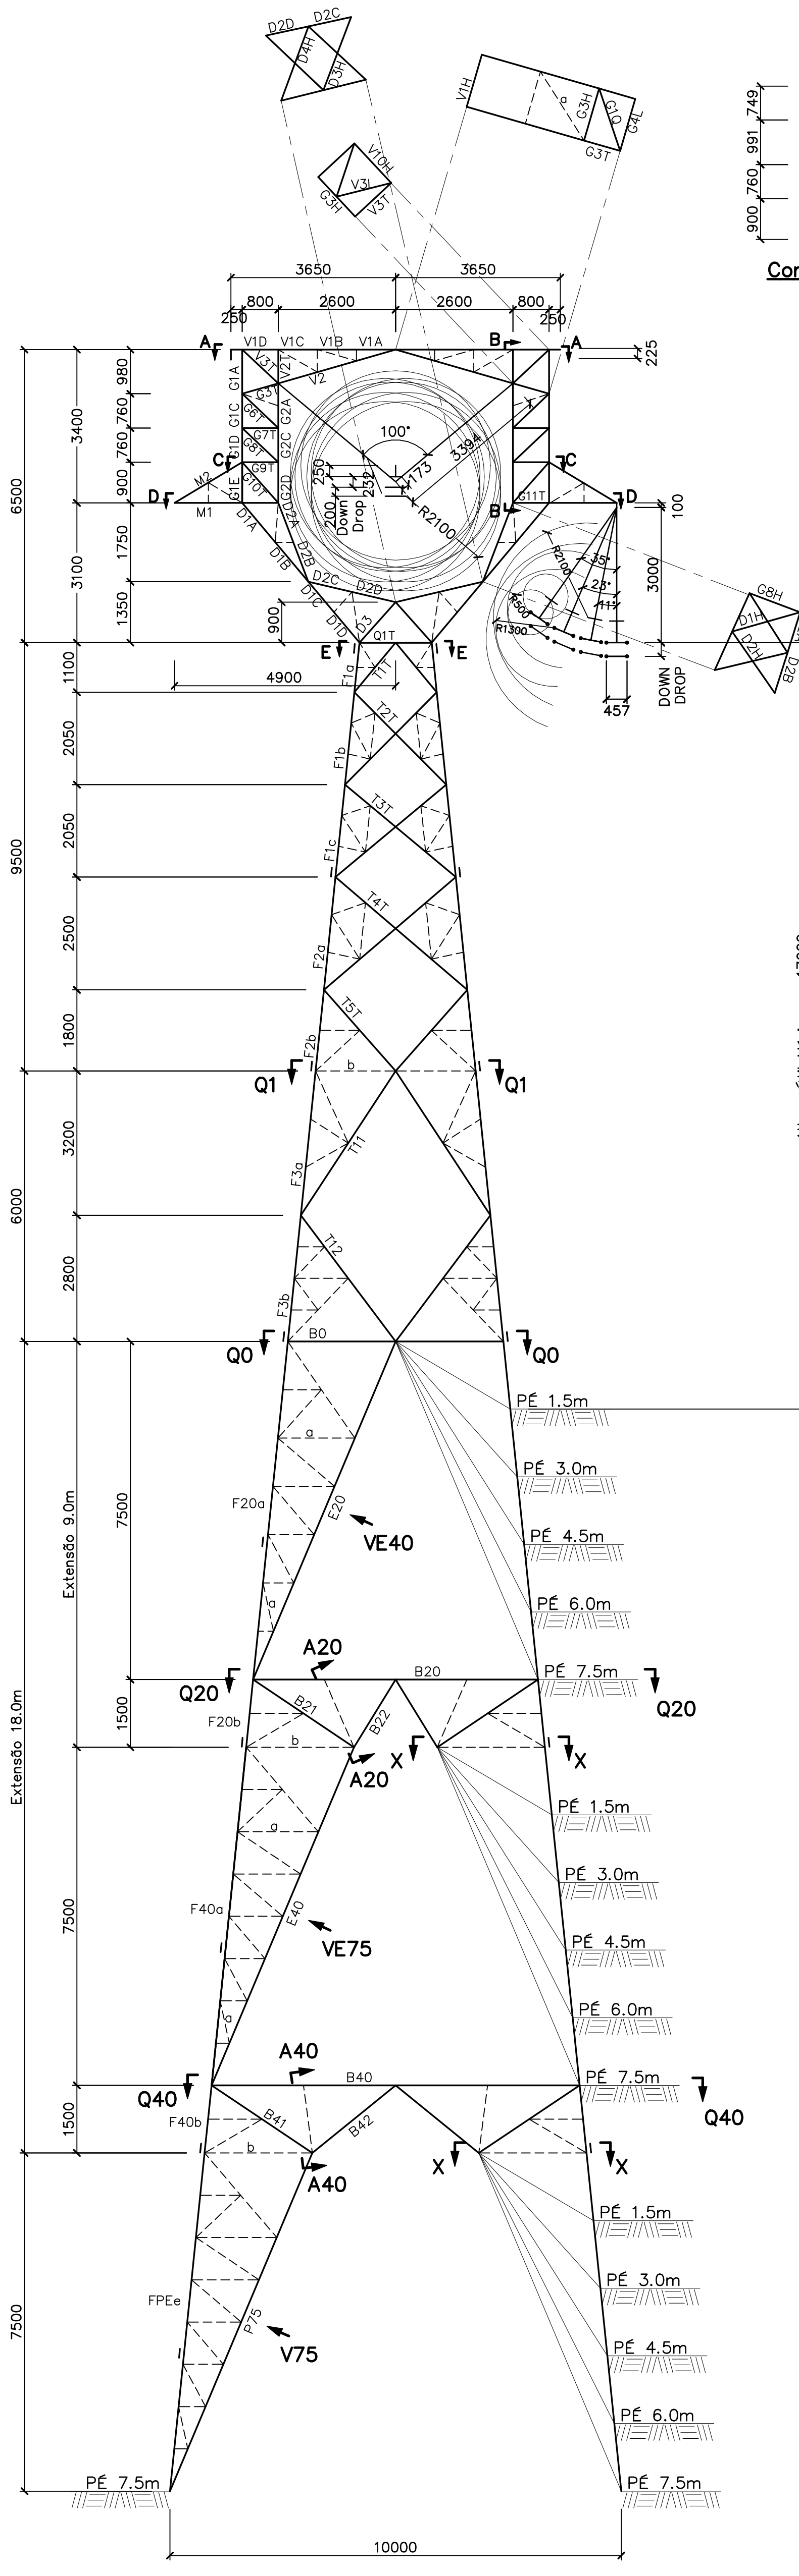

FACE TRANSVERSAL

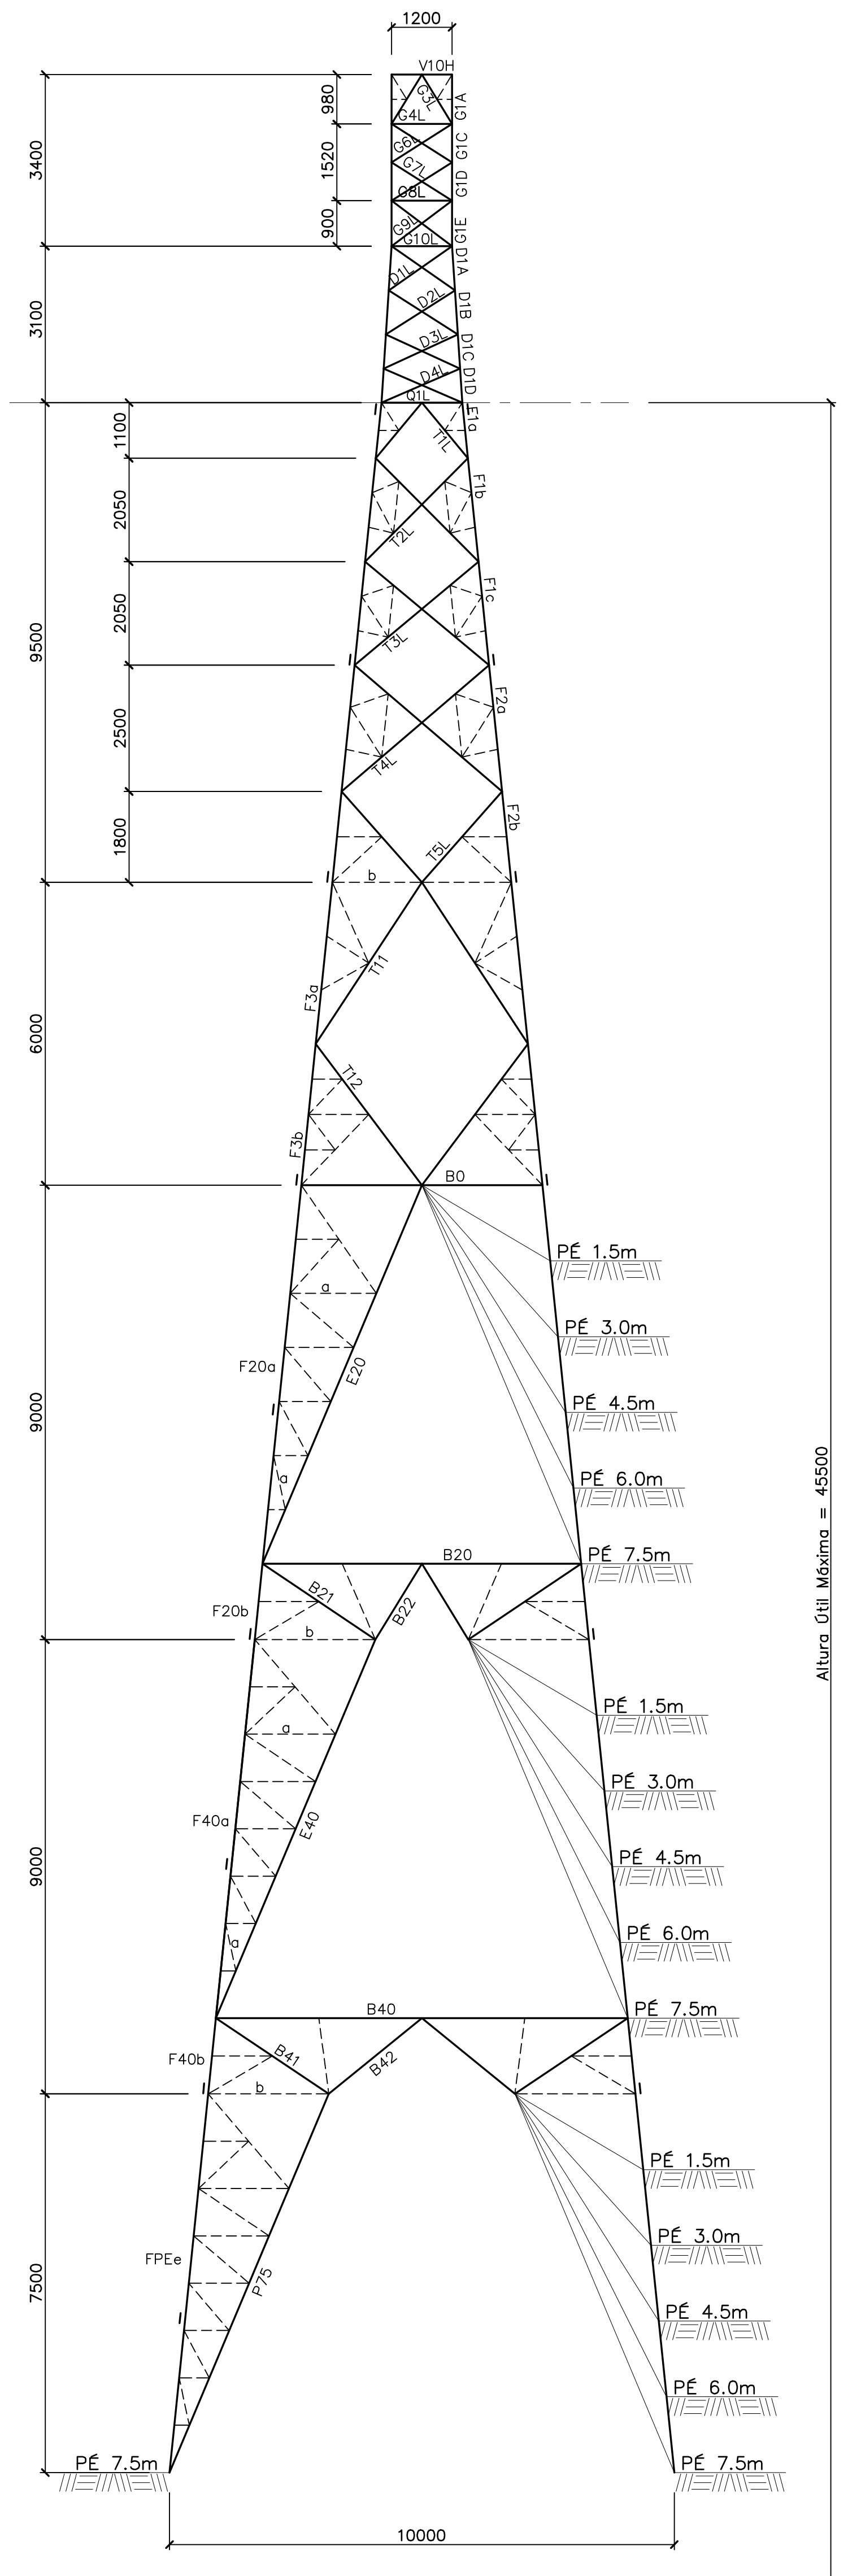

FACE LONGITUDINAL

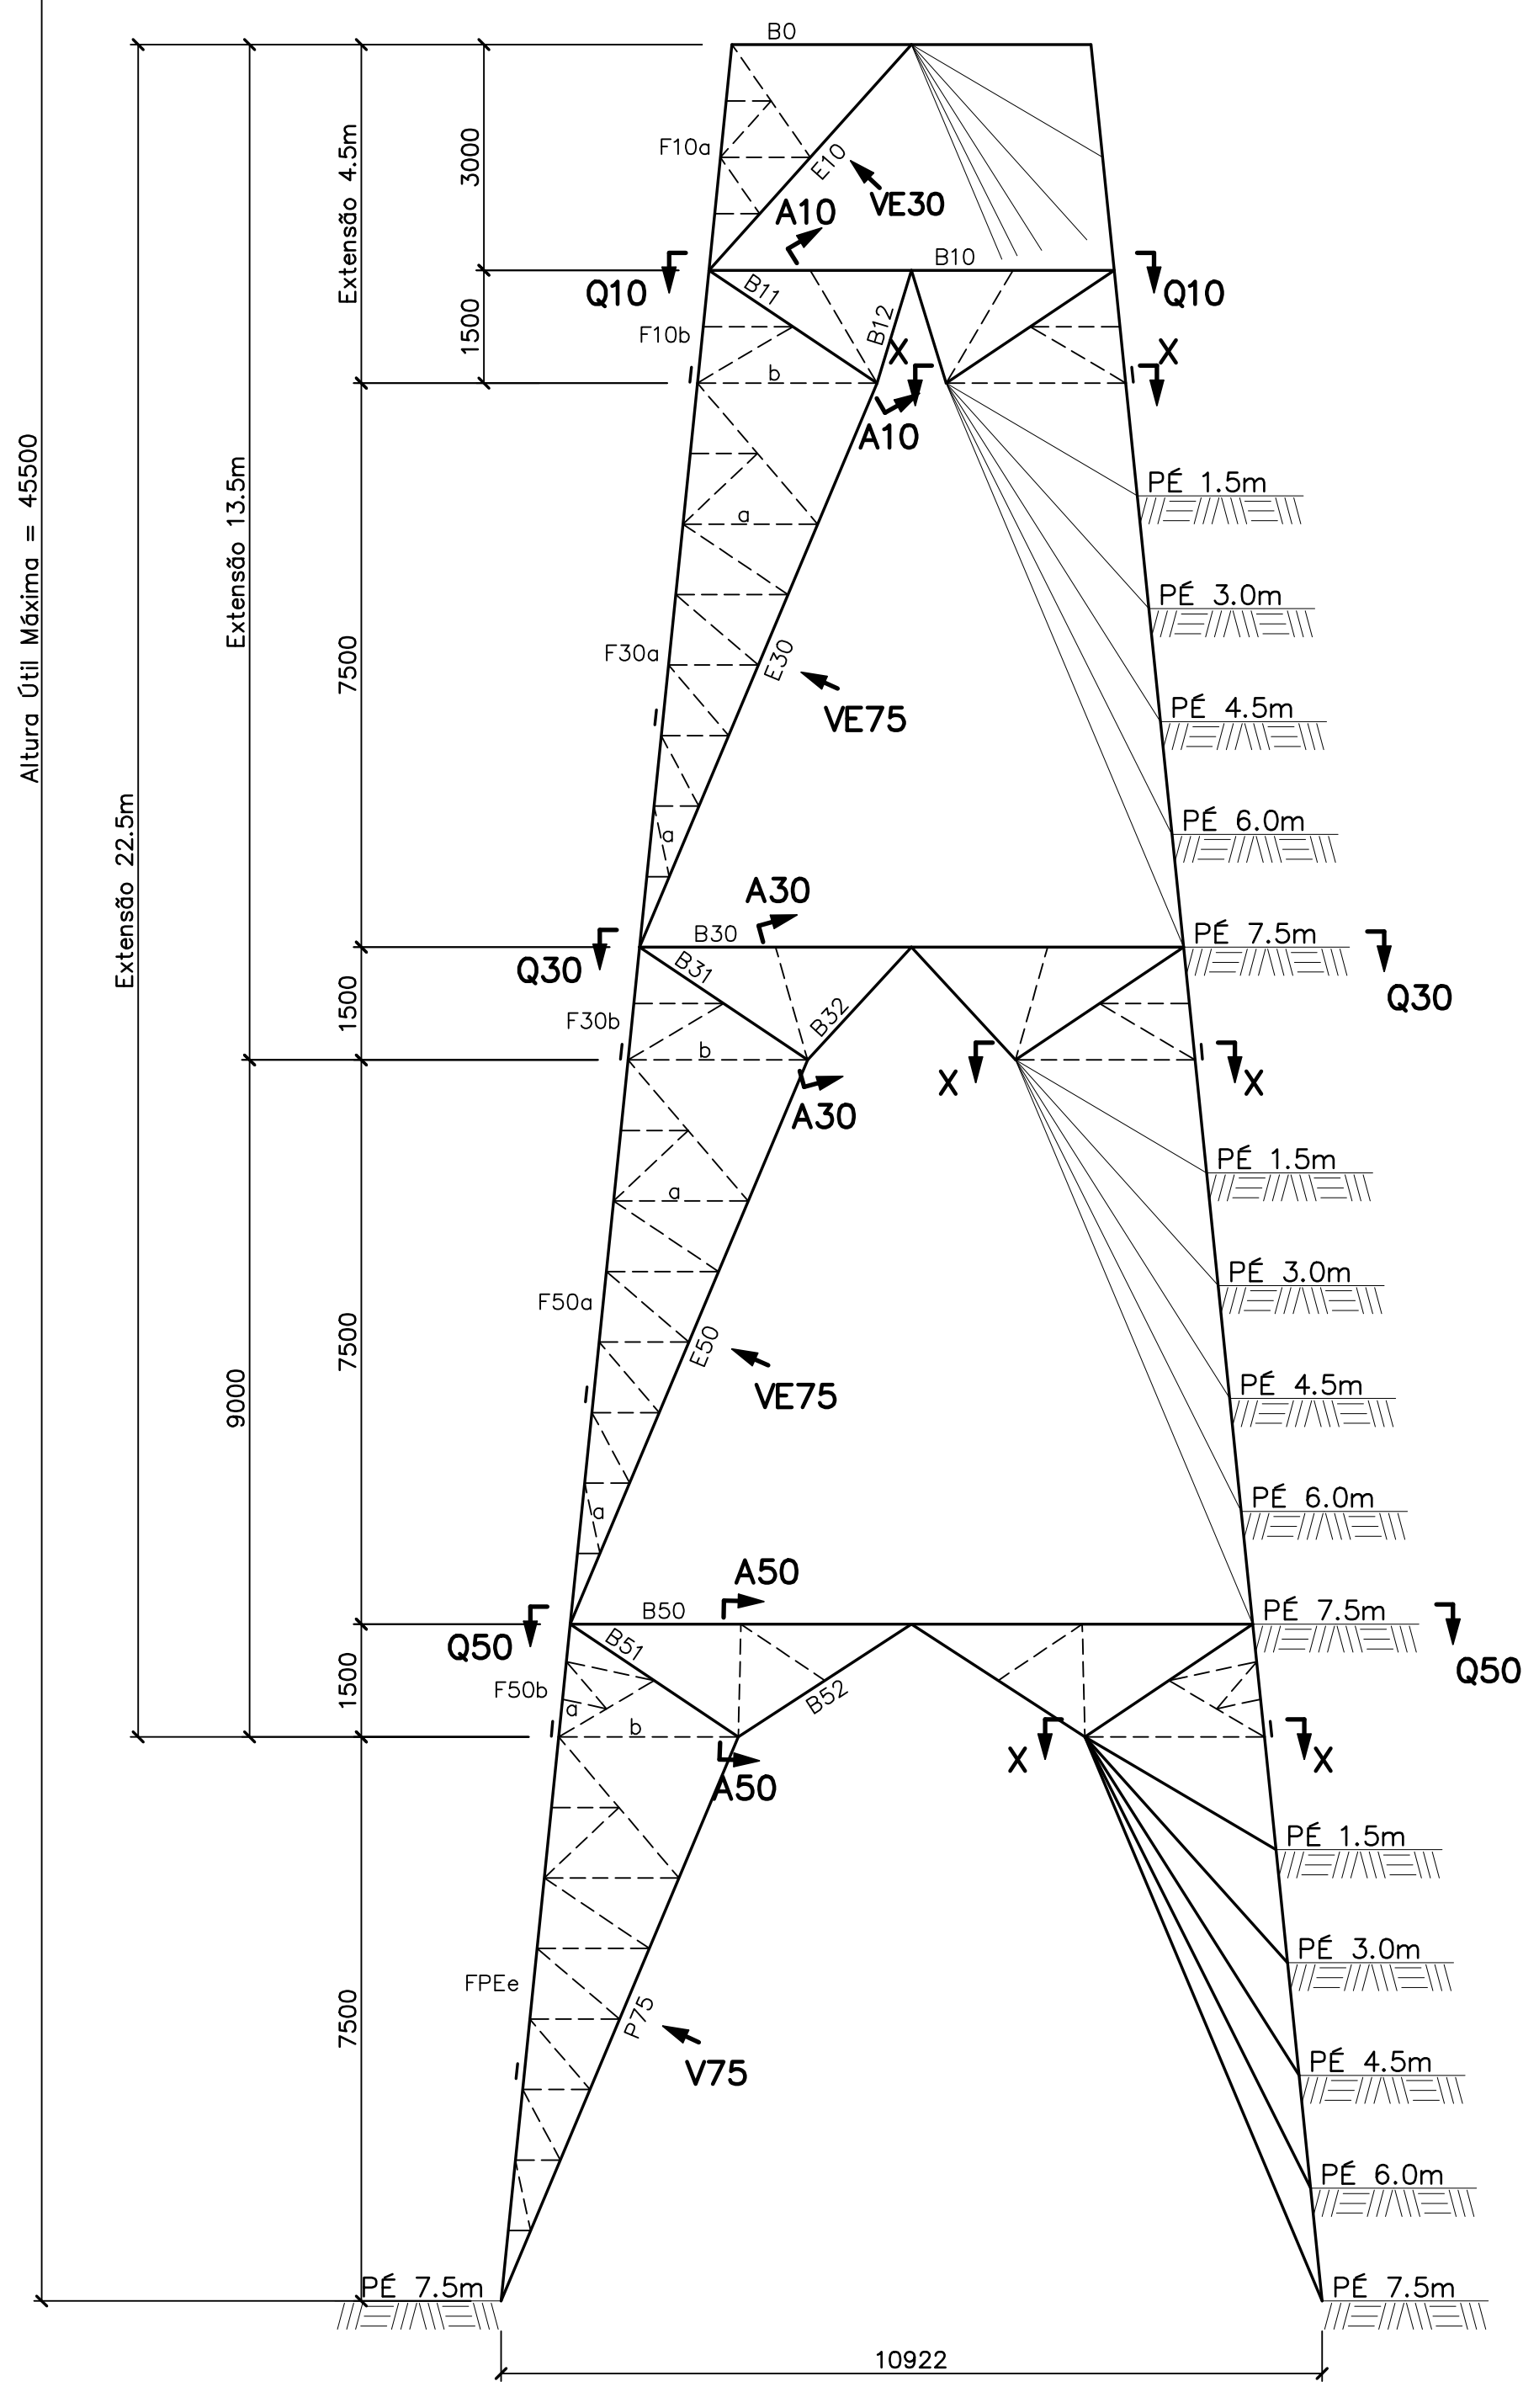

FACE TRANSVERSAL

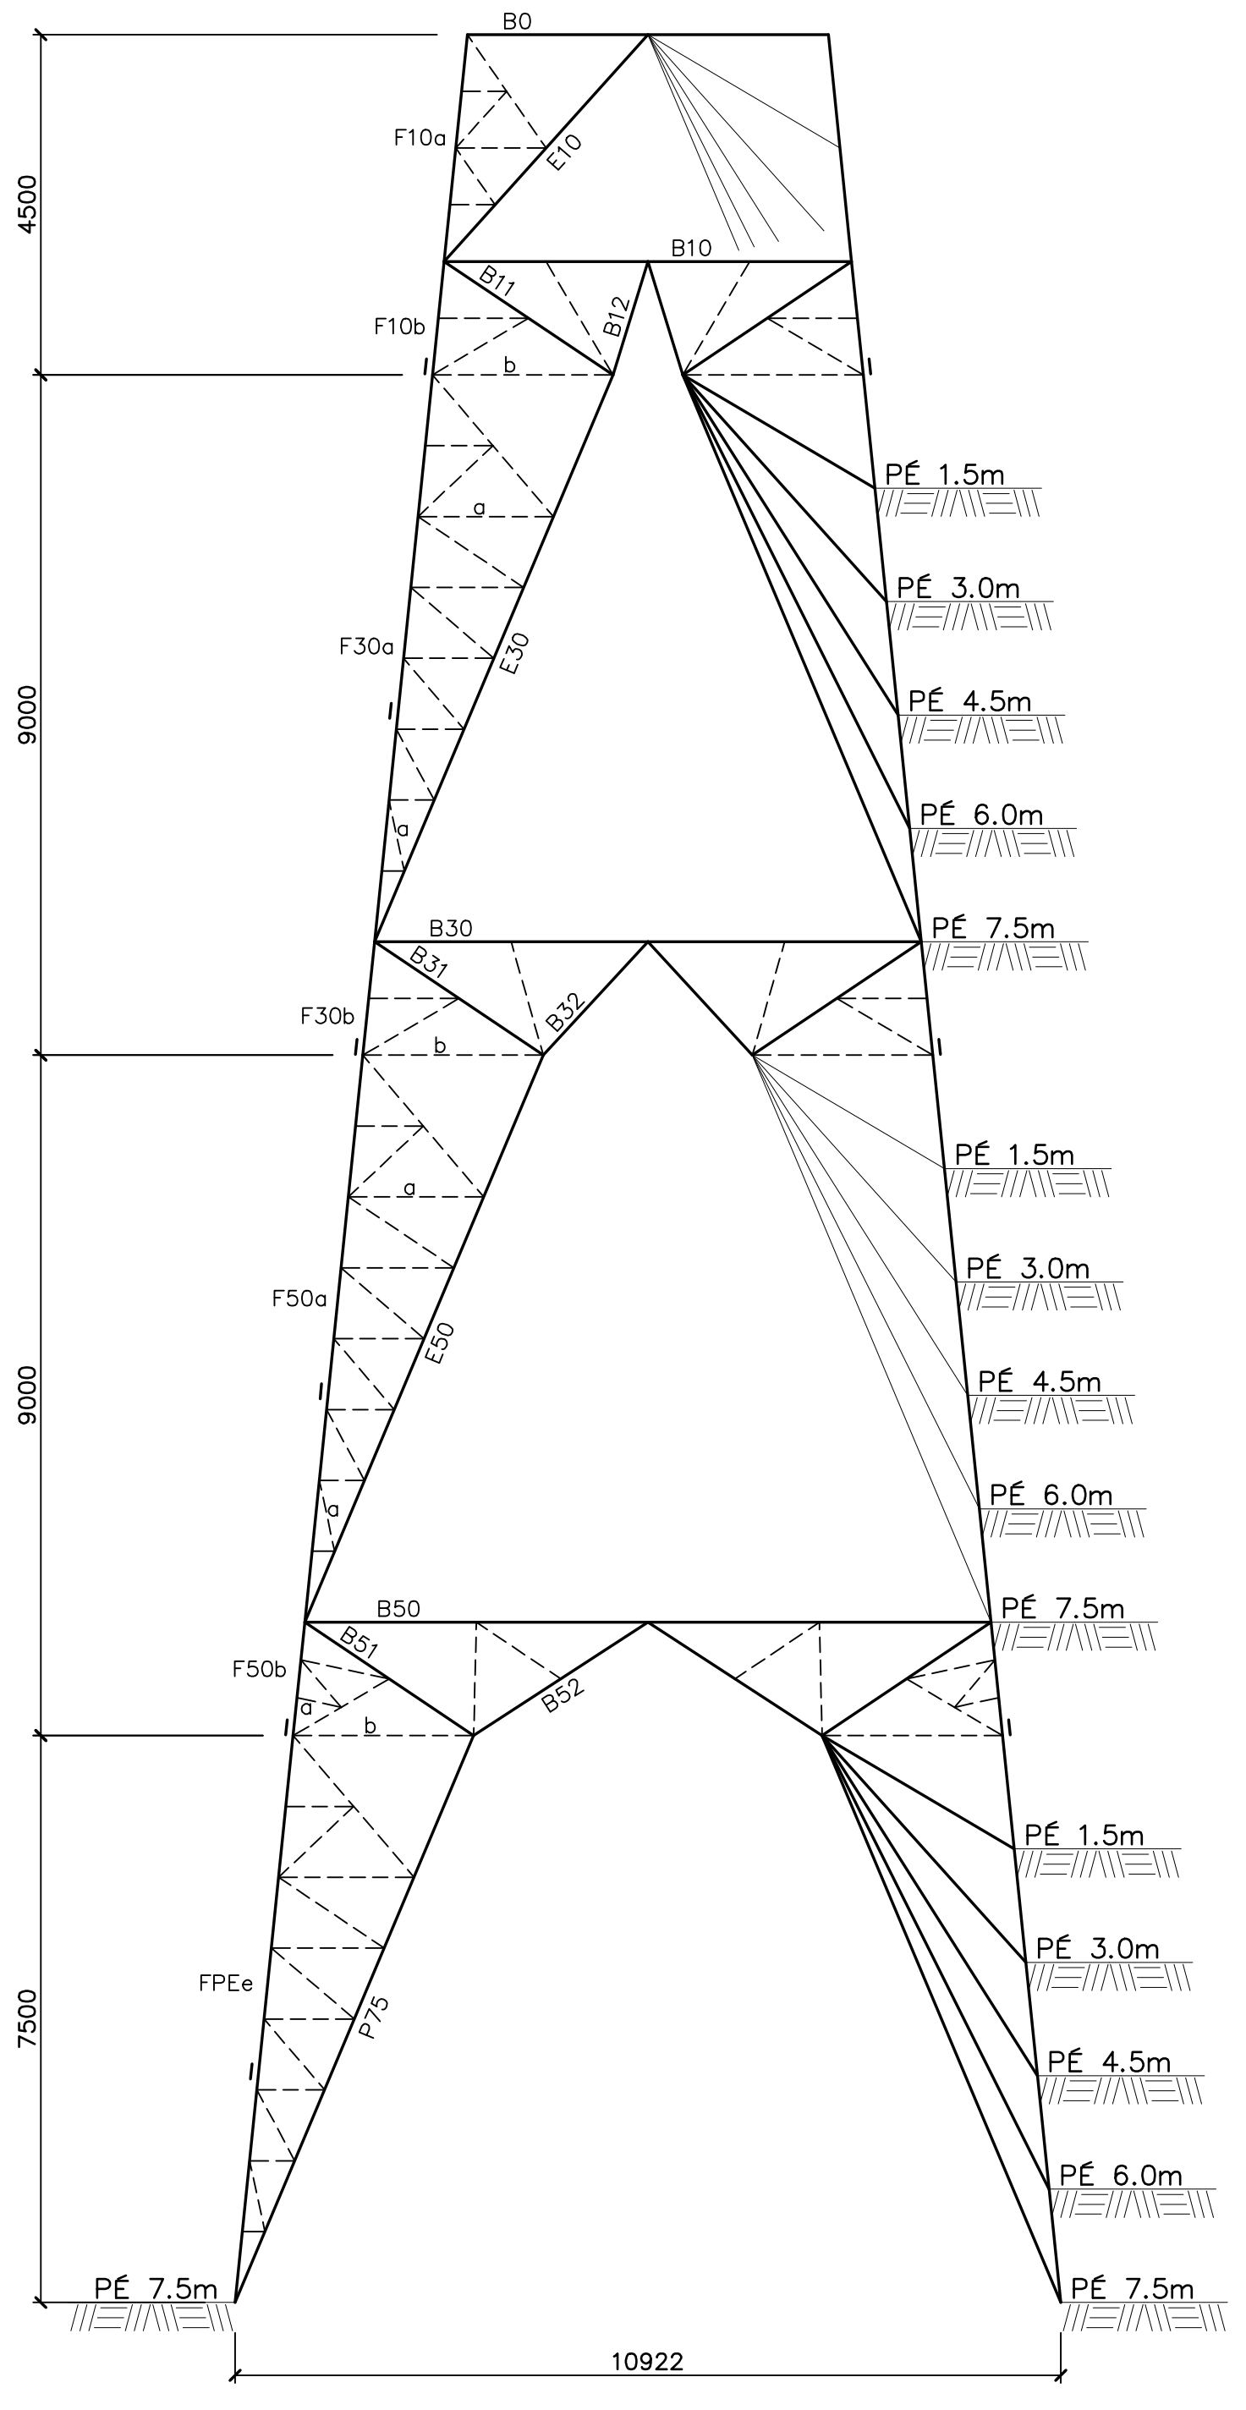

FACE LONGITUDINAL

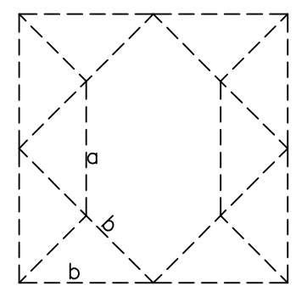

Seção Q1–Q1

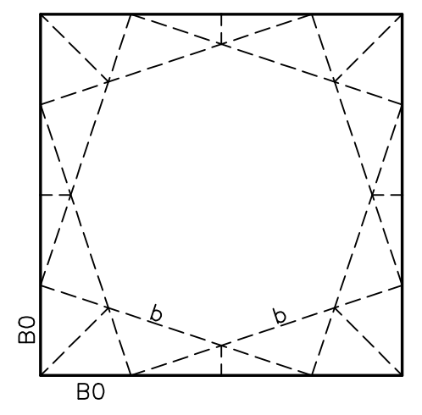

Seção Q0–Q0

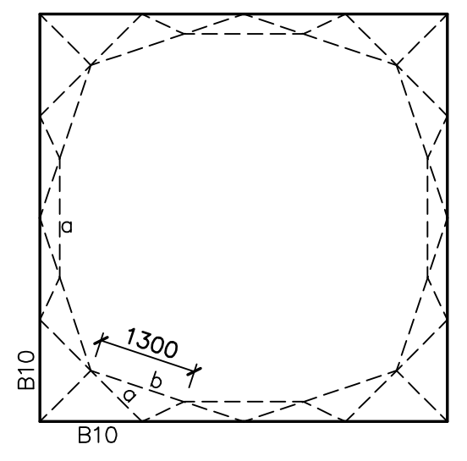

Seção Q10–Q10

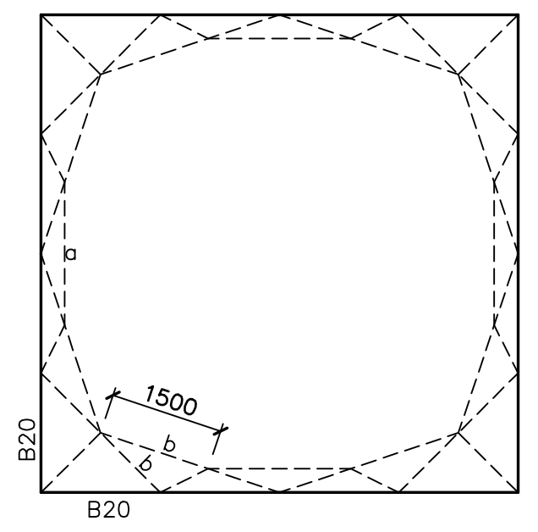

Seção Q20–Q20

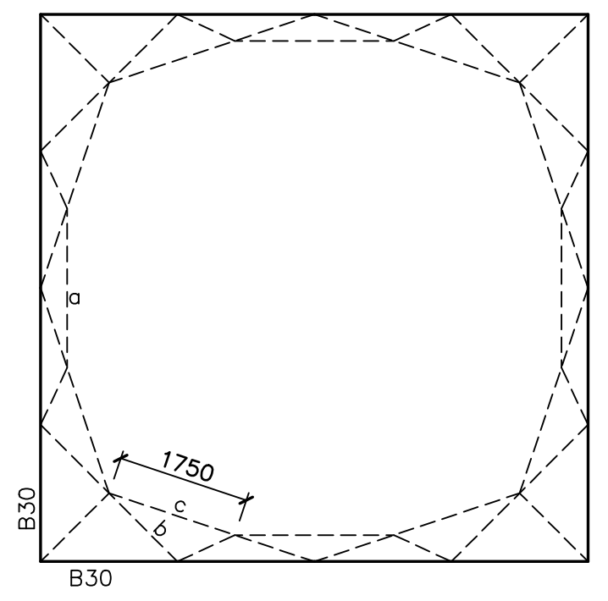

Seção Q30–Q30

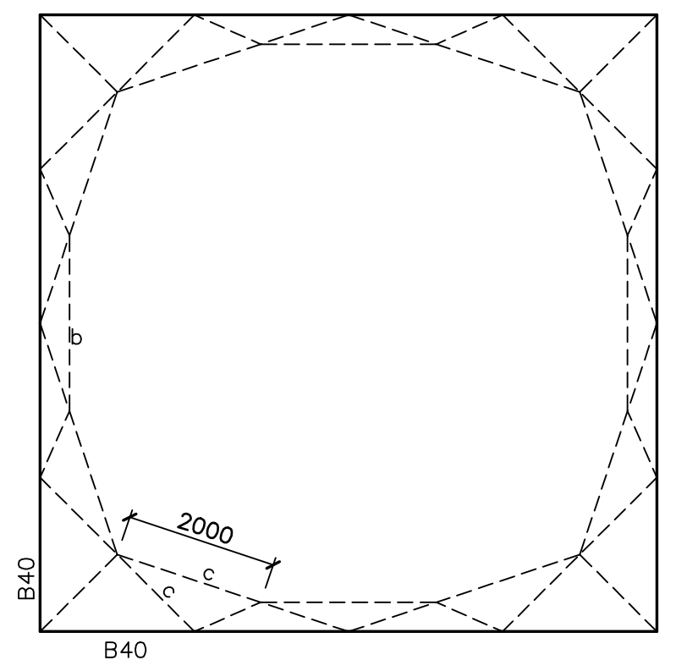

Seção Q40–Q40

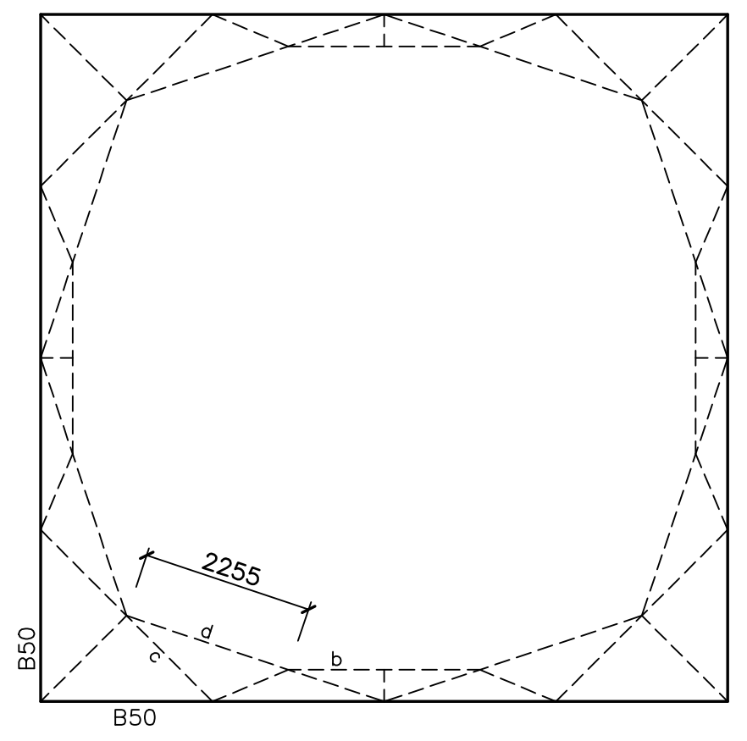

Seção Q50–Q50

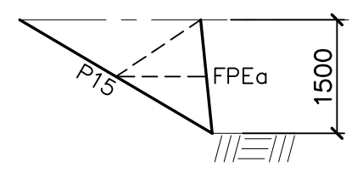

PÉ 1,50m

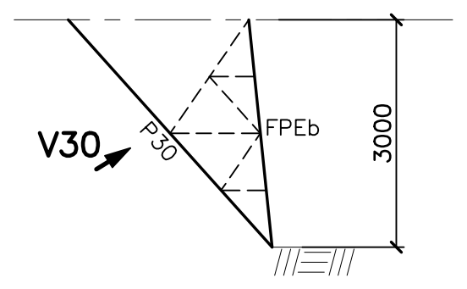

PÉ 3,00m

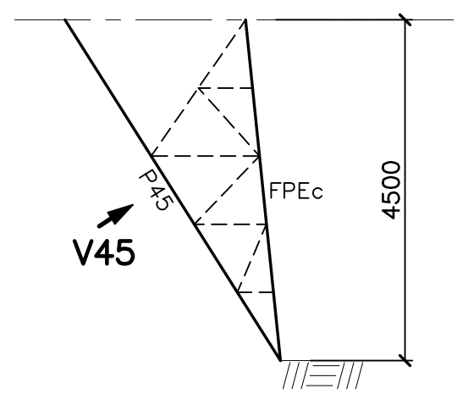

PÉ 4,50m

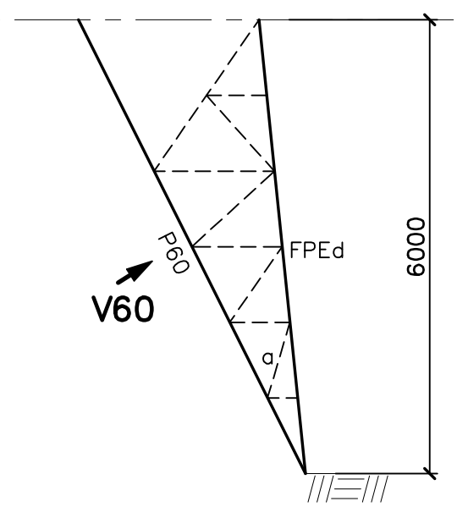

PÉ 6,00m

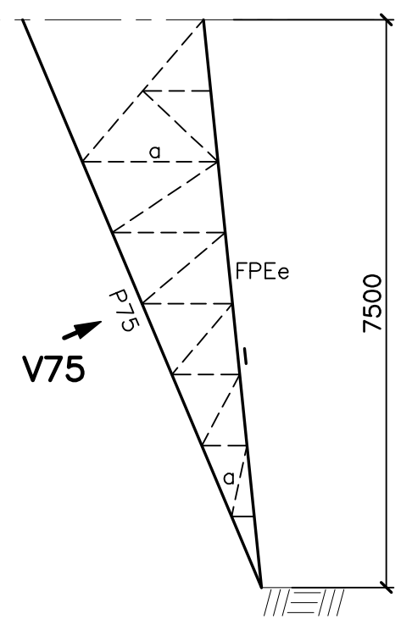

PÉ 7,50m

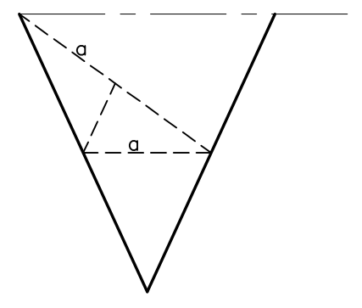

Vista V30
Vista VE30

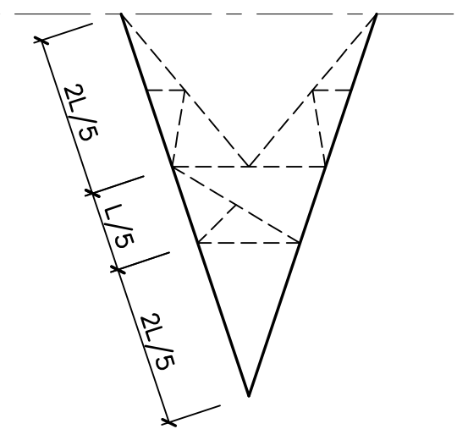

Vista V45

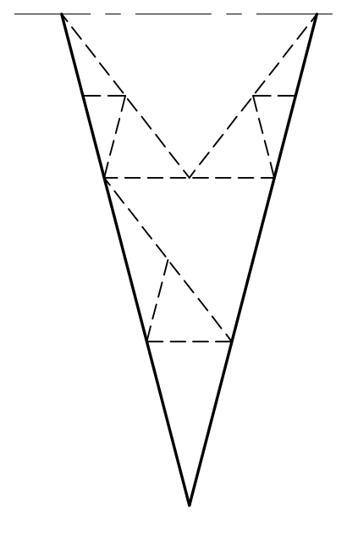

Vista V60

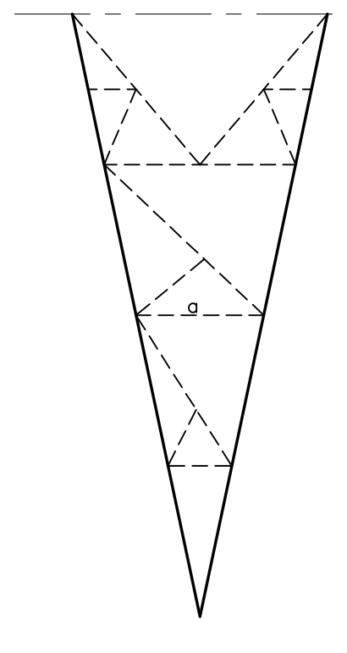

Vista V75
Vista VE75

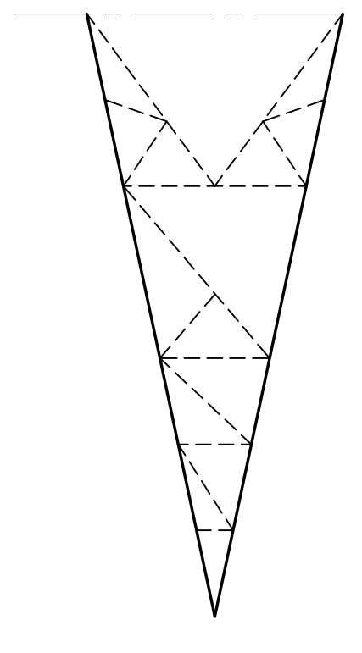

Vista VE40

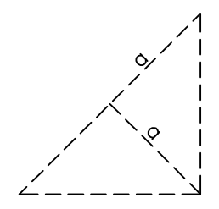

Seção X–X

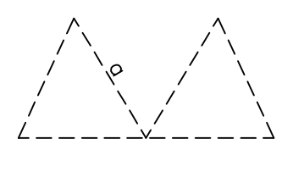

Seção A10–A10

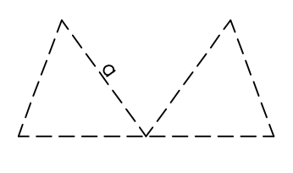

Seção A20–A20

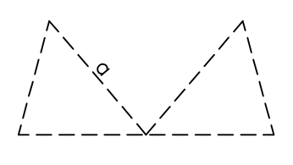

Seção A30–A30

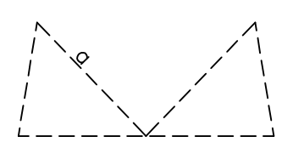

Seção A40–A40

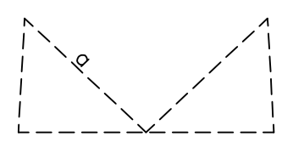

Seção A50–A50

1. Todas as cotas estão em milímetro.
2. Barras descarregadas:
   Não indicadas: L40x40x3,0H – 1ø12.0
   a) L45x45x3,0H – 1ø12.0
   b) L50x50x3,0H – 1ø12.0
   c) L50x50x4,0H – 1ø12.0
   d) L60x60x4,0H – 1ø12.0
3. Para memória de cálculo ver doc. BNSM_ADR2451-M2001.

NOTAS

NÚMERO	TÍTULO
N°_DO_DOCUMENTO	TÍTULO DO DOCUMENTO DE REFERÊNCIA

DOCUMENTOS DE REFERÊNCIA

REV.	DESCRIÇÃO	DATA	ELABORAÇÃO	VERIFICAÇÃO
00	APROVADO	26/08/26	MDR	HDG
00C	CONFORME COMENTÁRIOS	11/08/26	MDR	HDG
00B	CONFORME COMENTÁRIOS	17/07/26	L.PENIDO	HDG
00A	EMISSÃO INICIAL	13/03/26	CSC	HDG

N° CR GONTIJO
BNSM_ADR2451-D2001

PROPRIEDADE
AXIA ENERGIA

AUTORIA
AG CONSAG CONSÓRCIO CONSTRUTOR SÃO FRANCISCO ENGENHARIA
CR GONTIJO Engenharia de Projetos

APROVAÇÃO
HENRIQUE GONTIJO
RESPONSÁVEL TÉCNICO
CREA 108382/MG

RESPONSÁVEL TÉCNICO

LOTE 05 – ANEEL 01/2024

DESCRIÇÃO DESENHO

TORRE AUTOPORTANTE DE SUSPENSÃO MÉDIA TIPO BNSM

SILHUETA

DESCRIÇÃO PROJETO

NOVA ERA INTEGRAÇÃO
LOTE 5 – LT 230 kV
BOM NOME – BOM NOME II C1 E C2

CÓDIGO PROJETO	FORMATO	N° DESENHO	
LTNEI	A0	LTRH1.06–230–PE–EM.DDM–0002	
CLASSIFICAÇÃO	ESCALA	FOLHA	REVISÃO
EXECUTIVO.BÁSICO.PADRÃO	1/100	1	00