
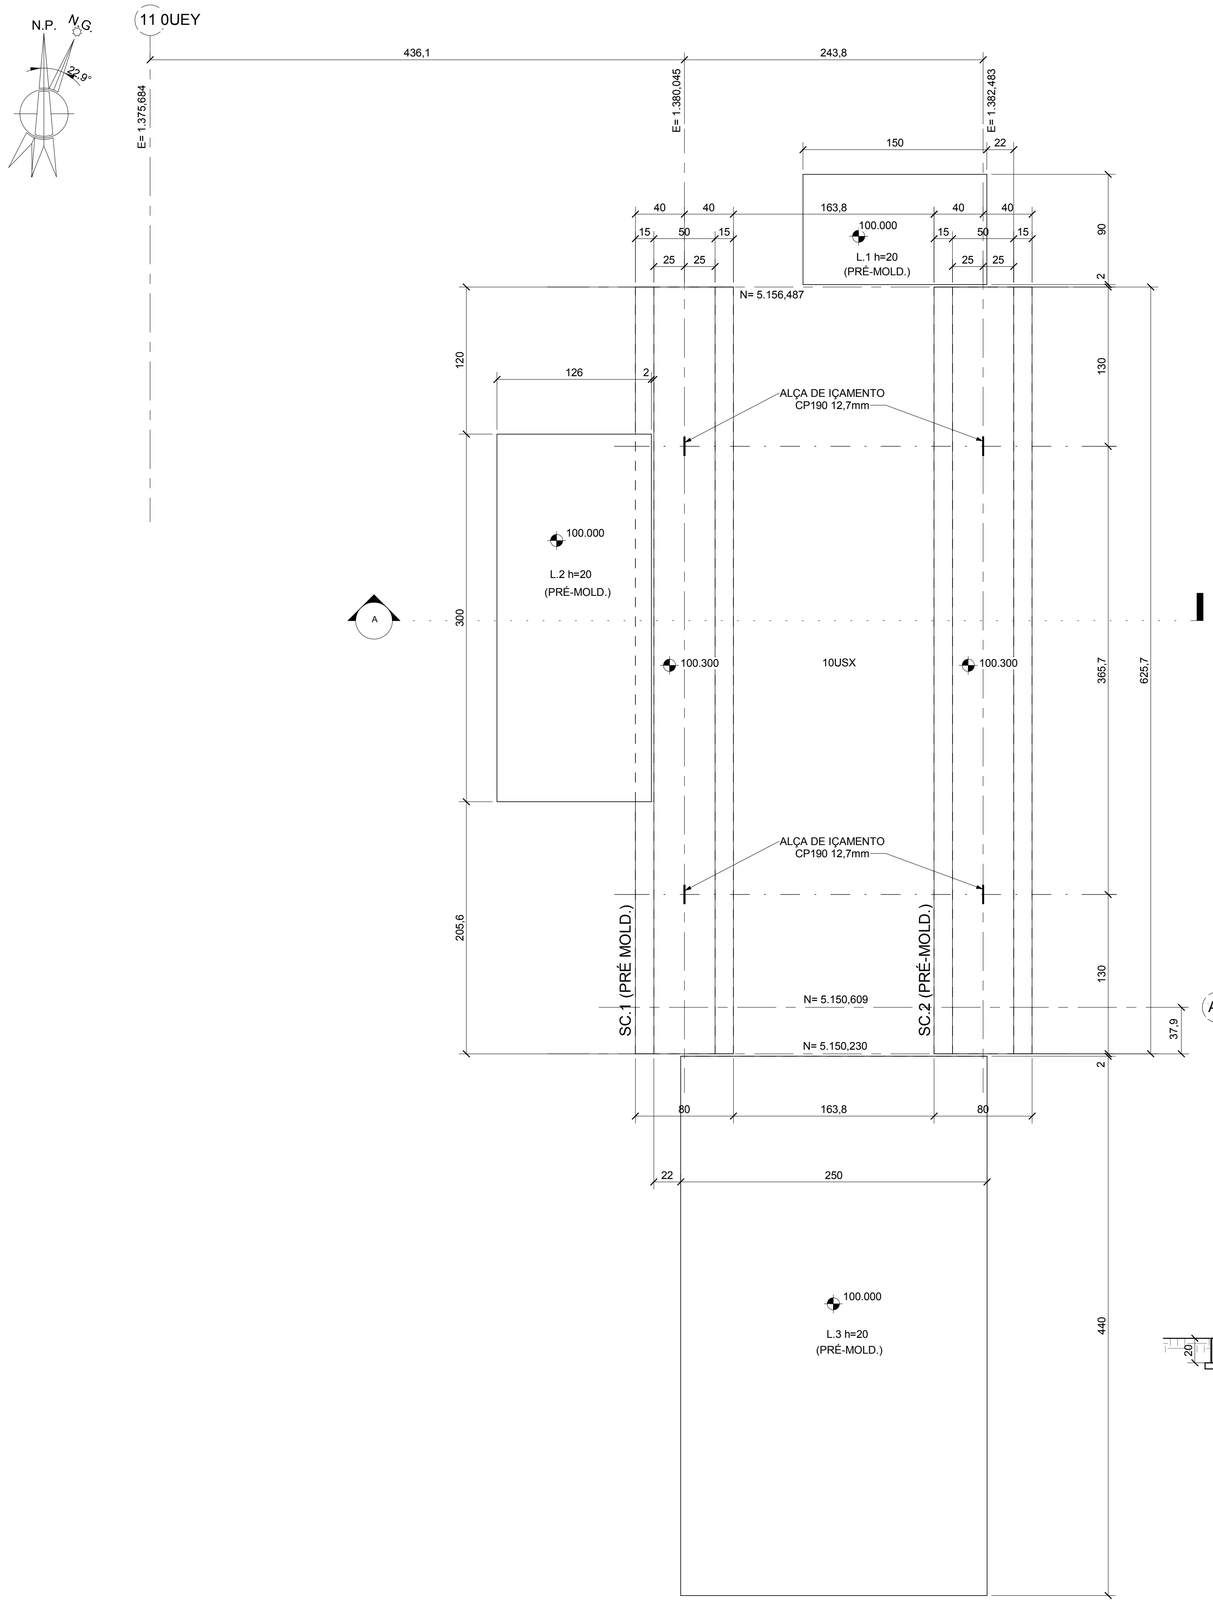


PLANTA DA BASE - LOCAÇÃO


ESCALA: 1 : 25

TRANSFORMAÇÃO DE COORDENADAS	
COORDENADAS DE PROJETO	COORD. UTM SIRGAS 2000
E: 1.000,000	X = 291.392,622
N: 5.000,000	Y = 7.582.694,937
TRANSFORMAÇÃO DE ELEVAÇÃO	
ELEVAÇÃO	ELEVAÇÃO EM RELAÇÃO AO NÍVEL MÉDIO DO MAR
+100,000 (m)	+5,200 (m)

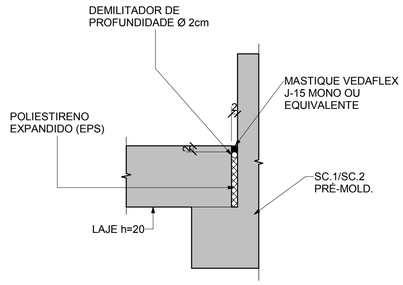


DET. 1 - JE (TÍP.)

JUNTA DE ENCONTRO (JE)	
MASTIQUE VEDAFLEX J-15 MONO OU EQUIV.	4,0 m.
DEMILITADOR DE PROFUNDIDADE Ø 2cm	
POLIESTIRENO EXPANDIDO (EPS)	

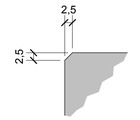

CHANFRO EM ARESTAS-DET.TIP

ESCALA: 1 : 10

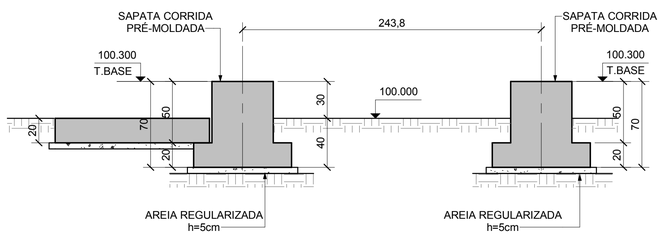

CORTE A

ESCALA: 1 : 25

DOCUMENTOS DE REFERÊNCIA:

BR1045-10QCD10-&MLH020-445128 - MS2 INPUT FOR AMMONIA DOSING SYSTEM
NOVO-SRCA-SP-0004-CIVIL - ESPECIFICAÇÃO TÉCNICA PARA CIVIL E ARQUITETURA
NOVO-SRCA-SP-0003 - ESPECIFICAÇÃO TÉCNICA DE TERRAPLENAGEM
NOVO-SRCA-CD-0001 - CRITÉRIOS DE PROJETO CIVIL
BR1045-11UEN-&CLH011-633014-STRUCTURE FOR FUEL GAS REDUCING

NOTAS

1 - MEDIDAS EM CENTÍMETRO, BITOLAS EM MILÍMETRO, NÍVEIS E COORDENADAS EM METRO, EXCETO ONDE INDICADO.

2 - MATERIAIS :

- CONCRETO ESTRUTURAL C30 fck ≥ 30MPa
- CONCRETO MAGRO C10 fck ≥ 10MPa.
- RELAÇÃO a/c (ÁGUA/CIMENTO) ≤ 0,50 CLASSE DE AGRESSIVIDADE III
- CONSUMO DE CIMENTO ≥ 320 kg/m³
- MÓDULO DE ELASTICIDADE Ecs ≥ 26,8 GPa (AGREGADO GRAÚDO-GNAISSE)

- AÇO CA-50 fyk≥500 MPa.

- PARA TRANSPORTE, MANUSEIO E DESFORMA:
  fcj >= 20 MPa
  Ecs >= 21 GPa

- PARA A ALÇA: CORDOALHA CP 190 RB 12,7mm

3 - PARA CONTROLE TECNOLÓGICO DO CONCRETO SEGUIR RIGOROSAMENTE AS ESPECIFICAÇÕES DA NBR 12655 "CONCRETO-PREPARO, CONTROLE E RECEBIMENTO".

4 - A TENSÃO APLICADA NA COTA DE APOIO NA FUNDAÇÃO DIRETA É DE 0,45kgf/cm².

REV.	DESCRIÇÃO	DATA	DES.	VERIF.	APROV.
2	REVISÃO ONDE INDICADO/EMITIDO PARA CONSTRUÇÃO	30-07-18	J.K.Y.	M.P.R.	E.R.P.
1	REVISÃO ONDE INDICADO/EMITIDO PARA CONSTRUÇÃO	17-07-18	J.K.Y.	M.P.R.	E.R.P.
0	EMISSÃO INICIAL / EMITIDO PARA CONSTRUÇÃO	22-06-18	G.P.V.	M.P.R.	E.R.P.

REVISÕES

CONTRATANTE: SIEMENS / ANDRADE GUTIERREZ CONSÓRCIO ADJ

ENGENHARIA SUBCONTRATADA: SENER

CLIENTE: **UTE GNA I** Gás Natural Açu S.A.

© SENER, SETE PLA TECNOMETAL ENGENHARIA E SISTEMAS S.A.
AS INFORMAÇÕES CONTIDAS NESTE DOCUMENTO SÃO CONFIDENCIAIS E RESTRITAS, E DEVEM SER UTILIZADAS SOMENTE PARA FINS ESTABELECIDOS NO DOCUMENTO. MODIFICAÇÃO, EXPLORAÇÃO, REPRODUÇÃO, COMUNICAÇÃO A QUALQUER TERCEIRO, EXPLORAÇÃO OU DISTRIBUIÇÃO DE TODO OU QUALQUER PARTE DO DOCUMENTO NÃO É PERMITIDO SEM O CONSENTIMENTO PRÉVIO POR ESCRITO DA SENER SETE PLA TECNOMETAL ENGENHARIA E SISTEMAS S.A. A FALTA DE RETORNO SOBRE TAL CONSENTIMENTO NÃO DEVE, EM HIPÓTESE ALGUMA, SER INTERPRETADA COMO AUTORIZAÇÃO PARA USO DA INFORMAÇÃO.

No ARQUIVO CAD :	NOVO-SRCA-PC-0509-01 Rev 2
ESCALA :	
REFERÊNCIA :	P0Q27003
TAMANHO ORIGINAL	A1
PROJETO:	UTE GNA I PLANTA DE CICLO COMBINADO PORTO DO AÇU - RIO DE JANEIRO
No DESENHO SUBCONTRATADA:	NOVO-SRCA-PC-0509
No DESENHO CLIENTE:	
No DESENHO SAG:	BR1045-30710-&CLB020-102139
TÍTULO DO DESENHO:	FUNDAÇÃO DO SISTEMA DE DOSAGEM *DOSING SYSTEM FOUNDATION - FORMS/STEEL REINFORCEMENT* LOCAÇÃO DA FUNDAÇÃO
FL.	01
PRÓX.	02

DIN A1 (841 x 594)