Eletrobras
APROVADO
Por: Wallace Castro em 01/09/2026

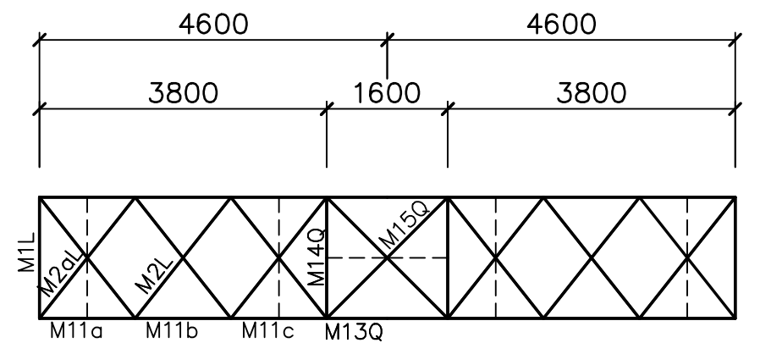

CORTE B-B

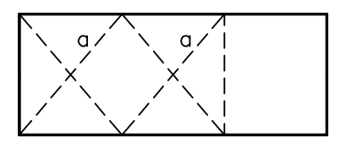

VISTA F

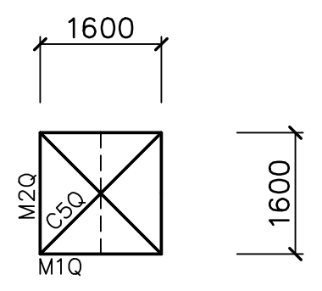

CORTE C-C

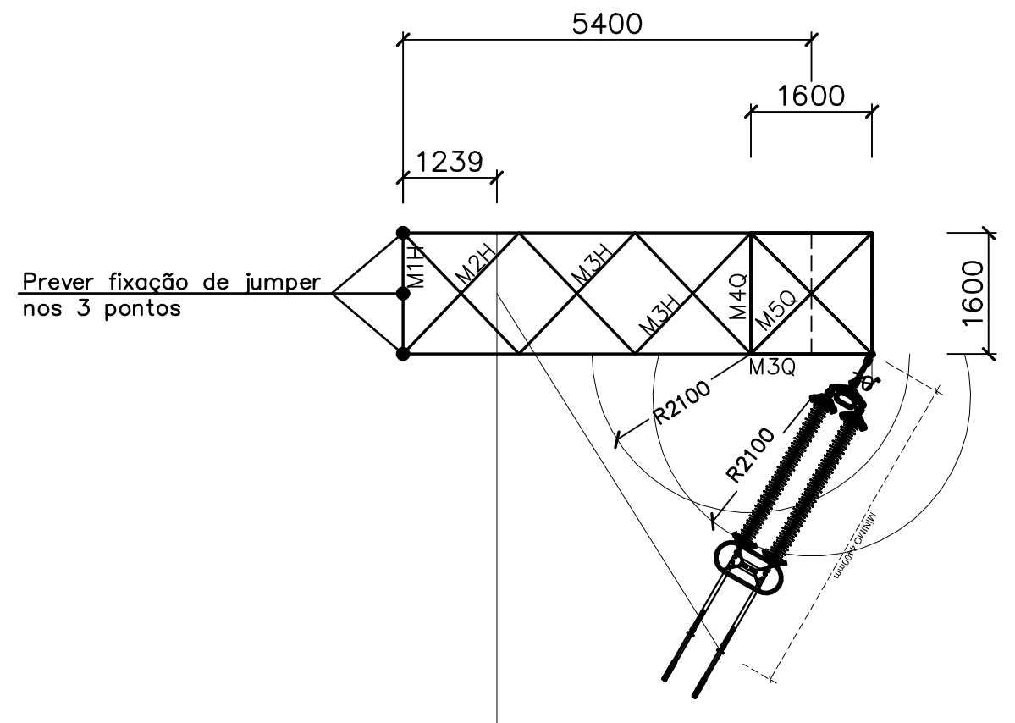

CORTE A-A

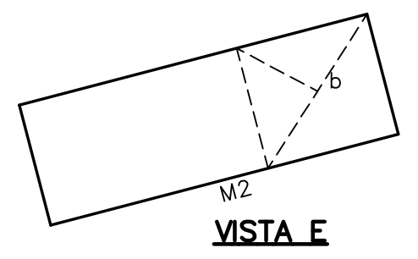

VISTA E

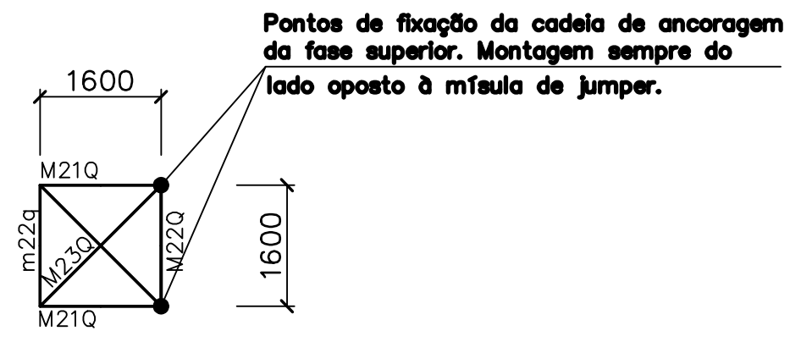
1600
1600
M21Q
m22q
M22Q
Pontos de fixação da cadeia de ancoragem da fase superior. Montagem sempre do lado oposto à mísula de jumper.

CORTE D-D

– PARA TORRE EM ALINHAMENTO e ATÉ 30°: devem ser usadas duas cadeias de suspensão do jumper

– PARA TORRE EM ÂNGULO ACIMA DE 30° (30° a 60°): usada apenas uma cadeia de suspensão do jumper na posição central da mísula.

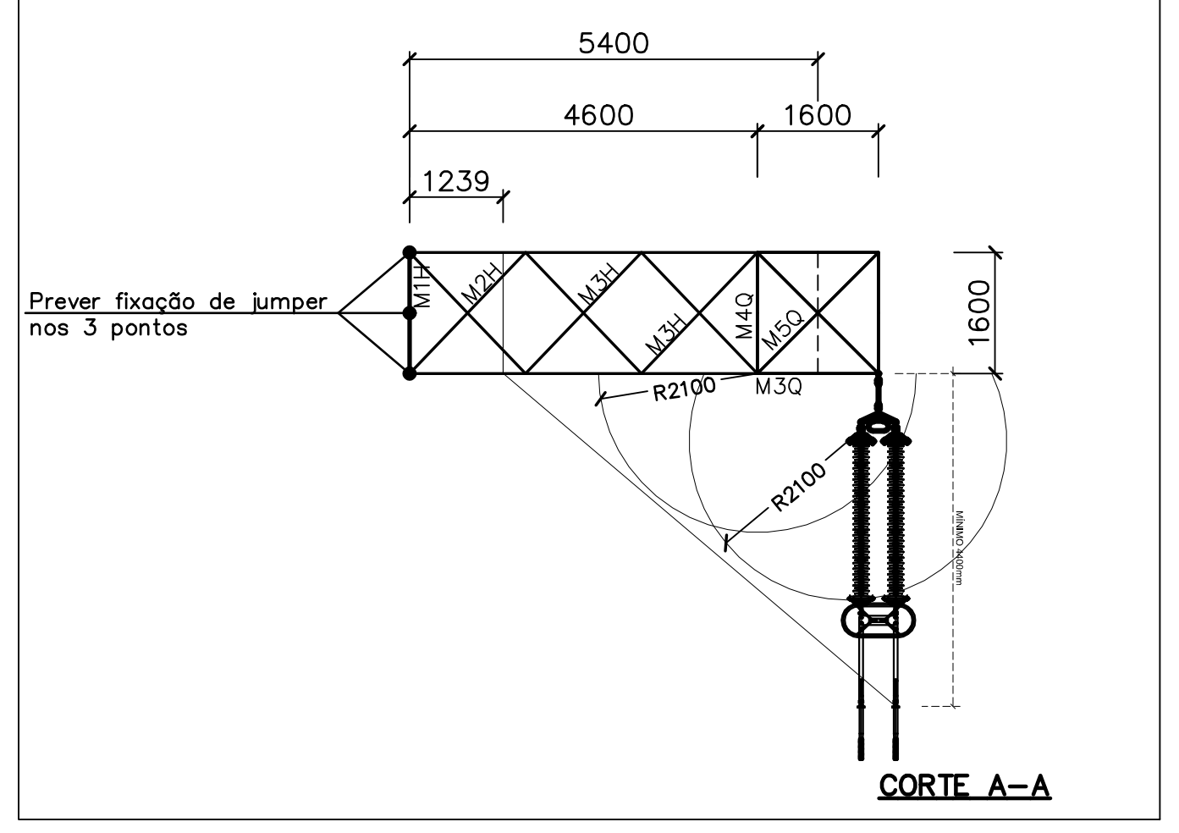

CORTE A-A

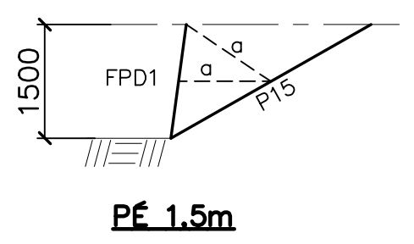

PÉ 1,5m

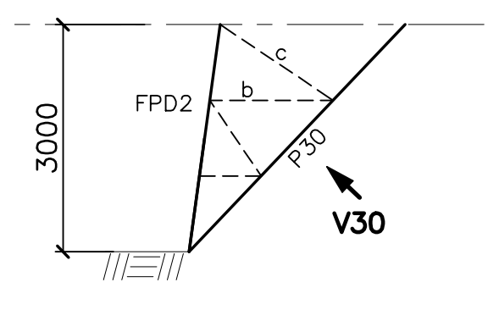

PÉ 3,0m

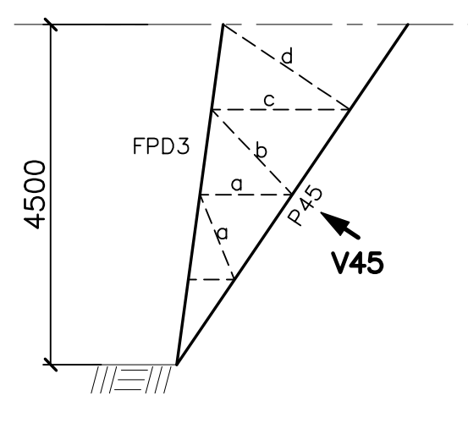

PÉ 4,5m

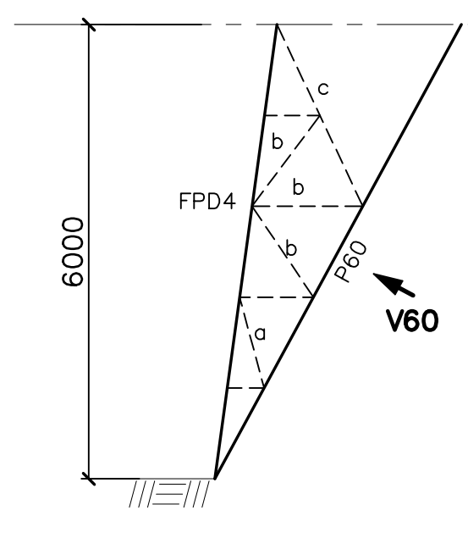

PÉ 6,0m

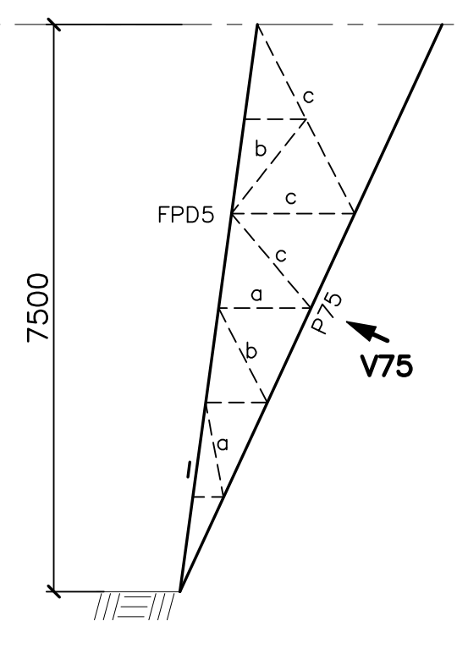

PÉ 7,5m

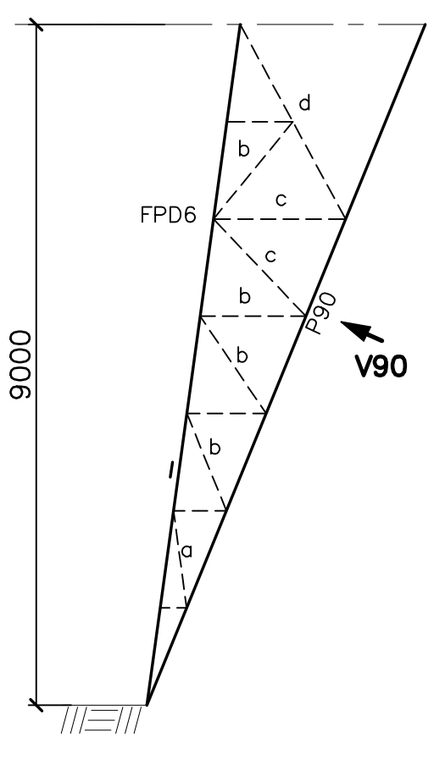

PÉ 9,0m

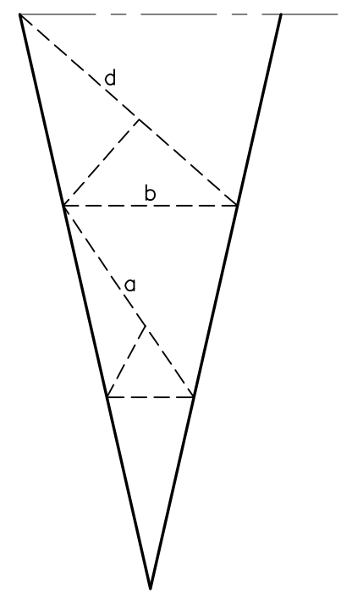

VISTA V70

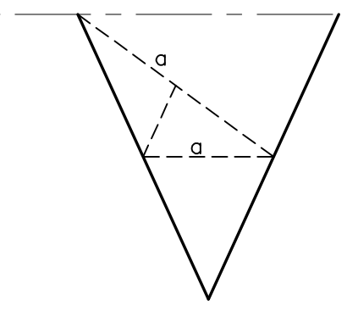

VISTA V30

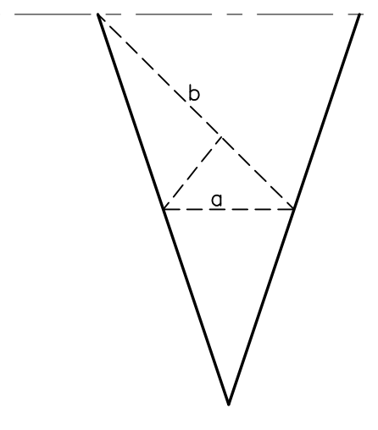

VISTA V45

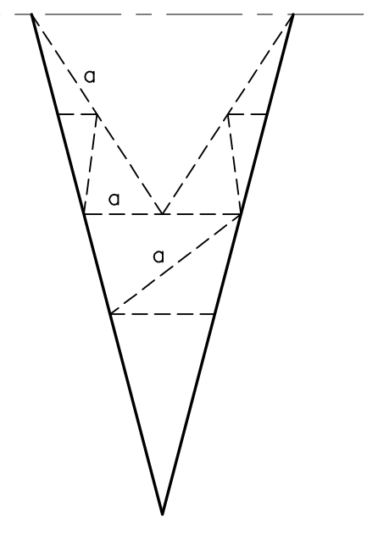

VISTA V60

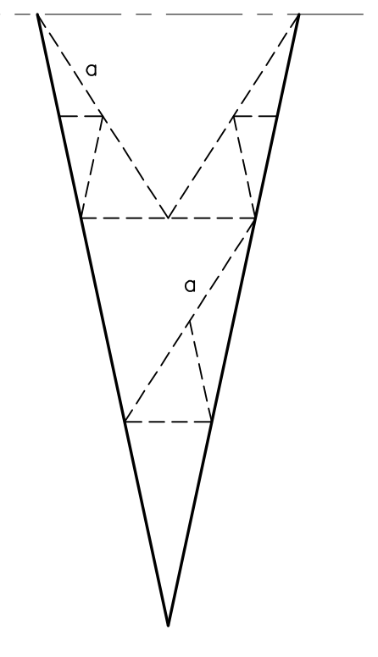

VISTA V75

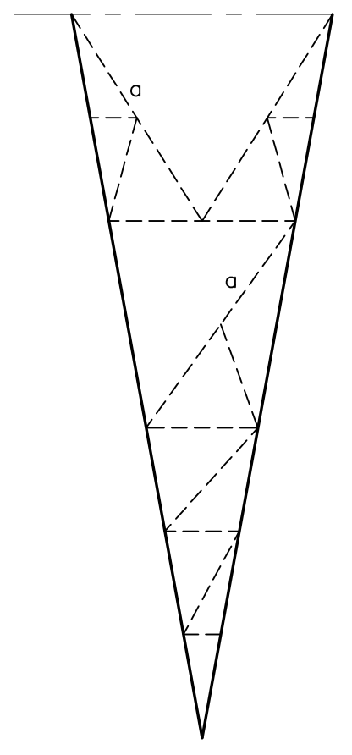

VISTA V90

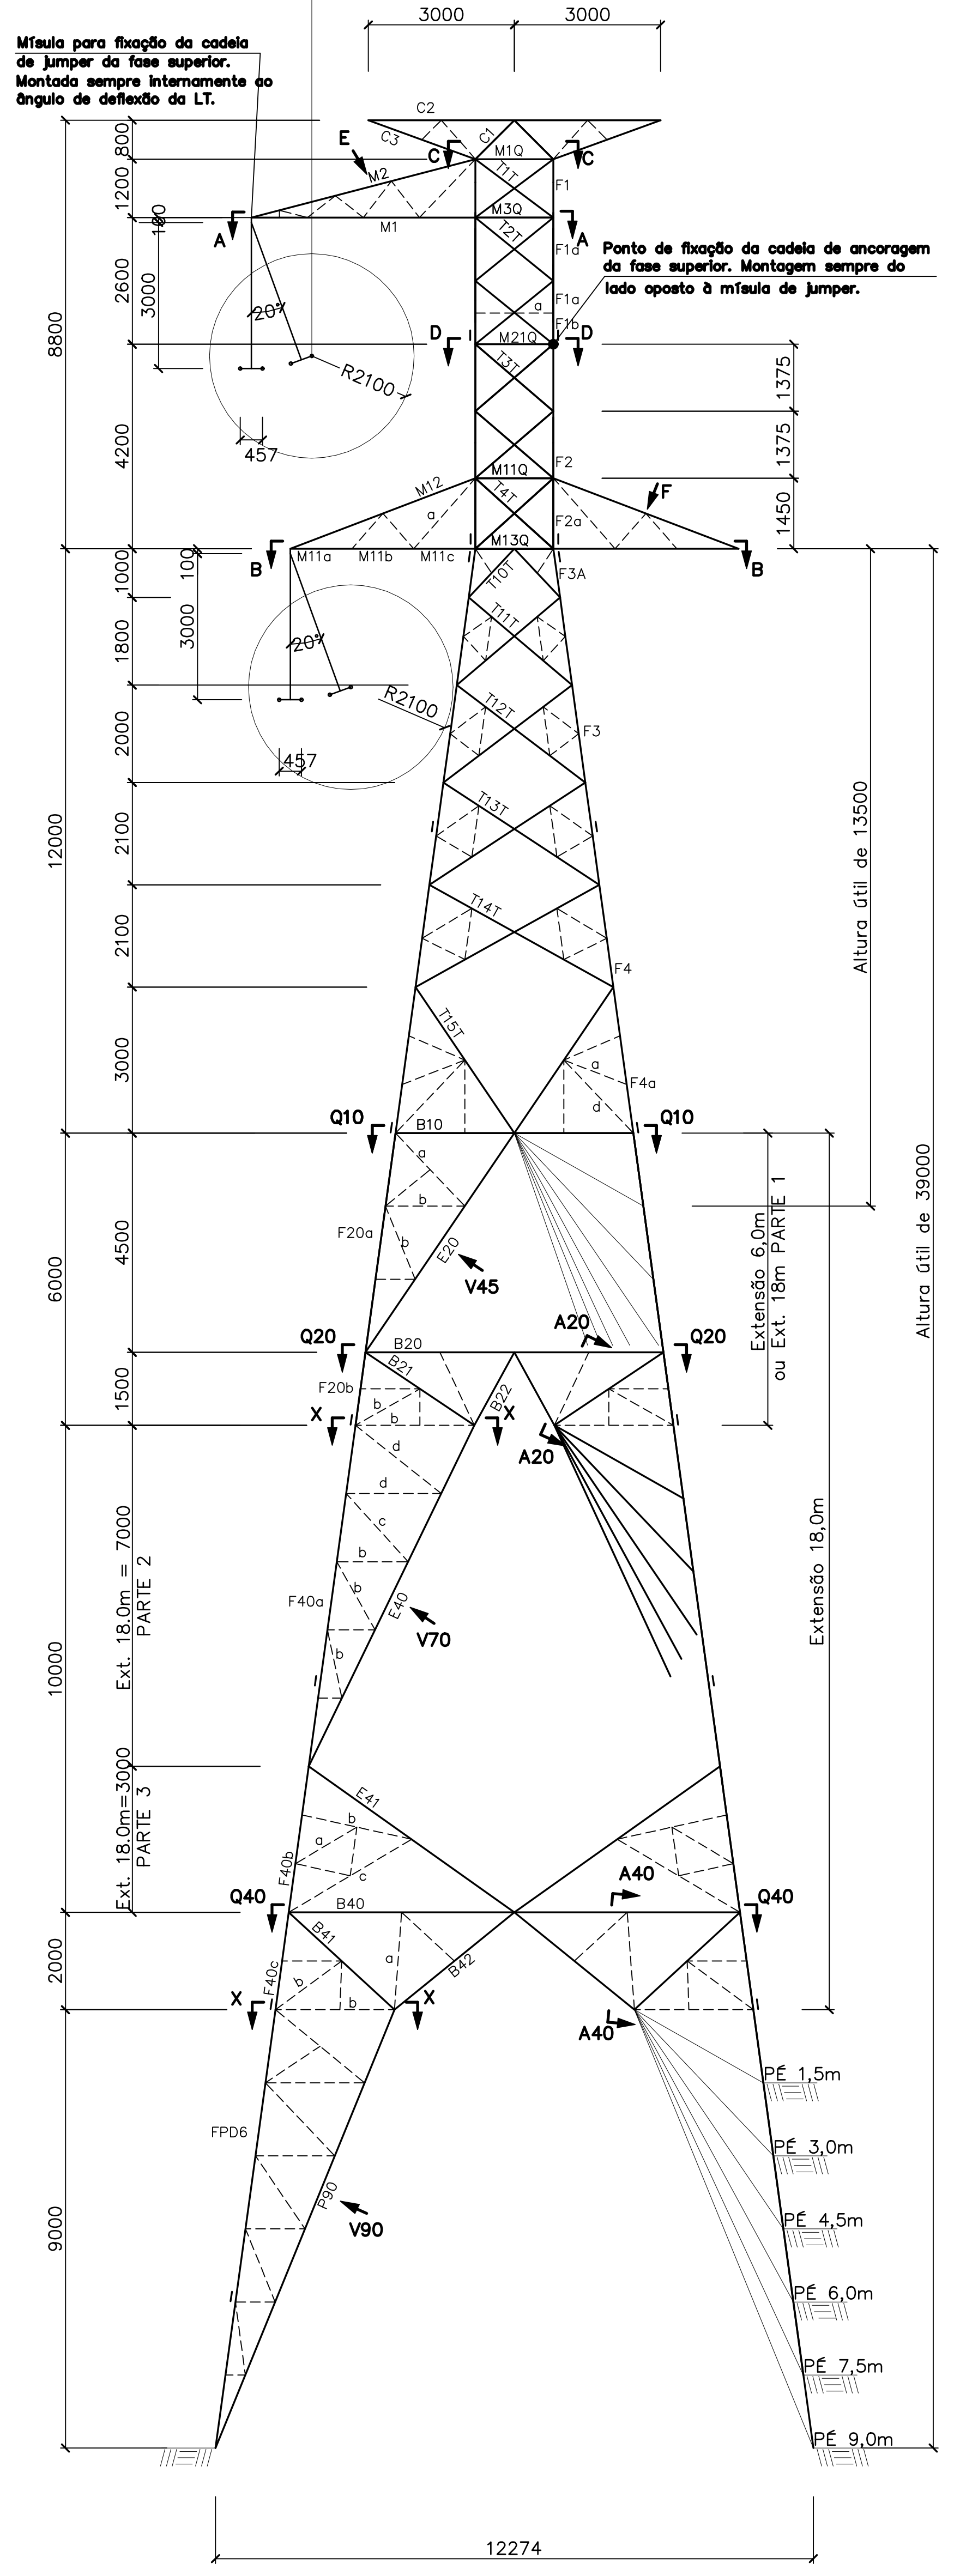
3000
3000
Mísula para fixação da cadeia de jumper da fase superior. Montada sempre internamente ao ângulo de deflexão da LT.
Ponto de fixação da cadeia de ancoragem da fase superior. Montagem sempre do lado oposto à mísula de jumper.
C2
C3
M1Q
M2
M1
M3Q
M21Q
M11Q
M12
M13Q
M11a
M11b
M11c
R2100
R2100
20°
20°
457
457
8800
12000
6000
10000
9000
Altura Útil de 13500
Altura Útil de 39000
Extensão 6,0m ou Ext. 18m PARTE 1
Ext. 18,0m = 7000 PARTE 2
Ext. 18,0m=3000 PARTE 3
Extensão 18,0m
Q10
Q20
Q40
A20
A40
B10
B20
B40
V45
V70
V90
F20a
F20b
F40a
FPD6
X
PÉ 1,5m
PÉ 3,0m
PÉ 4,5m
PÉ 6,0m
PÉ 7,5m
PÉ 9,0m
12274

FACE TRANSVERSAL

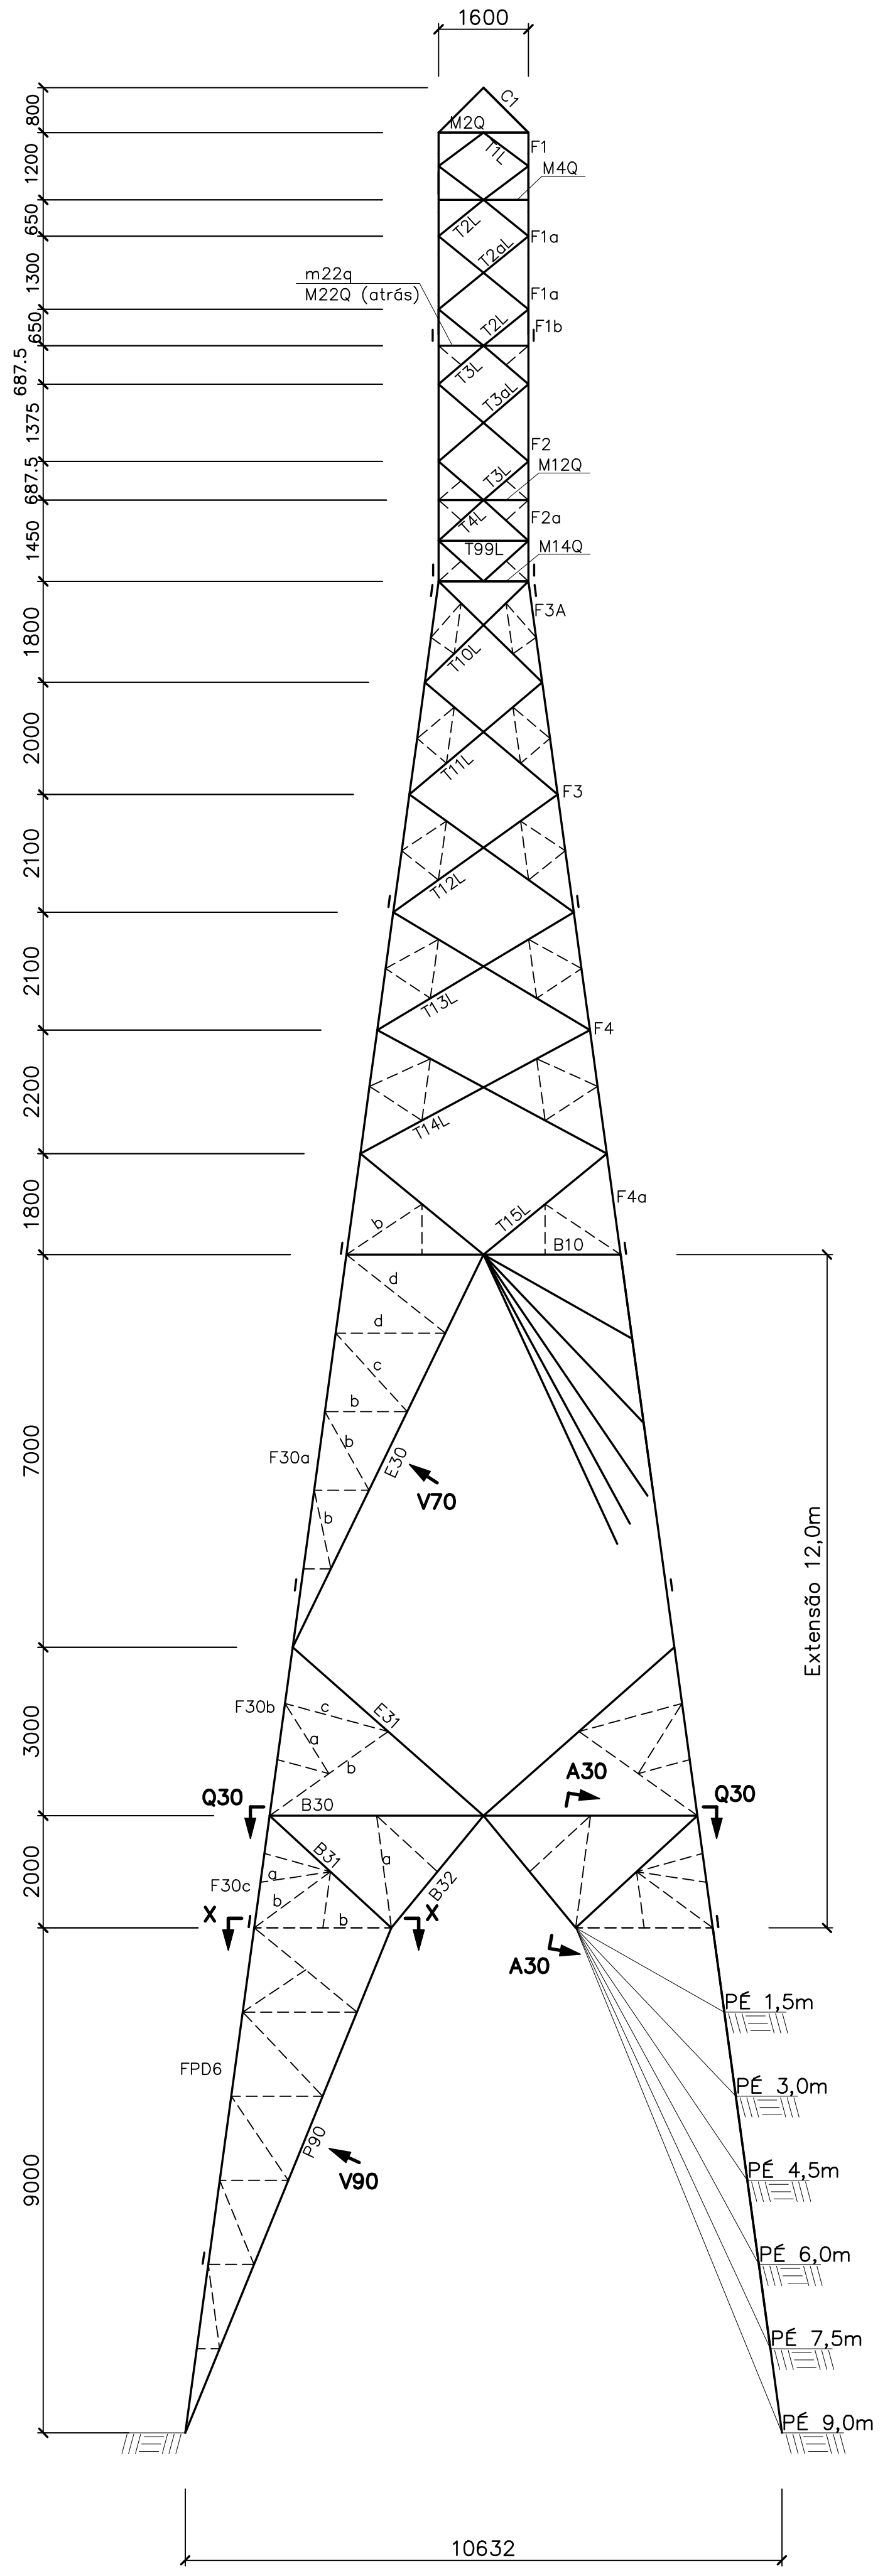

FACE LONGITUDINAL

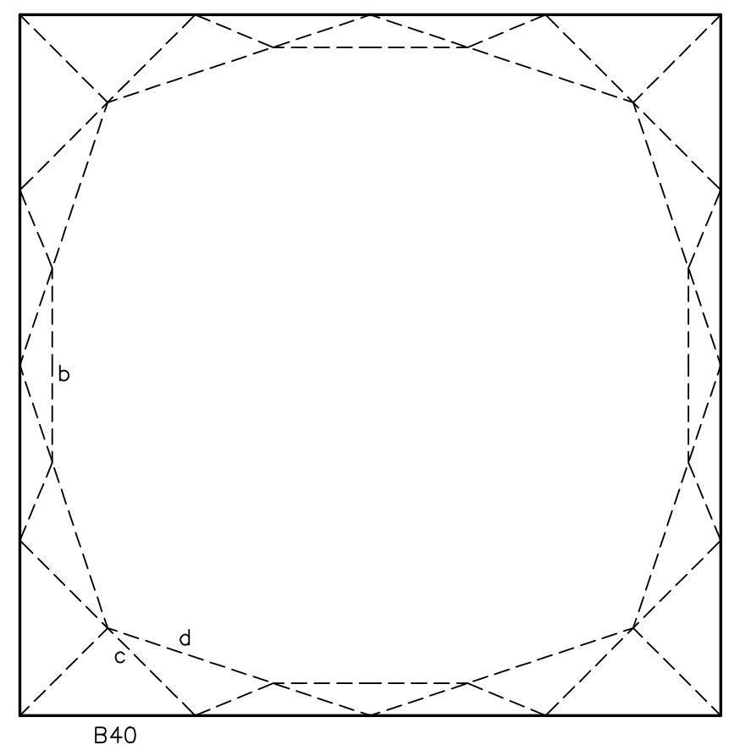

CORTE Q40–Q40

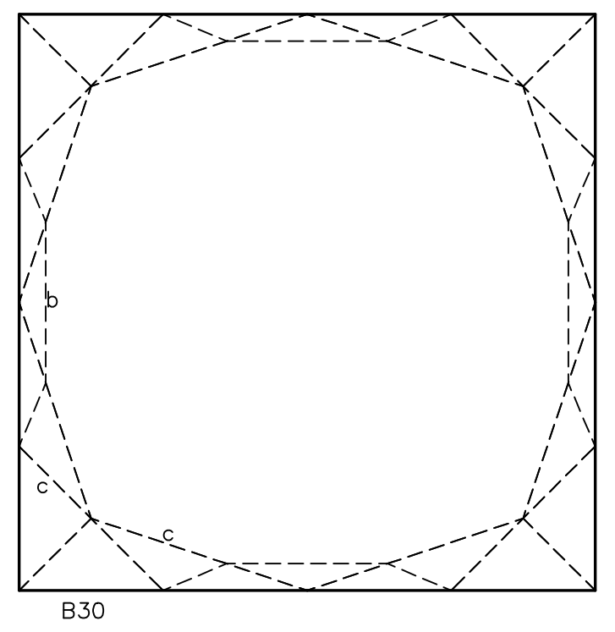

CORTE Q30–Q30

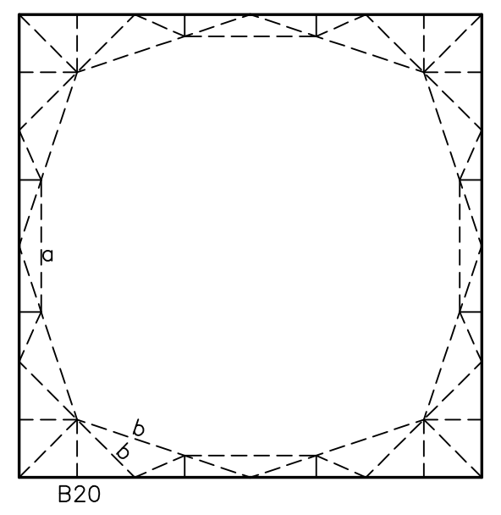

CORTE Q20–Q20

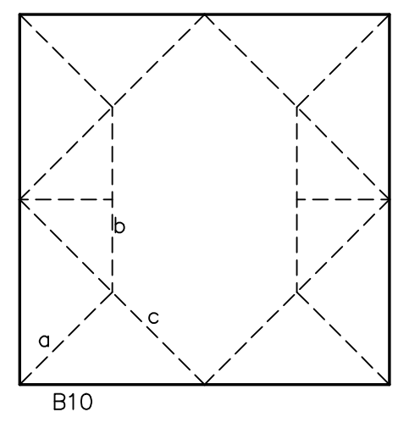

CORTE Q10–Q10

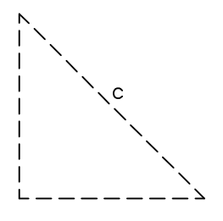

CORTE X–X

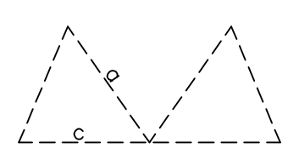

CORTE A20–A20

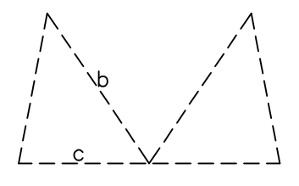

CORTE A30–A30

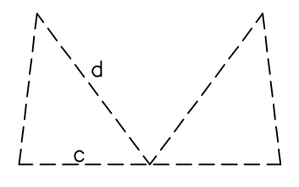

CORTE A40–A40

PADRÃO DE IMPRESSÃO		
DETC.ctb		
COR CAD	ESPESSURA (mm)	COR IMPRESSÃO
1	0,1	7
2	0,2	7
3	0,3	7
4	0,4	7
5	0,5	7
6	0,6	7
7	0,15	7
8	0,1	7
9	0,05	7
11	0,05	7
41	0,05	7

AS DEMAIS CORES DEVEM SER IMPRESSAS EM SUAS RESPECTIVAS CORES COM ESPESSURA DE 0.20 mm.

1. Todas as cotas estão em milímetro.
2. Barras descarregadas:
   Não indicadas: L40x40x3,0H – 1ø12.0
   a) L45x45x3,0H – 1ø12.0
   b) L50x50x3,0H – 1ø12.0
   c) L50x50x4,0H – 1ø12.0
   d) L60x60x4,0H – 1ø12.0
3. Para memória de cálculo ver doc. BNAT_ADR2451–M4001.

NOTAS

NÚMERO	TÍTULO
N°_DO_DOCUMENTO	TÍTULO DO DOCUMENTO DE REFERÊNCIA

DOCUMENTOS DE REFERÊNCIA

REV.	DESCRIÇÃO	DATA	ELABORAÇÃO	VERIFICAÇÃO
00	APROVADO	31/08/2026	MICHAEL RODRIGUES	RANIA PEIXOTO
00A	EMISSÃO INICIAL	20/03/2026	CRISTINA CASSIMIRO	RANIA PEIXOTO

N° CR GONTIJO
BNAT_ADR2451–D4001

PROPRIEDADE
Eletrobras
SPE Nova Era Integração Transmissora S.A.

AUTORIA
AG CONSAG ENGENHARIA CONSÓRCIO CONSTRUTOR SÃO FRANCISCO
CR GONTIJO ENGENHARIA DE PROJETOS

LOTE 05 – ANEEL 01/2024

DESCRIÇÃO DESENHO
TORRE DE ANCORAGEM MEIO DE LINHA PESADA e FIM DE LNHA TIPO BNAT
SILHUETA

APROVAÇÃO
HENRIQUE GONTIJO
RESPONSÁVEL TÉCNICO
CREA 108382/MG

RESPONSÁVEL TÉCNICO

DESCRIÇÃO PROJETO
NOVA ERA INTEGRAÇÃO
LOTE 5 – LT 230 kV
BOM NOME – BOM NOME II C1 E C2

CÓDIGO PROJETO	FORMATO	N° DESENHO	
LTNEI	A0	LTRH1.06–230–PE–EM.DDM–0004	
CLASSIFICAÇÃO	ESCALA	FOLHA	REVISÃO
EXECUTIVO.BÁSICO.PADRÃO	1/100	1	00