
SENER	PADRÃO DE ESCADAS E CORRIMÃOS	Nº DES. PADRÃO PEC-200
DESENHO PADRÃO	ESCADA TIPO MARINHEIRO	EMISSÃO INICIAL 12/12/2017 / FOLHA 1/1
	FIXAÇÃO EM ESTRUTURA METÁLICA - SAÍDA FRONTAL	DATA REV. 19/06/2018 / REV. 3

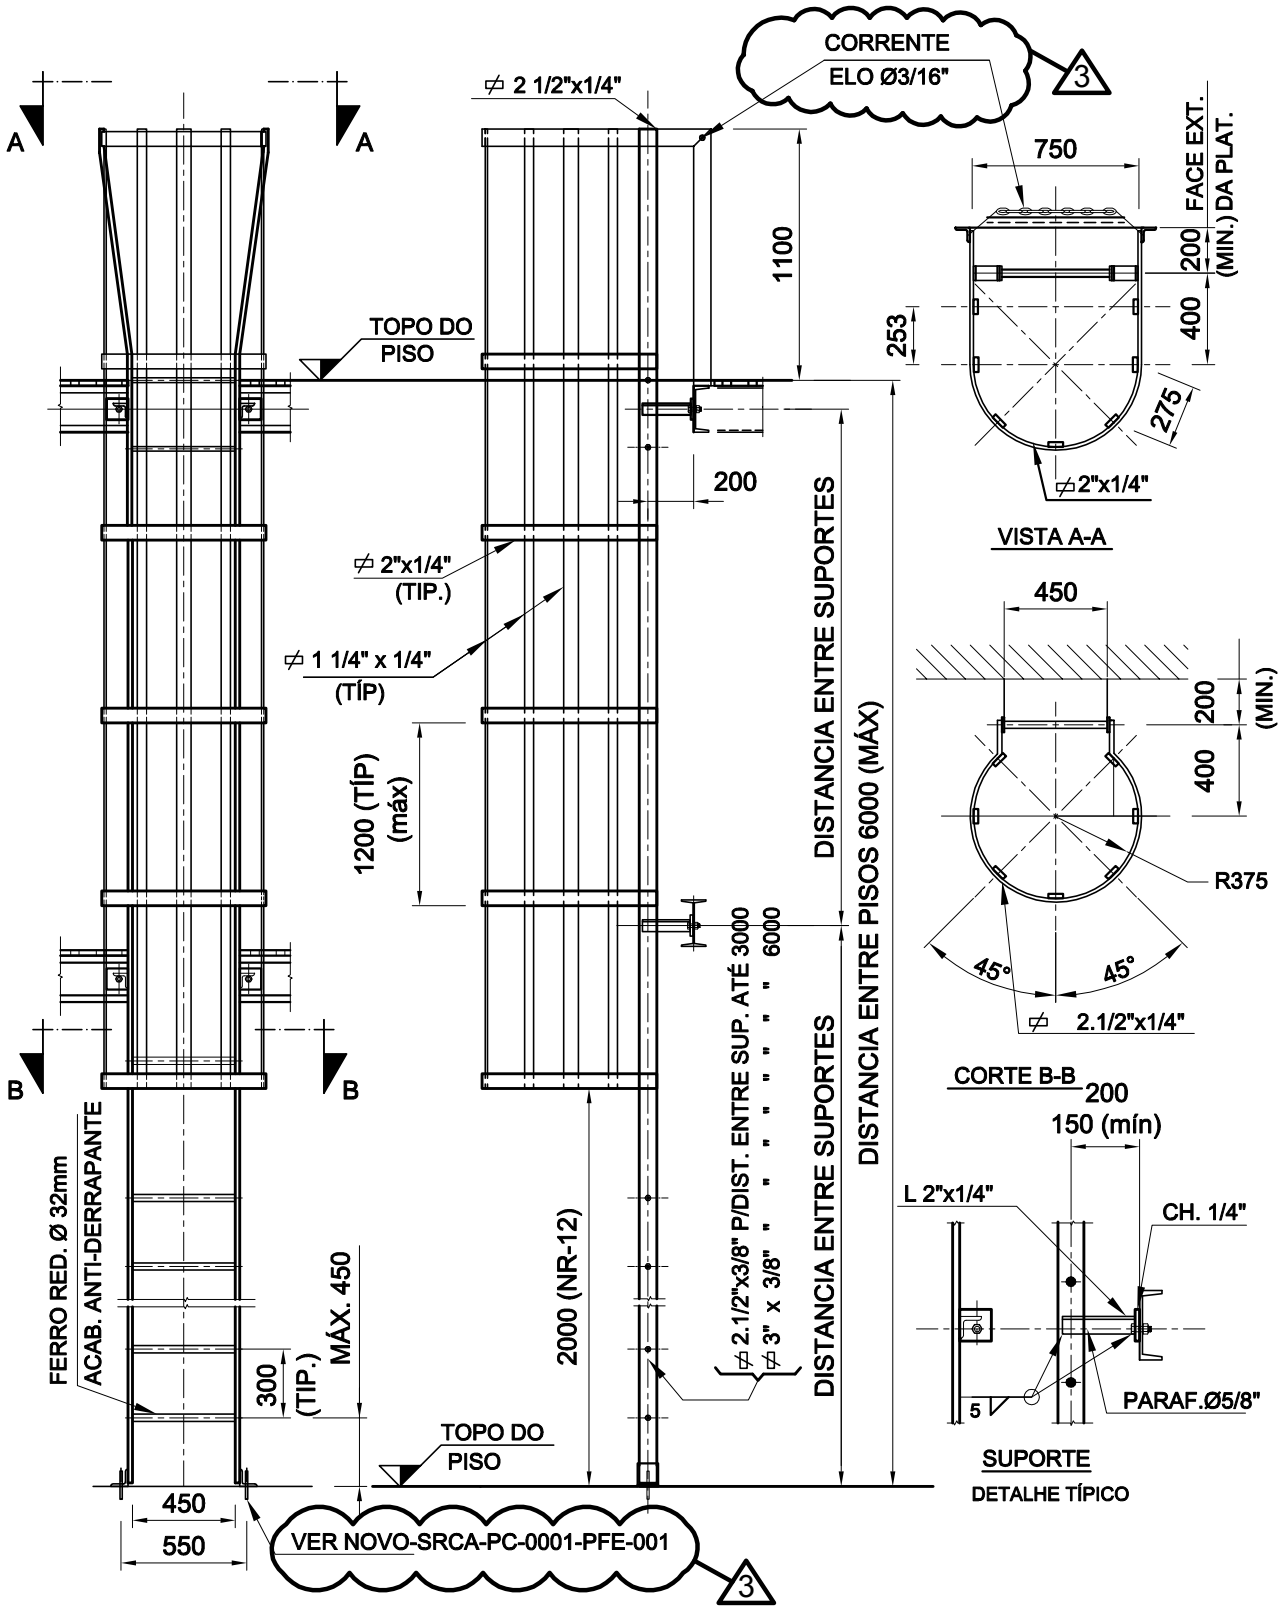

NOTAS:

1-MEDIDAS EM MILIMETROS (EXCETO ANOTADO)

2-MATERIAL: AÇO ESTRUTURAL ASTM A36
SOLDA CONFORME AWS-ELETRODO E70XX
PARAFUSOS ASTM A307
FERRO REDONDO SAE 1010/1020

3-TODA ESCADA COM LANCE ENTRE PISOS IGUAL OU MAIOR A 2000mm, DEVE TER GAIOLA DE SEGURANÇA

4-NO CASO DE DIVERGÊNCIA ENTRE ESTE PADRÃO E O DES. DE PROJETO PREVALECERÁ O ÚLTIMO

© SENER SETEPLA TECNOMETAL ENGENHARIA E SISTEMAS S.A.
AS INFORMAÇÕES CONTIDAS NESTE DOCUMENTO SÃO CONFIDENCIAIS E RESTRITAS, E DEVEM SER UTILIZADAS SOMENTE PARA FINS ESTABELECIDOS NO DOCUMENTO. MODIFICAÇÃO, EXPLORAÇÃO, REPRODUÇÃO, COMUNICAÇÃO A QUALQUER TERCEIRO, DIFUSÃO OU DISTRIBUIÇÃO DE TODO OU QUALQUER PARTE DO DOCUMENTO NÃO É PERMITIDO SEM O CONSENTIMENTO PRÉVIO POR ESCRITO DA SENER, SETEPLA TECNOMETAL ENGENHARIA E SISTEMAS S.A. A FALTA DE RETORNO SOBRE TAL CONSENTIMENTO NÃO DEVE, EM HIPÓTESE ALGUMA, SER INTERPRETADA COMO AUTORIZAÇÃO PARA USO DA INFORMAÇÃO.