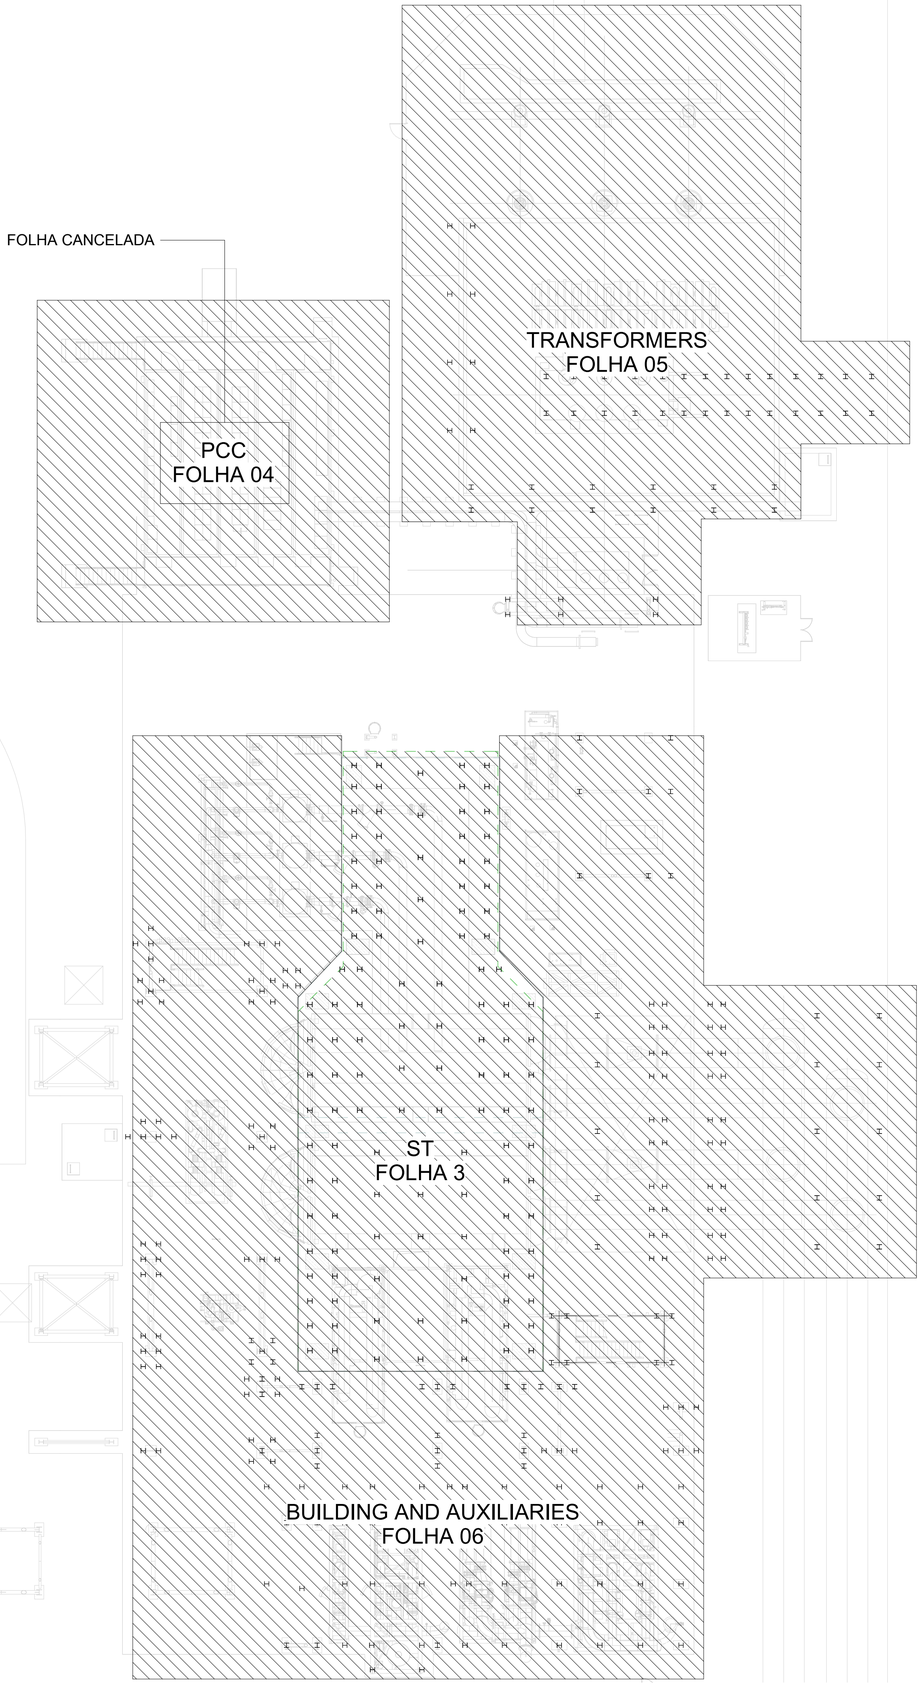


PLANTA GERAL DA ÁREA DA TURBINA A VAPOR

ESCALA: 1 : 200

ANDRADE GUTIERREZ CONSÓRCIO AÇU | ENGINEERING MANAGEMENT


AFC - APPROVED FOR CONSTRUCTION

Date: 30/087/2018 | Milton Sanches

RELEASED BY DISCIPLINE

NOTAS:

1 - VER NOTAS GERAIS NAS FOLHAS DE 03 A 06.

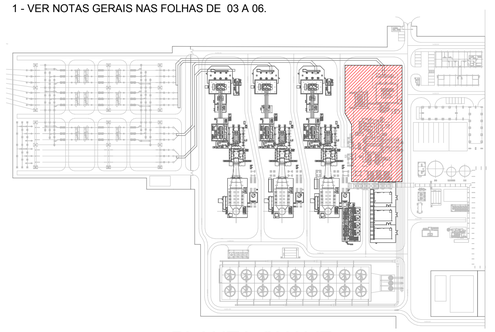

PLANTA CHAVE

TRANSFORMAÇÃO DE COORDENADAS	
COORDENADAS DE PROJETO	COORD. UTM SIRGAS 2000
E: 1.000,000	X = 291.392,622
N: 5.000,000	Y = 7.582.694,937
TRANSFORMAÇÃO DE ELEVAÇÃO	
ELEVAÇÃO	ELEVAÇÃO EM RELAÇÃO AO NÍVEL MÉDIO DO MAR
+100,000 (m)	+5,200 (m)

REV.	DESCRIÇÃO	DATA	DES.	VERIF.	APROV.
4	REV. DO NUMERO SAG	29-08-18	L.R.O.	P.Y.A/M.P.R.	J.A.B.
3	PCC FOLHA 04 - FOLHA CANCELADA / EMITIDO PARA CONSTRUÇÃO	29-06-18	J.K.Y.	M.P.R.	E.R.P.
2	RETIRADAS PENDÊNCIAS - APROV. PARA CONSTRUÇÃO - AFC	13-04-18	L.R.O.	M.P.R.	E.R.P.
1	ESTACAS PENDENTES. PARA CONSTRUÇÃO - IFC.	29-03-18	L.R.O.	M.P.R.	E.R.P.
0	EMISSÃO INICIAL	23-03-18	L.R.O.	M.P.R.	E.R.P.

REVISÕES

CONTRATANTE: SIEMENS / ANDRADE GUTIERREZ CONSÓRCIO AÇU

ENGENHARIA SUBCONTRATADA: SENER

CLIENTE: **UTE GNA I** Gás Natural Açu S.A.

© SENER SETEPLA TECNOMETAL ENGENHARIA E SISTEMAS S.A.
AS INFORMAÇÕES CONTIDAS NESTE DOCUMENTO SÃO CONFIDENCIAIS E RESTRITAS, E DEVEM SER UTILIZADAS SOMENTE PARA FINS ESTABELECIDOS NO DOCUMENTO. MODIFICAÇÃO, EXPLORAÇÃO, REPRODUÇÃO, COMUNICAÇÃO A QUALQUER TERCEIRO, DIFUSÃO OU DISTRIBUIÇÃO DE TODO OU QUALQUER PARTE DO DOCUMENTO NÃO É PERMITIDO SEM O CONSENTIMENTO PRÉVIO POR ESCRITO DA SENER SETEPLA TECNOMETAL ENGENHARIA E SISTEMAS S.A. A FALTA DE RETORNO SOBRE TAL CONSENTIMENTO NÃO DEVE, EM HIPÓTESE ALGUMA, SER INTERPRETADA COMO AUTORIZAÇÃO PARA USO DA INFORMAÇÃO.

No ARQUIVO CAD : NOVO-SRCA-PC-0300_07 FL02_04	PROJETO: UTE GNA I PLANTA DE CICLO COMBINADO PORTO DO AÇU - RIO DE JANEIRO
ESCALA : INDICADA	No DESENHO SUBCONTRATADA: NOVO-SRCA-PC-0300
REFERÊNCIA : P0Q27003	No DESENHO CLIENTE: -
	No DESENHO SAG: BR1045-UMA-&CLB010-102070
TAMANHO ORIGINAL A1	TÍTULO DO DESENHO: TURBINA A VAPOR - LEIAUTE E DETALHES *ST AREA PILING, LAYOUT AND DETAILS* PLANTA GERAL
	FL. 02 PRÓX. 03

DIN A1 (841 x 594)