
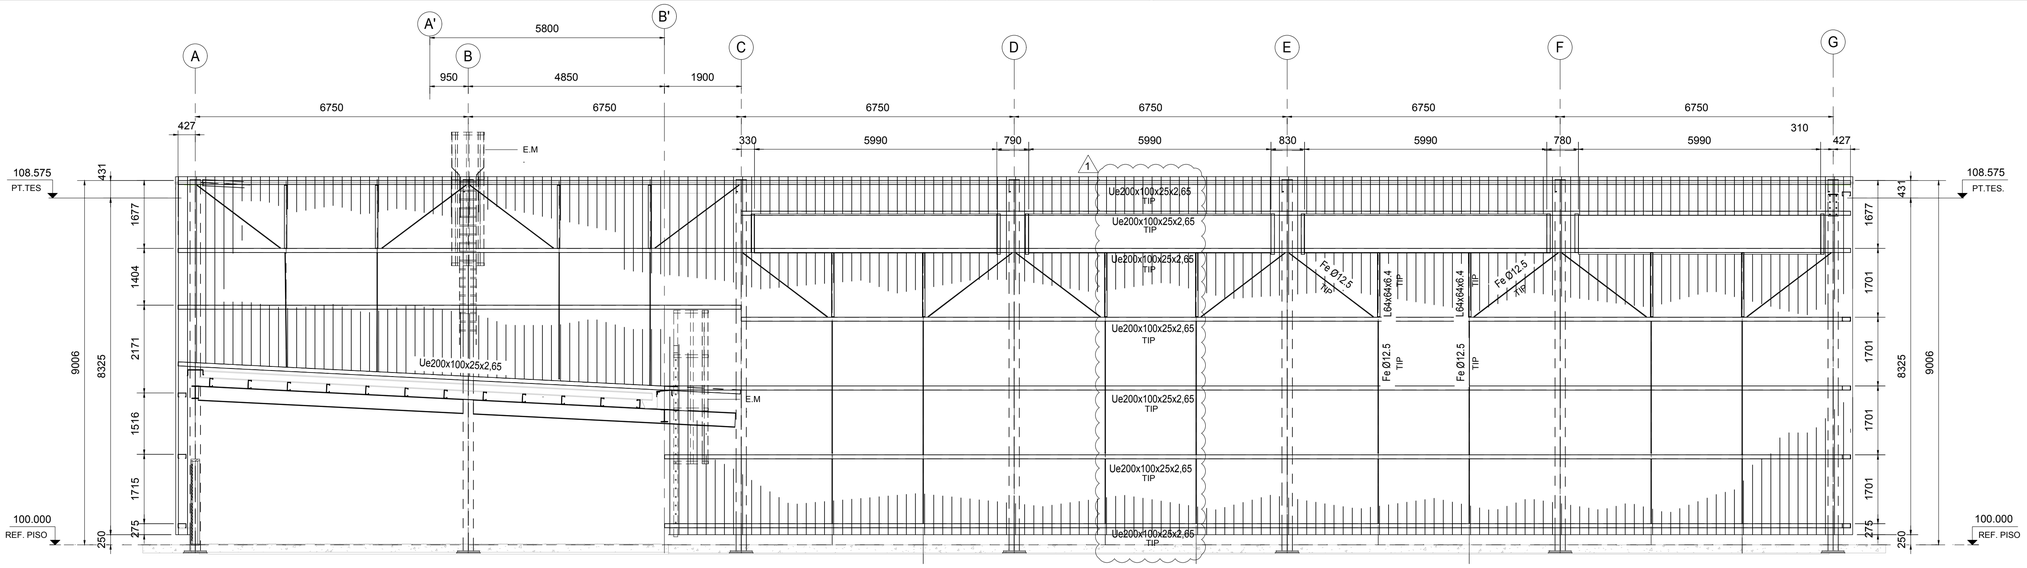


FECHAMENTO NO EIXO 8

ESCALA: 1 : 75

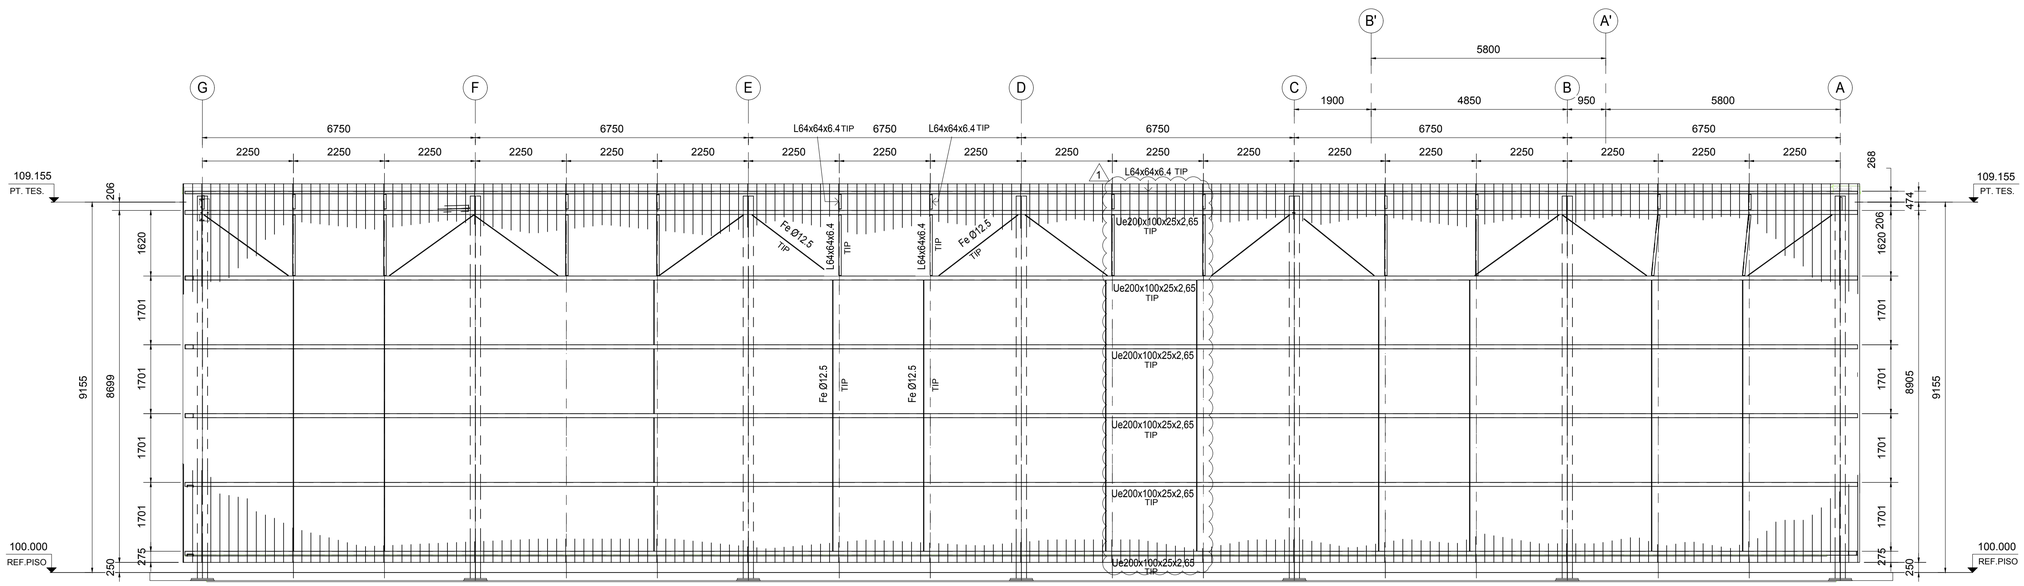

FECHAMENTO NO EIXO 10

ESCALA: 1 : 75

NOTAS

1- TODAS AS DIMENSÕES ESTÃO EM MILÍMETRO E ELEVAÇÕES EM METRO, SALVO INDICAÇÃO CONTRÁRIA.

2- PARA NOTAS GERAIS VER DESENHO: NOVO-SRCA-PC-0805-01.

REV.	DESCRIÇÃO	DATA	DES.	VERIF.	APROV.
1	REV. ONDE INDICADO/APROVADO P/ CONSTRUÇÃO	10/08/18	O.J.S.	M.P.R.	E.R.P.
0	EMISSÃO INICIAL/APROV. PARA CONSTRUÇÃO - AFC	28/04/18	G.F.A.	M.P.R.	E.R.P.

REVISÕES

CONTRATANTE: SIEMENS / AG ANDRADE GUTIERREZ CONSÓRCIO ACU

ENGENHARIA SUBCONTRATADA: SENER

CLIENTE: **UTE GNA I** Gás Natural Açu S.A.

© SENER SETEPLA TECNOMETAL ENGENHARIA E SISTEMAS S.A.
AS INFORMAÇÕES CONTIDAS NESTE DOCUMENTO SÃO CONFIDENCIAIS E RESTRITAS, E DEVEM SER UTILIZADAS SOMENTE PARA FINS ESTABELECIDOS NO DOCUMENTO. MODIFICAÇÃO, EXPLORAÇÃO, REPRODUÇÃO, COMUNICAÇÃO À QUALQUER TERCEIRO, EXPOSIÇÃO OU DISTRIBUIÇÃO DE TODO OU QUALQUER PARTE DO DOCUMENTO NÃO É PERMITIDO SEM O CONSENTIMENTO PRÉVIO POR ESCRITO DA SENER SETEPLA TECNOMETAL ENGENHARIA E SISTEMAS S.A. A FALTA DE RETORNO SOBRE TAL CONSENTIMENTO NÃO DEVE, EM HIPÓTESE ALGUMA, SER INTERPRETADA COMO AUTORIZAÇÃO PARA USO DA INFORMAÇÃO.

No ARQUIVO CAD :	NOVO-SRCA-PC-0805 -09 Rev 1
ESCALA :	INDICADA
REFERÊNCIA :	P0Q27003
TAMANHO ORIGINAL	A1
PROJETO:	UTE GNA I PLANTA DE CICLO COMBINADO PORTO DO AÇU - RIO DE JANEIRO
No DESENHO SUBCONTRATADA	NOVO-SRCA-PC-0805
No DESENHO CLIENTE:	
No DESENHO SIEMENS:	BR1045-31910-&CLC030-102195
TÍTULO DO DESENHO:	OFICINA / ALMOXARIFADO - ESTR. METÁLICA *WORKSHOP WAREHOUSE BUILDING STRUCTURE* FECHAMENTOS NOS EIXOS 8 e 10
FL.	09
PRÓX.	10

0 100 200 300 mm

DIN A1 (841 x 594)