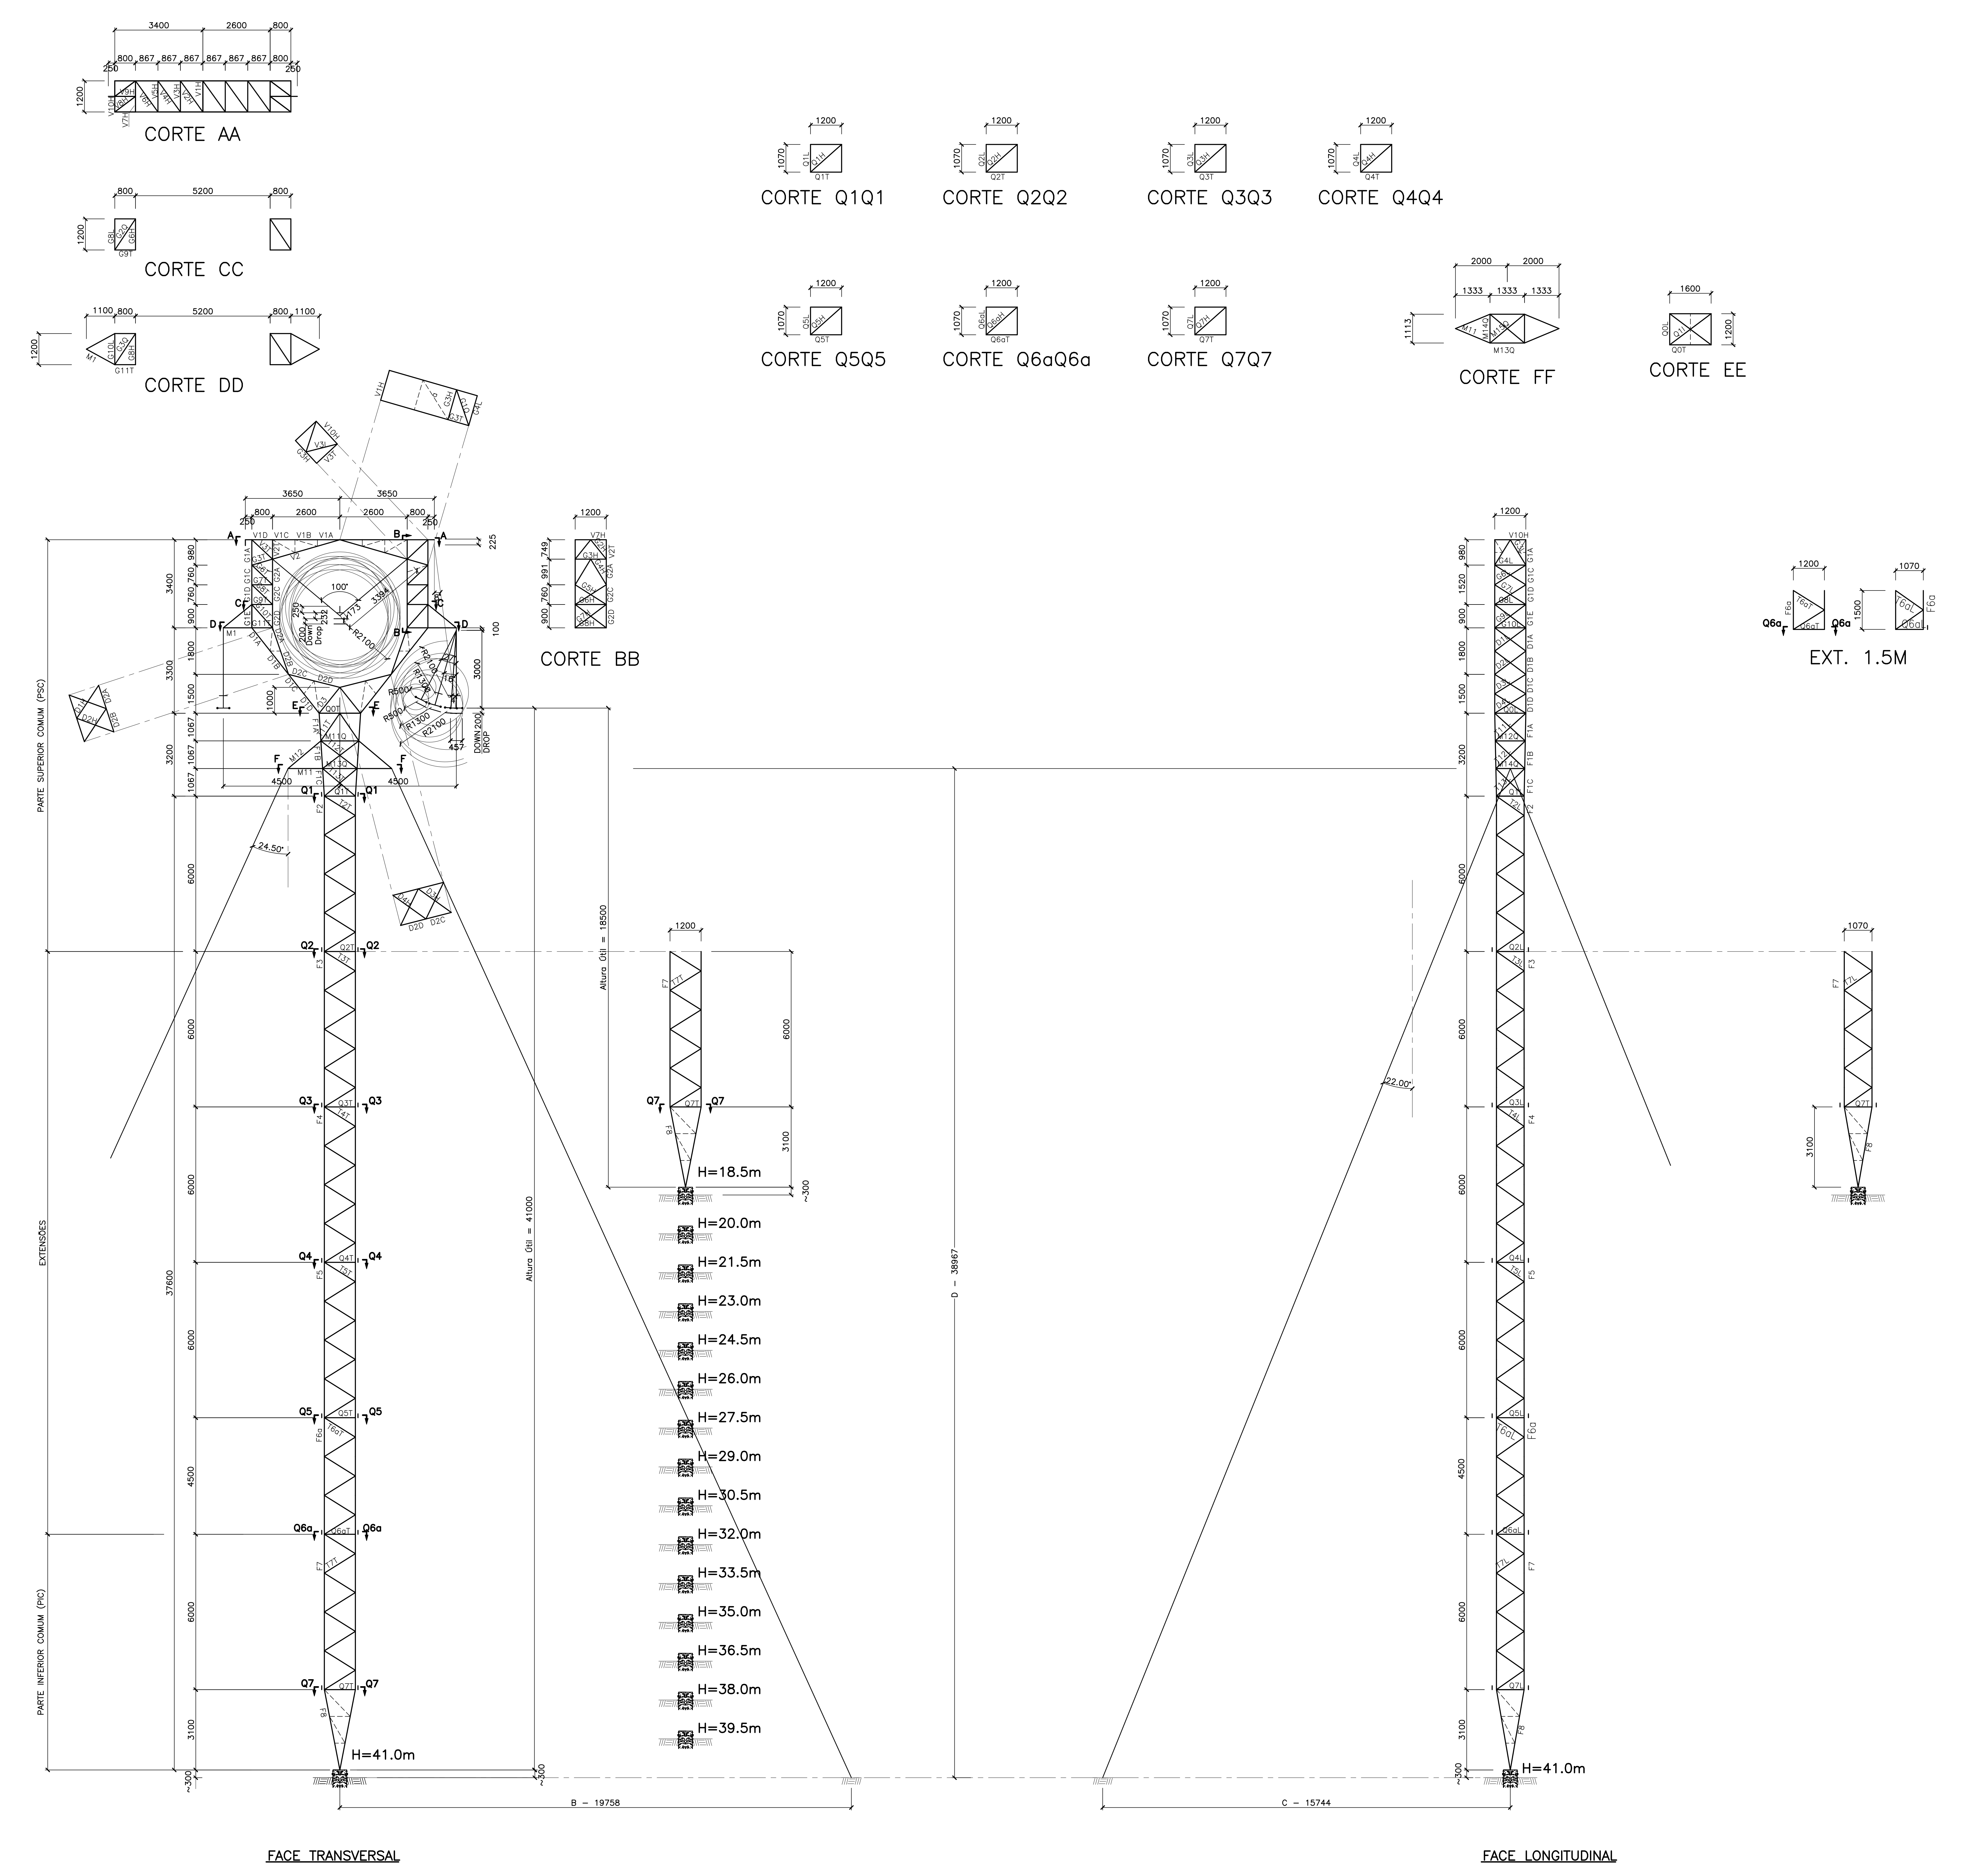

FACE TRANSVERSAL

FACE LONGITUDINAL

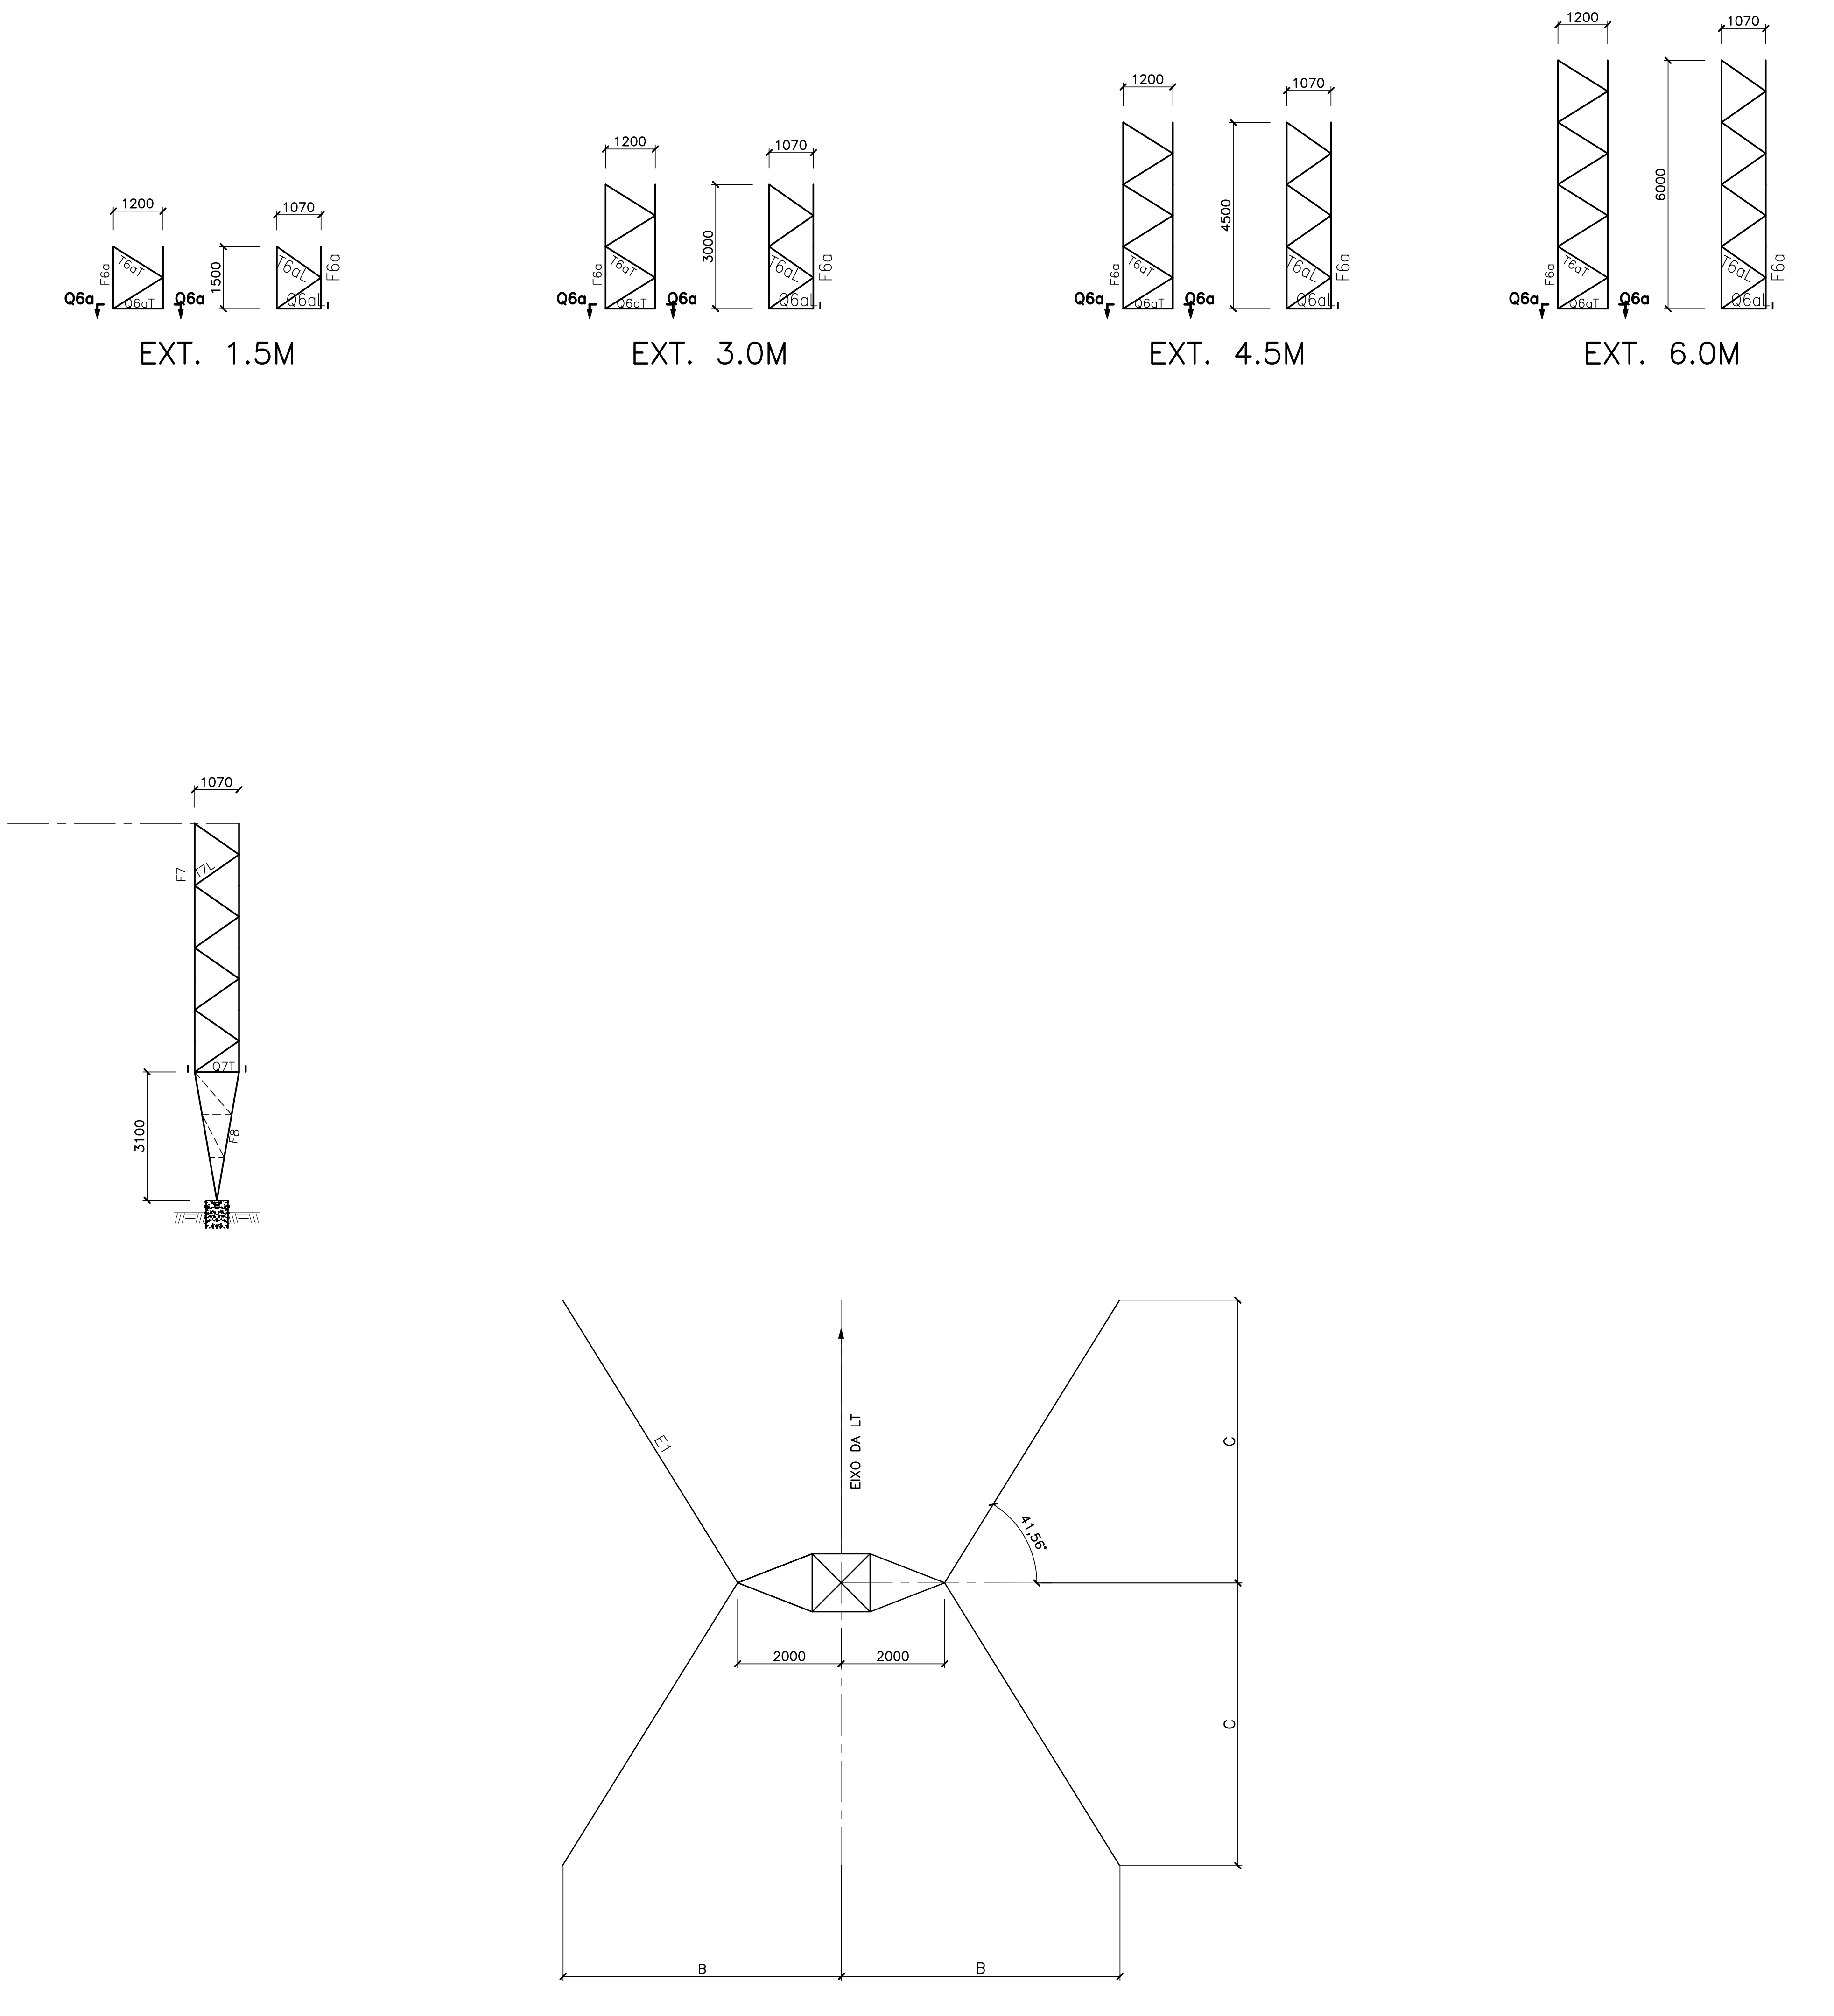

Altura Útil (m)	Composição das Estruturas	Locação Estai - solo (mm)		
		B	C	D
18.5	PSC + PIC	9504	6653	16467
20.0	PSC + F6a(Ext. 1.50m) + PIC	10188	7259	17967
21.5	PSC + F6a(Ext. 3.00m) + PIC	10871	7865	19467
23.0	PSC + F6a(Ext. 4.50m) + PIC	11555	8471	20967
24.5	PSC + F3(Ext. 6.00m) + PIC	12239	9077	22467
26.0	PSC + F3(Ext. 6.00m) + F6a(Ext. 1.50m) + PIC	12922	9683	23967
27.5	PSC + F3(Ext. 6.00m) + F6a(Ext. 3.00m) + PIC	13606	10289	25467
29.0	PSC + F3(Ext. 6.00m) + F6a(Ext. 4.50m) + PIC	14289	10895	26967
30.5	PSC + 2 x F3/F4(Ext. 6.00m) + PIC	14973	11501	28467
32.0	PSC + 2 x F3/F4(Ext. 6.00m) + F6a(Ext. 1.50m) + PIC	15657	12107	29967
33.5	PSC + 2 x F3/F4(Ext. 6.00m) + F6a(Ext. 3.00m) + PIC	16340	12713	31467
35.0	PSC + 2 x F3/F4(Ext. 6.00m) + F6a(Ext. 4.50m) + PIC	17024	13319	32967
36.5	PSC + 3 x F3/F4/F5(Ext. 6.00m) + PIC	17707	13925	34467
38.0	PSC + 3 x F3/F4/F5(Ext. 6.00m) + F6a(Ext. 1.50m) + PIC	18391	14531	35967
39.5	PSC + 3 x F3/F4/F5(Ext. 6.00m) + F6a(Ext. 3.00m) + PIC	19075	15138	37467
41.0	PSC + 3 x F3/F4/F5(Ext. 6.00m) + F6a(Ext. 4.50m) + PIC	19758	15744	38967

1. Todas as cotas estão em milímetro.
2. Estais E1 (para todas as alturas): Cordoalha 19 fios galvanizados 11/16", EHS – Ruptura mínima = 25000 kgf.
3. Barras descarregadas:
   Não indicadas: L40x40x3,0H – 1ø12.0
   a) L45x45x3,0H – 1ø12.0
   b) L50x50x3,0H – 1ø12.0
4. Para memória de cálculo ver doc. BNEL_ADR2451-M1001.

NOTAS

NÚMERO	TÍTULO
N°_DO_DOCUMENTO	TÍTULO DO DOCUMENTO DE REFERÊNCIA

DOCUMENTOS DE REFERÊNCIA

REV.	DESCRIÇÃO	DATA	ELABORAÇÃO	VERIFICAÇÃO
00	APROVADO	17/09/24	LETÍCIA PENIDO	RANIA PEIXOTO
00C	MÍSULA E CADEIA DOS CONDUTORES DESLOCADA 250mm	14/08/24	ARTHUR ALMEIDA	RANIA PEIXOTO
00B	CONFORME COMENTÁRIOS	25/07/24	MICHAEL RODRIGUES	RANIA PEIXOTO
00A	EMISSÃO INICIAL	28/06/24	MICHAEL RODRIGUES	RANIA PEIXOTO

N° CR GONTIJO
BNEL_ADR2451-D1001

PROPRIEDADE
Eletrobras
SPE Nova Era Integração Transmissora S.A.

AUTORIA
CONSAG CONSÓRCIO CONSTRUTOR SÃO FRANCISCO
CR GONTIJO ENGENHARIA DE PROJETOS

APROVAÇÃO
HENRIQUE GONTIJO
RESPONSÁVEL TÉCNICO
CREA 108382/MG

RESPONSÁVEL TÉCNICO

LOTE 05 – ANEEL 01/2024

DESCRIÇÃO DESENHO
TORRE DE SUSPENSÃO ESTAIADA DA ESTRUTURA TÍPICA BNEL
SILHUETA

DESCRIÇÃO PROJETO
NOVA ERA INTEGRAÇÃO
LOTE 5 – LT 230 kV
BOM NOME – BOM NOME II C1 E C2

CÓDIGO PROJETO	FORMATO	N° DESENHO
LTNEI	A0	LTNEI.AC-230-PB-EM.DSN-5001

CLASSIFICAÇÃO	ESCALA	FOLHA	REVISÃO
EXECUTIVO.BÁSICO.PADRÃO	1/100	1	00

PADRÃO DE IMPRESSÃO DETC.ctb		
COR CAD	ESPESSURA (mm)	COR IMPRESSÃO
1	0,1	7
2	0,2	7
3	0,3	7
4	0,4	7
5	0,5	7
6	0,6	7
7	0,15	7
8	0,1	7
9	0,05	7
11	0,05	7
41	0,05	7

AS DEMAIS CORES DEVEM SER IMPRESSAS EM SUAS RESPECTIVAS CORES COM ESPESSURA DE 0.20 mm.